


2251 SKODA CIRCUIT

POINTCOOK

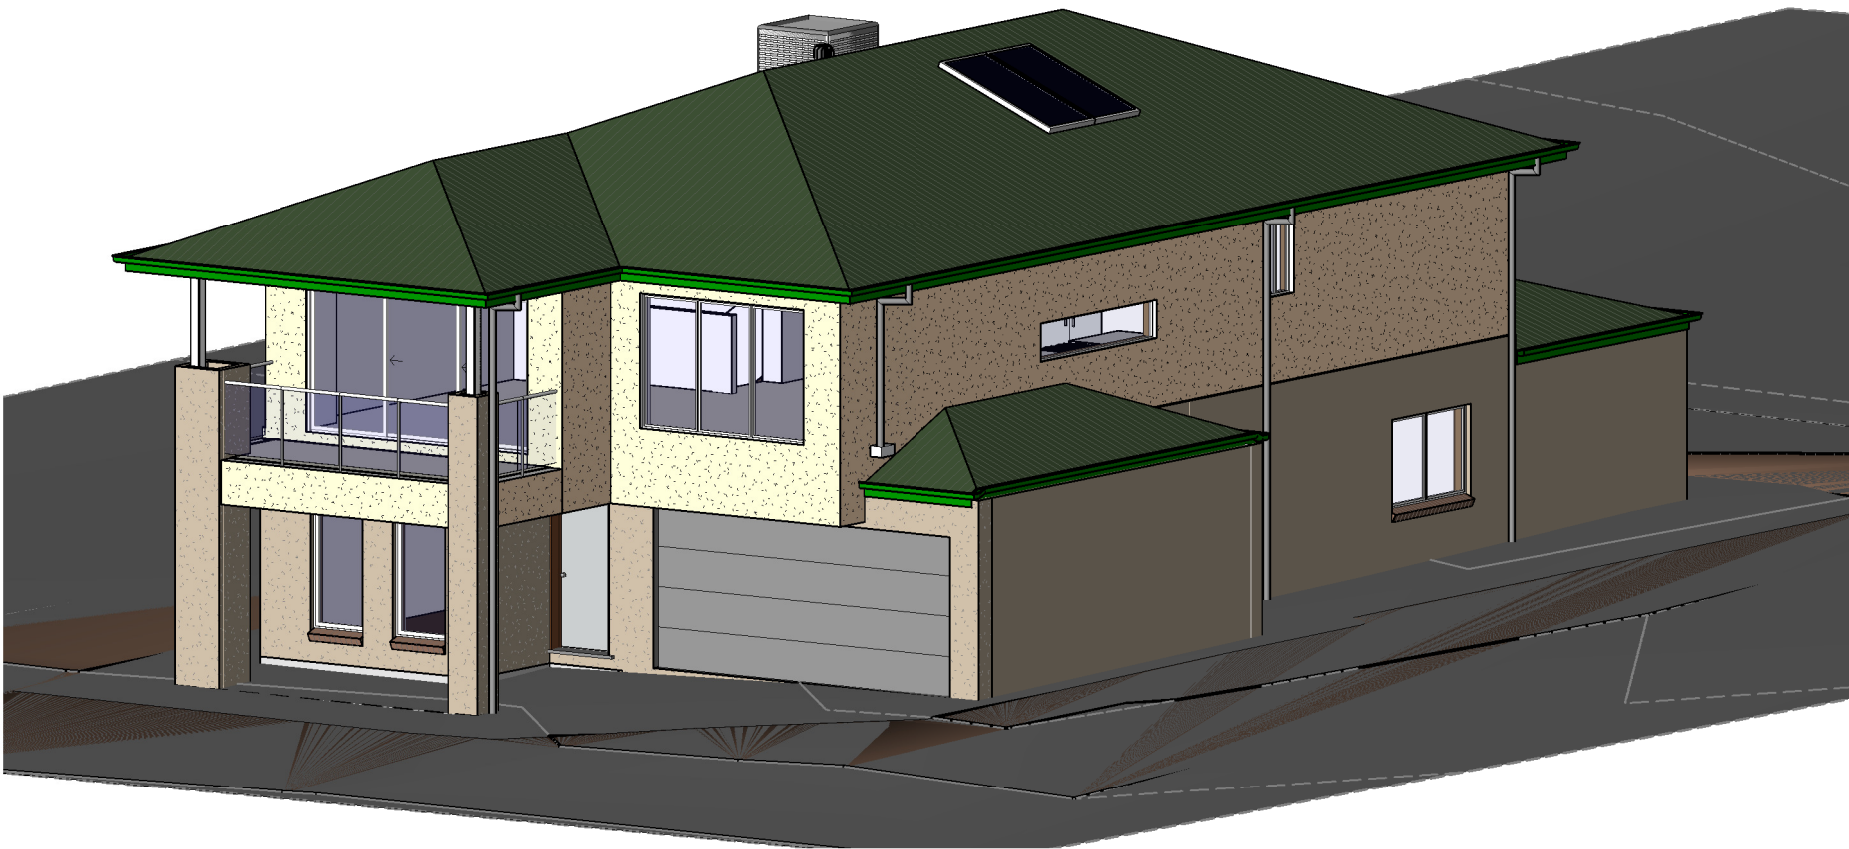

SHEET NO	DESCRIPTION
1.1	FACE SHEET & INDEX
1.2	GENERAL NOTES
2.1	SITE PLAN
3.1	PLAN - GROUND FLOOR
3.2	PLAN - FIRST FLOOR
4.1	ELEVATIONS A & B
4.2	ELEVATIONS C & D
5.1	ELECTRICAL - GROUND FLOOR
5.2	ELECTRICAL - FIRST FLOOR
6.1	FLOORING - GROUND FLOOR
6.2	FLOORING - FIRST FLOOR
7.1	SECTIONS
7.2	STAIR DETAILS
7.3	BALCONY DETAILS
8.1	KITCHEN, LAUNDRY
8.2	BATH, ENS1 & PDR
8.3	WC & TYPICAL
9.1	LANDSCAPE PLAN
10.1	SLAB LAYOUT
10.2	OVERLOOKING DIAGRAMS
11.1	SHADOW DIAGRAM - 9AM
11.2	SHADOW DIAGRAM - 10AM
11.3	SHADOW DIAGRAM - 11AM
11.4	SHADOW DIAGRAM - 12PM
11.5	SHADOW DIAGRAM - 1PM
11.6	SHADOW DIAGRAM - 2PM
11.7	SHADOW DIAGRAM - 3PM

GRAPHICAL PRESENTATION ONLY

 ISLANDER	Long Island Homes Pty. Ltd. PO BOX 6269 Point Cook, Vic 3030 p. 61 3 9369 6486 (1800 604 011) f. 61 3 9369 0994 email: admin@longislandhomes.com.au www.longislandhomes.com.au © Copyright THIS DESIGN & DRAWING SHALL REMAIN THE INTELLECTUAL PROPERTY OF LONG ISLAND HOMES PTY. LTD. AND SHALL NOT BE COPIED IN WHOLE OR PART WITHOUT WRITTEN CONSENT FROM LONG ISLAND HOMES PTY LTD. DB NUMBER	GENERAL NOTES: - THE CONTRACTOR IS RESPONSIBLE FOR SETTING OUT AND CHECKING ALL LEVELS AND DIMENSIONS ON SITE PRIOR TO COMMENCING ANY SITE WORKS. - FIGURED DIMENSIONS ARE TO TAKE PREFERENCE OVER SCALE - DIMENSIONS TO STRUCTURAL TIMBERS & FACE OF BRICKS EXCLUDING BATTENS, PLASTERBOARD ETC. - ALL DIMENSIONS ON PLAN ARE NOMINAL & MAY VARY TO ACTUAL SIZE - PROVIDE LOCKS TO ALL OPENABLE WINDOWS & EXTERNAL SLIDING DOORS (KEYED ALIKE). - MAN HOLE LOCATION MAY BE CHANGED DUE TO TRUSS LAYOUT. - WINDOW AND DOOR FRAME SIZES ARE NOMINAL AND MAY VARY WITH LONG ISLAND HOMES APPROVED SUPPLIERS.	CLIENT		SHEET CONTENT: FACE SHEET & INDEX		NORTH:	FACADE:	SCALE:	DATE:	SHEET NUMBER: 1.1	JOB NUMBER: H	
			I / WE.....		HOUSE TYPE: SANYA 380								MIN LOT WIDTH: 12M
			SIGN OFF		CONFIRM THESE DRAWINGS ACCORD WITH OUR REQUIREMENTS AND AUTHORISE THEIR USE FOR NEXT STAGE PURPOSES.		PROPERTY ADDRESS: 2251 SKODA CIRCUIT POINTCOOK		REVISIONS	ISSUE	DATE	REVISION DESCRIPTION	INITIALS
					SIGNED..... DATE.....		CLIENT: CLARE FRANSIS & CHRISTPHER KEVIN GRIFFITHS						
		SIGNED..... DATE.....											

27/10/2021 8:44:48 AM J:\LONG ISLAND JOBS\2251 Skoda Circuit, Point Cook\DRAWING\2251SKO_REV.H.rvt

GENERAL NOTES.

DO NOT SCALE DRAWINGS. USE WRITTEN DIMENSIONS ONLY.

THE OWNER, BUILDER AND/OR SUB-CONTRACTORS SHALL VERIFY ALL DIMENSIONS, LEVELS, SETBACKS AND ANY SPECIFICATIONS PRIOR TO COMMENCING ANY WORKS OR ORDERING MATERIALS AND SHALL BE RESPONSIBLE FOR ENSURING THAT ALL BUILDING WORKS CONFORM TO THE BUILDING CODE OF AUSTRALIA, AUSTRALIAN STANDARDS CODES (CURRENT EDITIONS), BUILDING REGULATIONS, LOCAL BY-LAWS AND RESCODE REQUIREMENTS. REPORT ALL DISCREPANCIES TO THIS OFFICE FOR CLARIFICATION.

- THESE PLANS SHALL BE READ IN CONJUNCTION WITH ANY STRUCTURAL OR CIVIL ENGINEERING COMPUTATIONS AND DRAWINGS.

THESE PLANS SHALL BE READ IN CONJUNCTION WITH THE SOIL REPORT. FOOTINGS ARE TO BE FOUNDED AT THE MINIMUM DEPTHS INDICATED I THE SOIL REPORT.

WHERE THE BUILDING (OTHER THAN A CLASS 10a) IS LOCATED IN A DESIGNATED TERMITE INFESTATION AREA THE BUILDING SHALL BE PROTECTED IN ACCORDANCE WITH THE RELEVANT AUSTRALIAN STANDARDS.

- STORMWATER SHALL BE TAKEN TO THE LEGAL POINT OF DISCHARGE TO THE SATISFACTION OF THE RELEVANT AUTHORITY.

SEWER OR SEPTIC SYSTEMS SHALL BE IN ACCORDANCE WITH THE RELEVANT AUTHORITY REQUIREMENTS.

- FOOTINGS ARE NOT TO ENCROACH OVER ANY TITLE BOUNDARIES AND/OR EASEMENT LINES.

FOR BUILDINGS IN CLOSE PROXIMITY TO THE SEA ENSURE THAT ALL STEELWORK, BRICK CAVITY TIES, STEEL LINTELS ETC. THAT ARE IMBEDDED OR FIXED TO MASONRY BE PROTECTED IN ACCORDANCE WITH A.S. 3700-2001 (TABLE 2.2), HOT DIP GALVANIZED, STAINLESS STEEL OR CADMIUM COATED.

BUILDING SETBACKS ARE FROM TITLE LINE (NOT FENCE LINE) REFER TITLE RE-ESTABLISHMENT PLAN FOR CORRECT OFF SETS IN RELATION TO FENCE LINES

- ALL WET AREAS ARE TO COMPLY WITH B.C.A. 3.8.1 OR A.S. 3740-2004. WALL FINISHES SHALL BE IMPERVIOUS TO A HEIGHT OF 1800MM ABOVE FLOOR LEVEL TO ANY SHOWER ENCLOSURES AND 150MM ABOVE BATHS, BASINS, SINKS AND TROUGHS IF WITHIN 75MM OF THE WALL.

RISERS ~190MM MAXIMUM, 115MM MINIMUM. GOING ~355MM MAXIMUM, 240MM MINIMUM. RISERS AND TREADS ARE TO BE CONSTANT IN SIZE THRU-OUT FLIGHT. PROVIDE NON-SLIP FINISH OR SUITABLE NON-SKID STRIP NEAR EDGE OF NOSING.

- ENSURE A MAXIMUM GAP BETWEEN RISERS IS NOT TO EXCEED 125MM OR USE CLOSED RISERS. PROVIDE CONTINUOUS HAND RAILING 1000MM MINIMUM HEIGHT TO BALCONIES AND DECKS WHICH ARE 1000MM OR GREATER ABOVE GROUND LEVEL. HANDRAILS ARE TO BE A MINIMUM OF 865MM ABOVE STAIR NOSINGS AND LANDINGS. MAXIMUM GAP BETWEEN BALUSTERS SHALL BE 125MM.

- SMOKE ALARMS ARE TO BE PROVIDED AND INSTALLED IN ACCORDANCE WITH A.S. 3786-1993, AND UNLESS INSTALLED IN AN EXISTING PART OF A CLASS 1, 2 OR 3 BUILDING OR A CLASS 4 PART OF A BUILDING THE SMOKE ALARM SHALL BE HARD-WIRED WITH A BATTERY BACK-UP INTERCONNECTED.

SPECIFICATION NOTES:

BRICKWORK:

PROVIDE WALL-TIES TO BRICKWORK AT A MAXIMUM OF 600MM IN EACH DIRECTION AND WITHIN 300MM OF ANY ARTICULATION JOINTS. FOR PERPS AND BEDS JOINTS SPACINGS (REFER TO BCA PART 3.3.1)

TIMBER FRAMING:

ALL TIMBER FRAMING THRU-OUT IS TO BE IN ACCORDANCE WITH A.S. 1684 AND ALSO READ IN CONJUNCTION WITH THE ENGINEERS DETAILS AND DRAWINGS.

FLOORING & FOOTINGS:

FINISHED FLOOR LEVELS ARE NOMINAL ONLY AND SHOULD BE CONFIRMED PRIOR TO START OF WORK.

READ IN ACCORDANCE WITH THE SOIL REPORT REQUIREMENTS. READ IN CONJUNCTION WITH THE ENGINEERS DETAILS FOR ALL FOOTING SIZE & DETAILS.

PLEASE NOTE MINIMUM FOUNDING DEPTH TO BE DETERMINED AS "NOTED" IN THE SOIL REPORT

WALL LINTELS & SUPPORT STUDS THRU-OUT:

FOR ALL EXTERNAL PERIMETER LOAD-BEARING LINTELS AND THEIR SUPPORTING STUDS REFER TO THE ENGINEERS DETAILS AND DRAWINGS AND TO GENERAL SPECIFICATIONS

CARPENTERS TO ALLOW 45MM DOOR STUD AT WALL JUNCTIONS

INTERNAL DOORS:

ALL INTERNAL DOORS ARE TO BE 2040mm HIGH UNLESS NOTED OTHERWISE ON THE PLAN.

WC DOORS:

HINGED DOORS THAT OPEN INWARDS TOWARDS THE PAN BUT THE EDGE OF THE DOOR IS A MINIMUM OF 1200MM AWAY FROM THE PAN AT ITS NEAREST POINT, MUST HAVE DEMOUNTABLE HINGES TO ALLOW EASY REMOVAL OF THE DOOR FROM THE OUTSIDE THE WC COMPARTMENT.

ROOFING:

CONCRETE TILED ROOF OVER ROOF BATTENS AT 330 CTRS. TYPICAL THRU-OUT UNLESS NOTED OTHERWISE.
METAL EITHER TIMBER OR METAL BATTENS TO BE USED & FIXED IN ACCORDANCE WITH THE MANUFACTURERS DETAILS & SPECIFICATIONS & PROVIDE APPROVED CAPPING & FLASHING THRU-OUT.

SELECTED TIMBER FRAMED ROOF TRUSS AT 600mm MAX CTRS. TO MANUFACTURERS SPECIFICATIONS UNLESS NOTED OTHERWISE.

PLASTERBOARD LINED CEILINGS THRU-OUT.

SELECTED PROFILE METAL EAVES GUTTER & FASCIA TO THE PERIMETER OF THE ROOF AREA.

ALSO READ IN CONJUNCTION WITH ANY ENGINEERS DETAILS & DRAWINGS FOR ANY ROOF BEAMS, LINTELS, ETC.

4.5mm THICK F.C. SHEET CEILING LINING TO THE UNDERSIDE OF THE FIRST FLOOR EAVES.

LINTEL NOTES:

BUILDER IS TO NOTE THAT LINTELS SELECTED BY THE ENGINEER ARE DESIGNED TO CARRY ONLY STANDARD TILE ROOFING & TRUSS LOADS WHERE ARE AT 600mm MAXIMUM CTRS. IF ANY GIRDER TRUSSES ARE LOCATED DIRECTLY ON ANY LINTELS.

TRUSS MANUFACTURER AND / OR BUILDER IS TO REFER TO THE ENGINEER TO CONFIRM IF LINTEL & SUPPORTING STUDS ARE ADEQUATE.

ENGINEER'S DRAWINGS TAKE PRECEDENCE OVER NOMINAL SIZES INDICATED ON THESE PLANS.

WINDOWS:

ALL GLAZING SHALL CONFORM TO AS1288-2006.
WINDOW SIZES SHOWN ARE NOMINAL DEPENDING ON THE WINDOW MANUFACTURERS CLOSEST STANDARD SPECIFICATIONS.

- ALL GLAZING IS TO BE IN ACCORDANCE WITH AS1228-2006.
- READ IN CONJUNCTION WITH THE WINDOW SCHEDULE & ELEVATIONS.
- ALL EXTERNAL DOORS ARE TO FITTED WITH WEATHER STRIPS.
- 'F' DENOTES FIXED GLAZING, 'D' DENOTES OPENABLE SASH.

NOTE: THESE HEIGHTS MAY VARY SLIGHTLY ACCORDING TO DIFFERENCES IN BRICK SIZES.

WALLING:

90mm WIDE STUD FRAME WALLS THRU-OUT
MGP10 GRADE
90x35 COMMON STUDS
70x35 NOGGINGS
2(90x35) TOP PLATES
2(90x45) JAMB STUDS

LININGS:

10mm PLASTERBOARD TO ALL INTERNAL WALLS.
10mm PLASTERBOARD TO CEILINGS.
SELECTED WATER RESISTANT SUB-STRATE & TILING TO WE AREAS.

HEATING & COOLING:

ALL HEATING & COOLING UNITS, SIZES, TYPES & LOCATIONS ARE TO BE CONFIRMED BETWEEN THE BUILDER & THE SUPPLIER.

ALL HEATING & COOLING DUCTS & VENT LOCATIONS ARE TO BE CONFIRMED BY THE BUILDER PRIOR TO COMMENCEMENT OF BUILDING TO DETERMINE IF ANY ADDITIONAL RISER DUCTS ARE REQUIRED.

ALL HEATING & COOLING POINTS LOCATIONS, MAY VARY FROM PLAN TO PLAN.

GEOTECHNICAL:

THESE DRAWINGS ARE TO BE READ IN CONJUNCTION WITH A GEOTECHNICAL REPORT. IT IS THE BUILDERS'S RESPONSIBILITY TO OBTAIN SUCH REPORTS PRIOR TO COMMENCEMENT OF WORKS.

FULL HEIGHT CONTROL JOINTS (FOOTING TO EAVES) AT 5m MAX CTRS UNLESS OTHERWISE STATED IN THE SOIL REPORT.

REFER TO SOIL REPORT.

PAINTWORK:

PROVIDE THREE COAT PAINT SYSTEM INTERNALLY, BASED ON ONE WALL COLOUR THROUGHOUT AND ONE CEILING COLOUR THROUGHOUT.

6 STAR ENERGY UPGRADE:

- ALL EXTERNAL GAPS & CRACKS TO WINDOW/DOOR FRAMES SEALED ON CONSTRUCTION.
- SISALATION APPLIED TO ALL WALLS, & GAPS/JOINS SEALED.
- SELF CLOSING EXHAUST FANS THROUGHOUT OR 'DRAFT STOPPER' SHROUDS OVER EXHAUST FANS.
- WEATHER STRIPS/SEALS TO ALL EXTERNAL HINGED DOORS AND INTERNAL GARAGE ACCESS DOOR.
- ALL CHIMNEYS FITTED WITH DAMPERS.
- ALL DOWNLIGHTS OF "CLOSED-RING" TYPE.
- INSULATION LEVELS AS DETAILED IN ATTACHED ENERGY RATING ASSESSOR'S REPORT.

LINTEL SCHEDULE

MEMBER SIZE	UPPER FLOOR & SINGLE STOREY	LOWER FLOOR (DOUBLE STOREY)
	MAX SIZE OF OPENING (mm)	MAX SIZE OF OPENING (mm)
90x45 F17	1000	800
140x45 F17	1400	1200
190x45 F17	1900	1600
240x45 F17	2400	2000
290x45 F17	2900	2400
190x45 F17	1900	1600
90x45 F17	1000 FRONT DOOR	800
90x45 F17	900 GARAGE REAR DOOR	800

SOIL CLASSIFICATION: "H2"

REPORT NO:	82315
BY:	INTRAX
DATE:	22/04/2021
B.A.L.:	LOW
WIND SPEED:	N-2

WALLING FRAME SIZES

EXTERNAL STUDS	450mm
INTERNAL STUDS	450mm

ENERGY REPORT - INSULATION

INSULATION TO BE INSTALLED TO THE FOLLOWING AREAS:	
CEILINGS (EXCLUDING GARAGE)	R 6.0
WALLS (EXCLUDING GARAGE EXTERNAL WALLS)	R 2.0 + SISALATION
FLOORS (FLOOR ABOVE PORCH, GARAGE & ALFRESCO)	R 4.1
INTERNAL BATH & LDRY WALLS	R 2.0
STANDARD INCLUSION FOR LONG ISLAND HOMES PROVIDE INSULATION TO: EXTERNAL DWELLING WALLS, WALL BETWEEN GARAGE AND HOUSE AND CEILING DIRECTLY UNDER ROOF SPACE EXCLUDED INSULATION TO GARAGE CEILING SPACE, GARAGE EXTERNAL WALLS AND GROUND FLOOR CEILING UNDER 1ST FLOOR OF DOUBLE STOREY HOMES.	
NOTE: WHERE SITE LEVELS ARE NOT AVAILABLE, THE BUILDER ASSUMES THE DWELLING SITS 200MM ABOVE N.G.L. FOR ENERGY REPORT PURPOSES.	
REQUIREMENTS ARE AS PER ENERGY REPORT - REF NO# 28IYHA27EF	
DATES	21/09/2021



ISLANDER

Long Island Homes Pty. Ltd.
PO BOX 6269
Point Cook, Vic 3030
p. 61 3 9369 6486 (1800 604 011)
f. 61 3 9369 0994
email: admin@longislandhomes.com.au
www.longislandhomes.com.au

© Copyright
THIS DESIGN & DRAWING SHALL REMAIN THE INTELLECTUAL PROPERTY OF LONG ISLAND HOMES PTY. LTD. AND SHALL NOT BE COPIED IN WHOLE OR PART WITHOUT WRITTEN CONSENT FROM LONG ISLAND HOMES PTY LTD.
DB NUMBER

GENERAL NOTES:

- THE CONTRACTOR IS RESPONSIBLE FOR SETTING OUT AND CHECKING ALL LEVELS AND DIMENSIONS ON SITE PRIOR TO COMMENCING ANY SITE WORKS.
- FIGURED DIMENSIONS ARE TO TAKE PREFERENCE OVER SCALE
- DIMENSIONS TO STRUCTURAL TIMBERS & FACE OF BRICKS EXCLUDING BATTENS, PLASTERBOARD ETC.
- ALL DIMENSIONS ON PLAN ARE NOMINAL & MAY VARY TO ACTUAL SIZE
- PROVIDE LOCKS TO ALL OPENABLE WINDOWS & EXTERNAL SLIDING DOORS (KEYED ALIKE).
- MAN HOLE LOCATION MAY BE CHANGED DUE TO TRUSS LAYOUT.
- WINDOW AND DOOR FRAME SIZES ARE NOMINAL AND MAY VARY WITH LONG ISLAND HOMES APPROVED SUPPLIERS.

CLIENT

I / WE.....

CONFIRM THESE DRAWINGS ACCORD WITH OUR REQUIREMENTS AND AUTHORISE THEIR USE FOR NEXT STAGE PURPOSES.

SIGNED..... DATE.....

SIGNED..... DATE.....

SHEET CONTENT:

GENERAL NOTES

HOUSE TYPE: SANYA 380

MIN LOT WIDTH: 12M

PROPERTY ADDRESS: 2251 SKODA CIRCUIT POINTCOOK

CLIENT:

CLARE FRANSIS & CHRISTPHER KEVIN GRIFFITHS

NORTH:

FACADE:

SCALE: 1 : 1

DATE:

REVISIONS

ISSUE	DATE	REVISION DESCRIPTION	INITIALS
A	19.04.21	MASTER	FT
B	29.07.21	R & C	CM
C	04.08.21	R & C ADD AREA	CM
D	20.09.21	COLOUR, PRE CONTRACT CLARIFICATION 06/09/21	CM
E	27.09.21	ENERGY UPGRADES (OPT 2) & CLARIFICATION 27.09.21	CM
F	27.09.21	WIR DOOR	CM
G	29.09.21	ADDED ENGINEERING	CM
H	27.10.21	CONTRACT QUOTE COMMENTS	CM

NOTE: SITE SCAPE
SCRAPE SITE TO REMOVE SURFACE VEGETATION AND PROVIDE LEVEL BUILDING PLATFORM. PROVIDE ADDITIONAL CUT TO GARAGE AREA TO ACCOMMODATE 86mm SLAB STEP DOWN.

NOTE: SITE CLEAR
LONG ISLAND HOMES REQUIRES THE SITE TO BE CLEAR OF ALL OBSTRUCTIONS, INCLUDING EXISTING SITE RUBBLE, EXISTING STRUCTURES, PAVING AND FENCING, PRIOR TO SITE START.

NOTE: BACK FILL
SITE TO BE BACK FILLED TO REBATE HEIGHT & FALL AWAY FROM DWELLING.

NOTE: DRIVEWAY GRADIENT
DRIVEWAY TO BE GRADED TO ENSURE MAXIMUM 1:6 GRADIENT FROM CROSSOVER TO GARAGE FLOOR.

NOTE: EASEMENTS
FOUNDATION MAYBE AFFECTED DUE TO PIPE DEPTH AND RESULTING ANGLE OF REPOSE CONSIDERATIONS.

NOTE: TERMITE PROTECTION
PROVIDE TERMITE TREATMENT IN ACCORDANCE WITH AS 3660.1

SITE SPECIFIC NOTES

NOTE: DRIVEWAY, PORCH & PATH
DRIVEWAY, PORCH & FRONT PATH TO BE CONSTRUCTED OF EXPOSED AGGREGATE, COMPLETED BY OWNER & TO COMPLY WITH RELEVANT DESIGN GUIDELINES.



NOTE: FENCING
SIDE, REAR & WING FENCE TO BE CONSTRUCTED AS PER DEVELOPERS GUIDELINES REQUIREMENTS & COMPLETED BY OWNER.

NOTE: AUTHORITY APPROVAL
SITING OF PROPOSED RESIDENCE IS SUBJECT TO APPROVAL BY DEVELOPER AND RELEVANT LOCAL AUTHORITY.

NOTE: FIBRE OPTIC ESTATE
THIS IS A FIBRE OPTIC ESTATE: ONT CONNECTION REQUIRED – BY OTHERS

NOTE: COROSION PROTECTION
PROVIDE CORROSION PROTECTION TO EXPOSED STEELWORK OF DOUBLE STOREY DWELLING WITH TILED ROOF, REQUIRED DUE TO PROXIMITY OF DWELLING TO THE OCEAN. PROVIDE CORROSION PROTECTION TO EXPOSED METAL ROOF.

NOTE: RAINWATER TANK
2000L RAINWATER TANK TO BE INSTALLED AND CONNECTED TO DWELLING AS PER THE DEVELOPERS GUIDELINES:
• CONNECTION OF WATER THANK TO ALL APPLICABELT TOILET SUITES.
• 1 x EXTERNAL TAP.

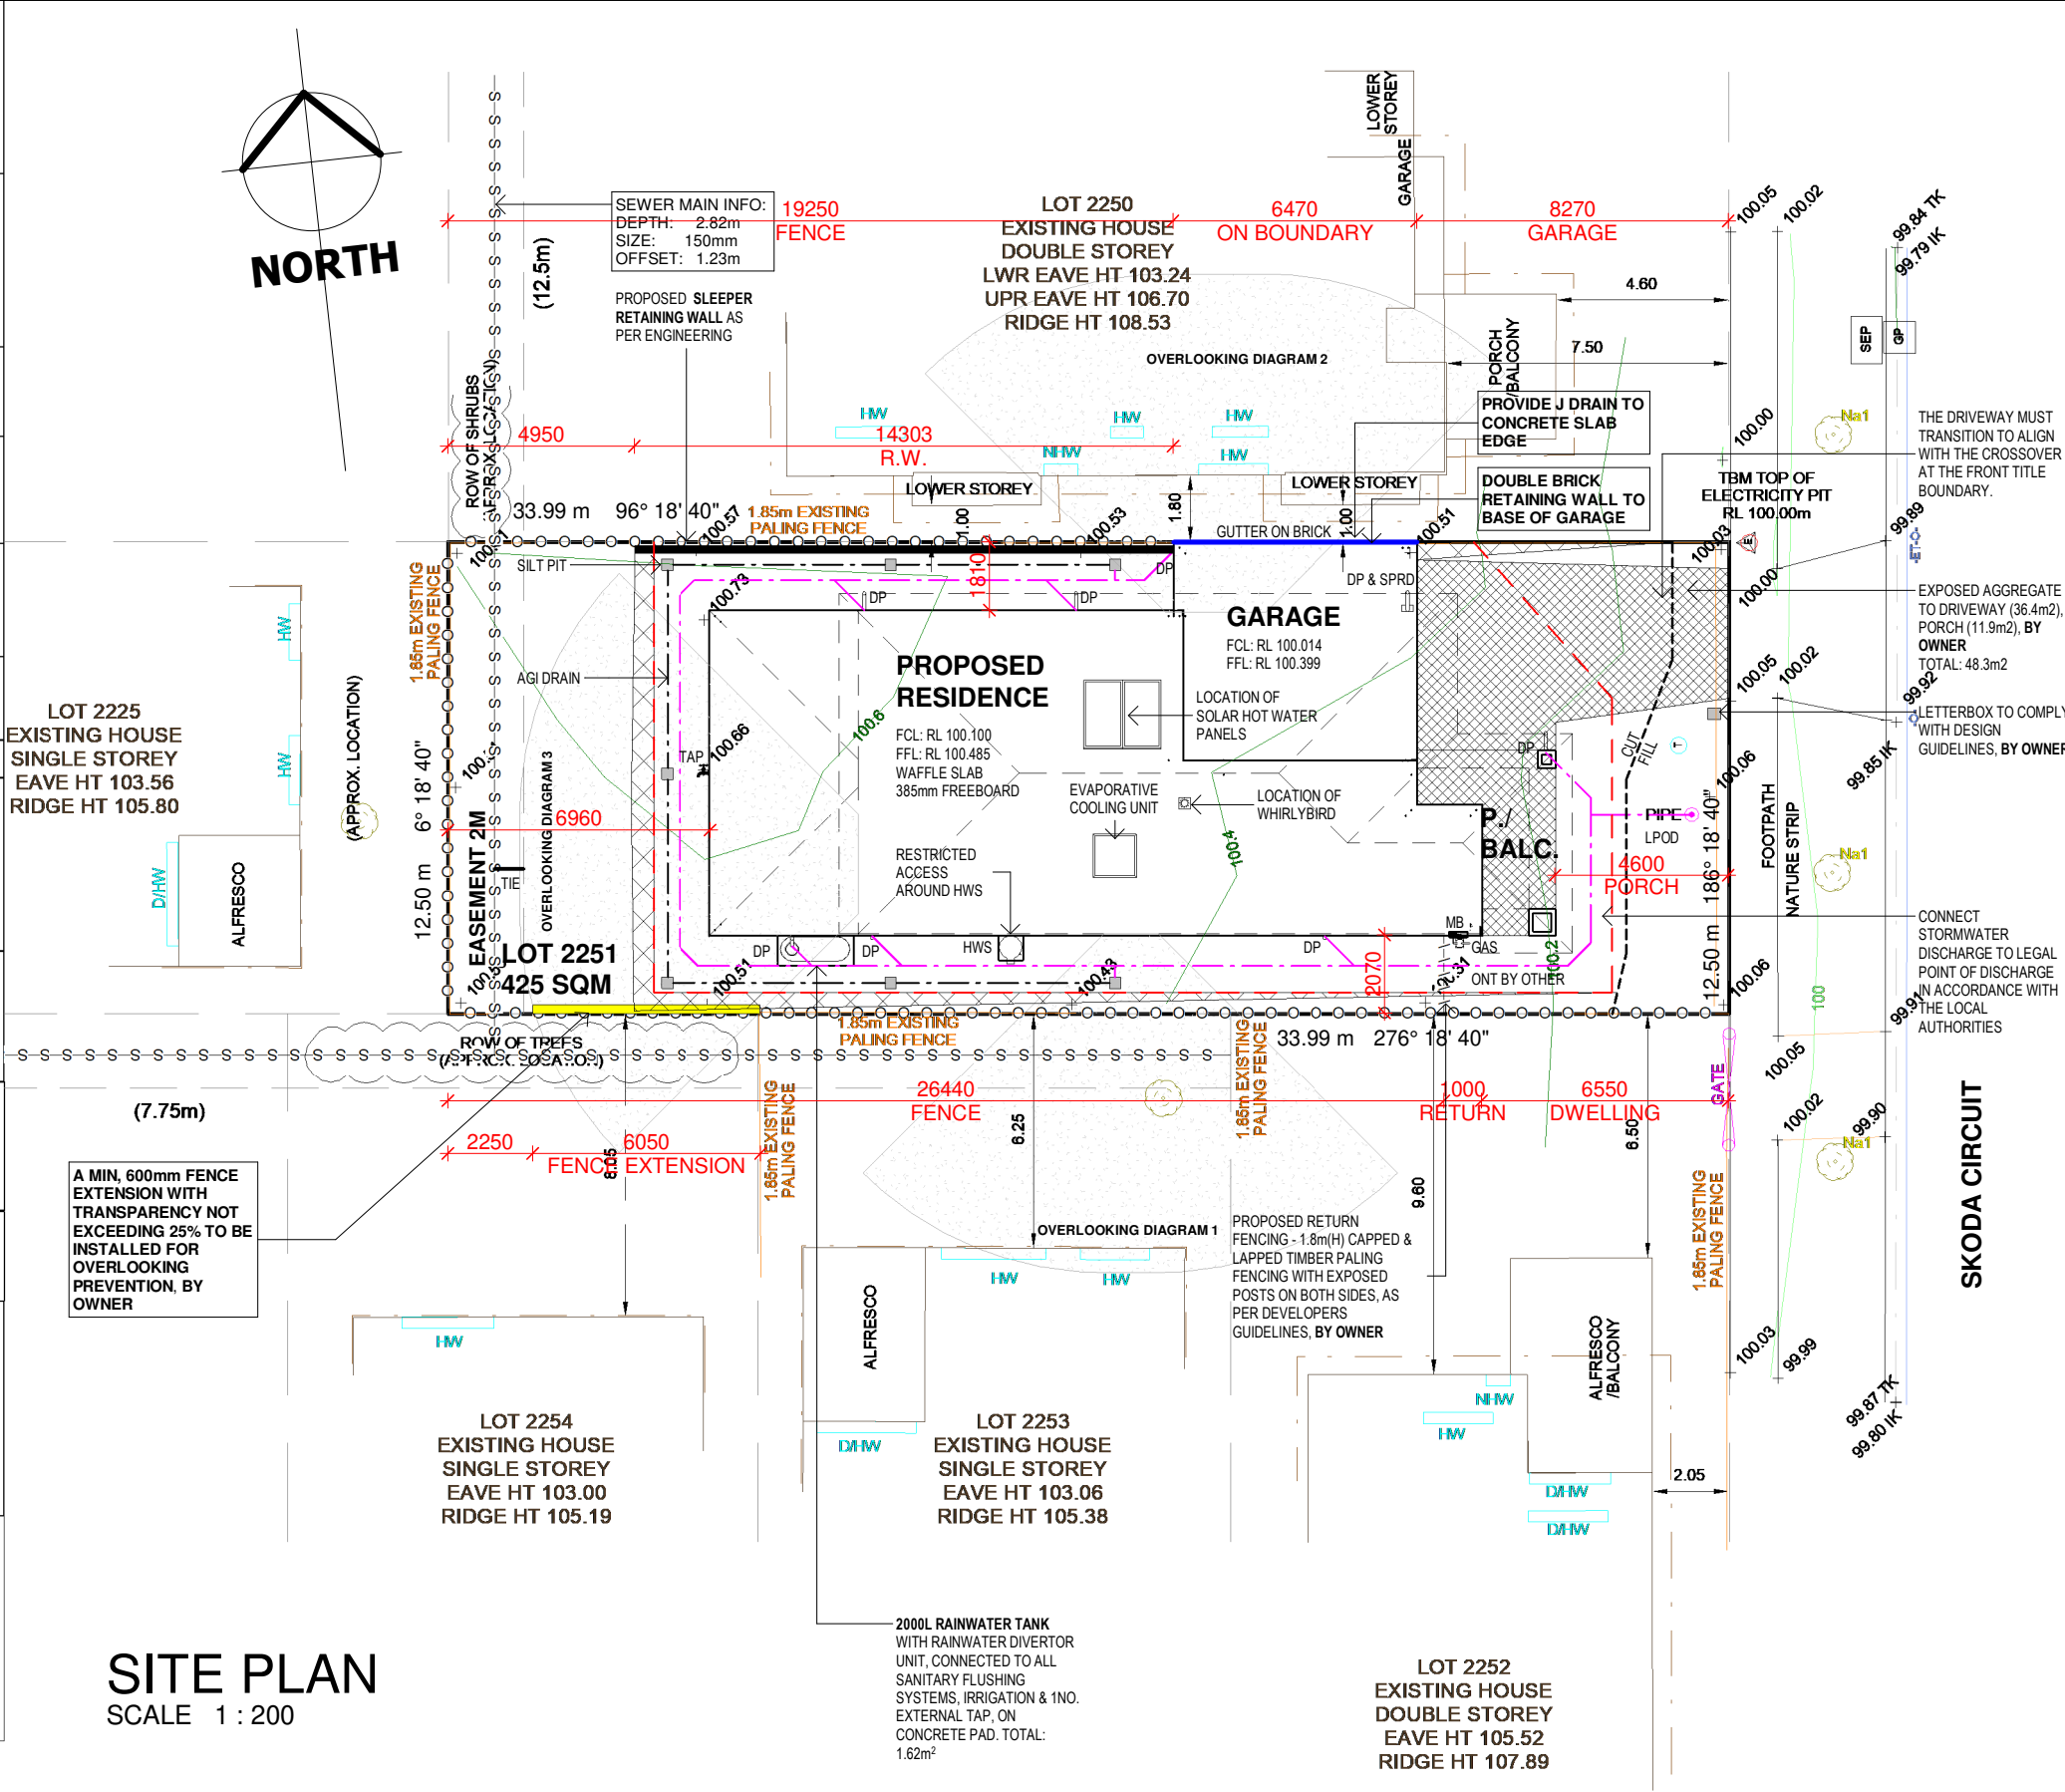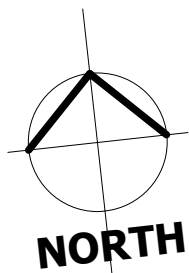

SITE PLAN
SCALE 1 : 200

LEGEND	
	- GAS METER
	- HOT WATER SYSTEM
	- METER BOX
	- TITLE PEG
	- SEWER VENT / I.S.
	- TELSTRA PIT
	- TREE
	- STREET SIGN
	- SEWER MANHOLE
	- ELECT. PIT
	- ELEC. POLE
	- SIDE ENTRY PIT
	- WATER VALVE
	- S/W PROPERTY INLET
	- WATER METER
	- STORM WATER PIT
	- TBM
	- HABITABLE ROOM WINDOW
	- SIGN STAMPED ON CONCRETE KERB
	- NON-HABITABLE ROOM WINDOW
	- PRIVATE OPEN SPACE
	- POWERLINES
	- PROPOSED FENCE
	- EXISTING FENCE
	- SEWER PIPE
	- STORM WATER PIPE
	- EASEMENT
	- SILT PIT
	- AG DRAIN
	- RETAINING WALL

TOTAL HOUSE AREA		
TOTAL HOUSE AREA	199.85	m ²
SITE AREA	425	m ²
SITE COVERAGE	46.52	%
PAVING	36.40	m ²
PERMEABLE COVERAGE	46.48	%
GARDEN COVERAGE	43.67	%



Long Island Homes Pty. Ltd.
PO BOX 6269
Point Cook, Vic 3030
p. 61 3 9369 6486 (1800 604 011)
f. 61 3 9369 0994
email: admin@longislandhomes.com.au
www.longislandhomes.com.au

© Copyright
THIS DESIGN & DRAWING SHALL REMAIN THE INTELLECTUAL PROPERTY OF LONG ISLAND HOMES PTY. LTD. AND SHALL NOT BE COPIED IN WHOLE OR PART WITHOUT WRITTEN CONSENT FROM LONG ISLAND HOMES PTY LTD.
DB NUMBER

GENERAL NOTES:
- THE CONTRACTOR IS RESPONSIBLE FOR SETTING OUT AND CHECKING ALL LEVELS AND DIMENSIONS ON SITE PRIOR TO COMMENCING ANY SITE WORKS.
- FIGURED DIMENSIONS ARE TO TAKE PREFERENCE OVER SCALE
- DIMENSIONS TO STRUCTURAL TIMBERS & FACE OF BRICKS EXCLUDING BATTENS, PLASTERBOARD ETC.
- ALL DIMENSIONS ON PLAN ARE NOMINAL & MAY VARY TO ACTUAL SIZE
- PROVIDE LOCKS TO ALL OPENABLE WINDOWS & EXTERNAL SLIDING DOORS (KEYED ALIKE).
- MAN HOLE LOCATION MAY BE CHANGED DUE TO TRUSS LAYOUT.
- WINDOW AND DOOR FRAME SIZES ARE NOMINAL AND MAY VARY WITH LONG ISLAND HOMES APPROVED SUPPLIERS.

CLIENT
I / WE.....
CONFIRM THESE DRAWINGS ACCORD WITH OUR REQUIREMENTS AND AUTHORISE THEIR USE FOR NEXT STAGE PURPOSES.
SIGNED..... DATE.....
SIGNED..... DATE.....

SHEET CONTENT:
SITE PLAN
HOUSE TYPE: SANYA 380 MIN LOT WIDTH: 12M
PROPERTY ADDRESS: 2251 SKODA CIRCUIT POINTCOOK
CLIENT: CLARE FRANSIS & CHRISTPHER KEVIN GRIFFITHS

NORTH:		FACADE:		SHEET NUMBER: 2.1	JOB NUMBER:
		SCALE: As indicated			JOB ISSUE: H
		DATE:			
REVISIONS	ISSUE	DATE	REVISION DESCRIPTION		INITIALS
	A	19.04.21	MASTER		FT
	B	29.07.21	R & C		CM
	C	04.08.21	R & C ADD AREA		CM
	D	20.09.21	COLOUR, PRE CONTRACT CLARIFICATION 06/09/21		CM
	E	27.09.21	ENERGY UPGRADES (OPT 2) & CLARIFICATION 27.09.21		CM
	F	27.09.21	WIR DOOR		CM
	G	29.09.21	ADDED ENGINEERING		CM
	H	27.10.21	CONTRACT QUOTE COMMENTS		CM

- NOTES
- ALL DIMENSIONS ON PLAN ARE NOMINAL & MAY VARY TO ACTUAL SIZES
 - CARPENTERS TO ALLOW 45MM DOOR STUD AT WALL JUNCTIONS
 - PROVIDE LOCKS TO ALL OPENABLE WINDOWS & EXTERNAL SLIDING DOORS (KEYED ALIKE)
 - MAN HOLE LOCATION MAY BE CHANGED DUE TO TRUSS LAYOUT.
 - WINDOW AND DOOR FRAME SIZES ARE NOMINAL AND MAY VARY WITH LONG ISLAND HOMES APPROVED SUPPLIERS.
 - ALL WATER CLOSETS TO HAVE REMOVABLE HINGES TO THE DOORS IF THERE IS LESS THAN 1.2m CLEARANCE BETWEEN THE CLOSET PAN & THE DOORWAY.
 - ALL DOOR HEIGHTS TO BE 2040 mm(H) INCLUDING GARAGE ACCESS DOOR UNLESS OTHERWISE NOTED.
 - ALL DOOR HEIGHTS TO BE 2040 mm(H) INCLUDING GARAGE ACCESS DOOR UNLESS OTHERWISE NOTED.
 - SHOULD EXTERNAL DOOR THRESHOLDS EXCEED 230MM AN ADDITIONAL STEP MAY BE PROVIDED ON SITE TO COMPLY WITH NCC REQUIREMENT.

- VENTING TO EXHAUST FANS & RANGEHOODS
- ALL EXHAUST FANS ARE TO BE EXTERNAL VENTED VIA ROOF OR EAVES TO THE ATMOSPHERE IN ACCORDANCE WITH THE NCC PART 3.8.7.
 - ALL ROOF COWLS ARE NOT TO BE INSTALLED TO PROMINENT STREET VIEWS

LONG ISLAND HOMES

ISLANDER

Long Island Homes Pty. Ltd.
PO BOX 6269
Point Cook, Vic 3030
p. 61 3 9369 6486 (1800 604 011)
f. 61 3 9369 0994
email: admin@longislandhomes.com.au
www.longislandhomes.com.au

© Copyright

THIS DESIGN & DRAWING SHALL REMAIN THE INTELLECTUAL PROPERTY OF LONG ISLAND HOMES PTY. LTD. AND SHALL NOT BE COPIED IN WHOLE OR PART WITHOUT WRITTEN CONSENT FROM LONG ISLAND HOMES PTY LTD.

DB NUMBER

GENERAL NOTES:

- THE CONTRACTOR IS RESPONSIBLE FOR SETTING OUT AND CHECKING ALL LEVELS AND DIMENSIONS ON SITE PRIOR TO COMMENCING ANY SITE WORKS.
- FIGURED DIMENSIONS ARE TO TAKE PREFERENCE OVER SCALE
- DIMENSIONS TO STRUCTURAL TIMBERS & FACE OF BRICKS EXCLUDING BATTENS, PLASTERBOARD ETC.
- ALL DIMENSIONS ON PLAN ARE NOMINAL & MAY VARY TO ACTUAL SIZE
- PROVIDE LOCKS TO ALL OPENABLE WINDOWS & EXTERNAL SLIDING DOORS (KEYED ALIKE).
- MAN HOLE LOCATION MAY BE CHANGED DUE TO TRUSS LAYOUT.
- WINDOW AND DOOR FRAME SIZES ARE NOMINAL AND MAY VARY WITH LONG ISLAND HOMES APPROVED SUPPLIERS.

CLIENT

I / WE.....

CONFIRM THESE DRAWINGS ACCORD WITH OUR REQUIREMENTS AND AUTHORISE THEIR USE FOR NEXT STAGE PURPOSES.

SIGNED..... DATE.....

SIGNED..... DATE.....

SHEET CONTENT:

PLAN - GROUND FLOOR

HOUSE TYPE: SANYA 380

MIN LOT WIDTH: 12M

PROPERTY ADDRESS: 2251 SKODA CIRCUIT POINTCOOK

CLIENT: CLARE FRANSIS & CHRISTPHER KEVIN GRIFFITHS

NORTH:

REVISIONS

ISSUE	DATE	REVISION DESCRIPTION	INITIALS
A	19.04.21	MASTER	FT
B	29.07.21	R & C	CM
C	04.08.21	R & C ADD AREA	CM
D	20.09.21	COLOUR, PRE CONTRACT CLARIFICATION 06/09/21	CM
E	27.09.21	ENERGY UPGRADES (OPT 2) & CLARIFICATION 27.09.21	CM
F	27.09.21	WIR DOOR	CM
G	29.09.21	ADDED ENGINEERING	CM
H	27.10.21	CONTRACT QUOTE COMMENTS	CM

SANYA 380- AREAS			
NAME	AREA (sqm)	SQR	
PORCH	12.03 m²	1.30	
GROUND FLOOR	143.02 m²	15.40	
GARAGE	36.34 m²	3.91	
FIRST FLOOR	136.38 m²	14.68	
BALCONY	9.38 m²	1.01	
Total	337.15 m²	36.29	

SHEET NUMBER: 3.1		JOB NUMBER: H	
JOB ISSUE: H			

PLAN - GROUND FLOOR

SCALE 1 : 100

LEGEND

- GAS METER
- METER BOX
- HOT WATER SYSTEM
- CAPPED HOT WATER
- CAPPED COLD WATER
- CAPPED SEWER

SITE SPECIFIC NOTES

- PROVIDE 67 x 12mm PENCIL ROUND ARCHITRAVES AND SKIRTING BOARD TO WET AREAS
- PROVIDE 75mm SCOTIA COVE CORNICE.
- PROVIDE CAPPED COLD WATER POINT TO FRIDGE SPACE.
- PROVIDE 2NO. FLY DOORS TO LIVING STACKER DOOR AND 1NO. FLY DOOR TO MEALS SLIDING DOOR
- PROVIDE FLYSCREENS TO ALL OPENABLE WINDOWS
- PROVIDE CAPPED SEWER POINT, CAPPED COLD WATER POINT AND CAPPED HOT WATER POINT TO CASUAL LIVING.
- PROVIDE 2NO. PRIVACY LOCKS TO PDR AND BED 1 HINGED DOORS.

27/10/2021 8:44:50 AM J:\LONG ISLAND JOBS\2251 Skoda Circuit, Point Cook\DRAWING\2251SKO_REV.H.rvt

- 
- LONG
ISLAND
HOMES
- ISLANDER**

© Copyright
THIS DESIGN & DRAWING SHALL REMAIN THE INTELLECTUAL PROPERTY OF
LONG ISLAND HOMES PTY. LTD. AND SHALL NOT BE COPIED IN WHOLE OR
PART WITHOUT WRITTEN CONSENT FROM LONG ISLAND HOMES PTY LTD.
DB NUMBER


CLIENT

SIGNED..... DATE.....

CLIENT: CLARE FRANSIS & CHRISTPHER KEVIN GRIFFITHS

	ISSUE	DATE	REVISION DESCRIPTION	INITIALS
REVISIONS	A	19.04.21	MASTER	FT
	B	29.07.21	R & C	CM
	C	04.08.21	R & C ADD AREA	CM
	D	20.09.21	COLOUR, PRE CONTRACT CLARIFICATION 06/09/21	CM
	E	27.09.21	ENERGY UPGRADES (OPT 2) & CLARIFICATION 27.09.21	CM
	F	27.09.21	WIR DOOR	CM
	G	29.09.21	ADDED ENGINEERING	CM
	H	27.10.21	CONTRACT QUOTE COMMENTS	CM

SCALE 1 : 100

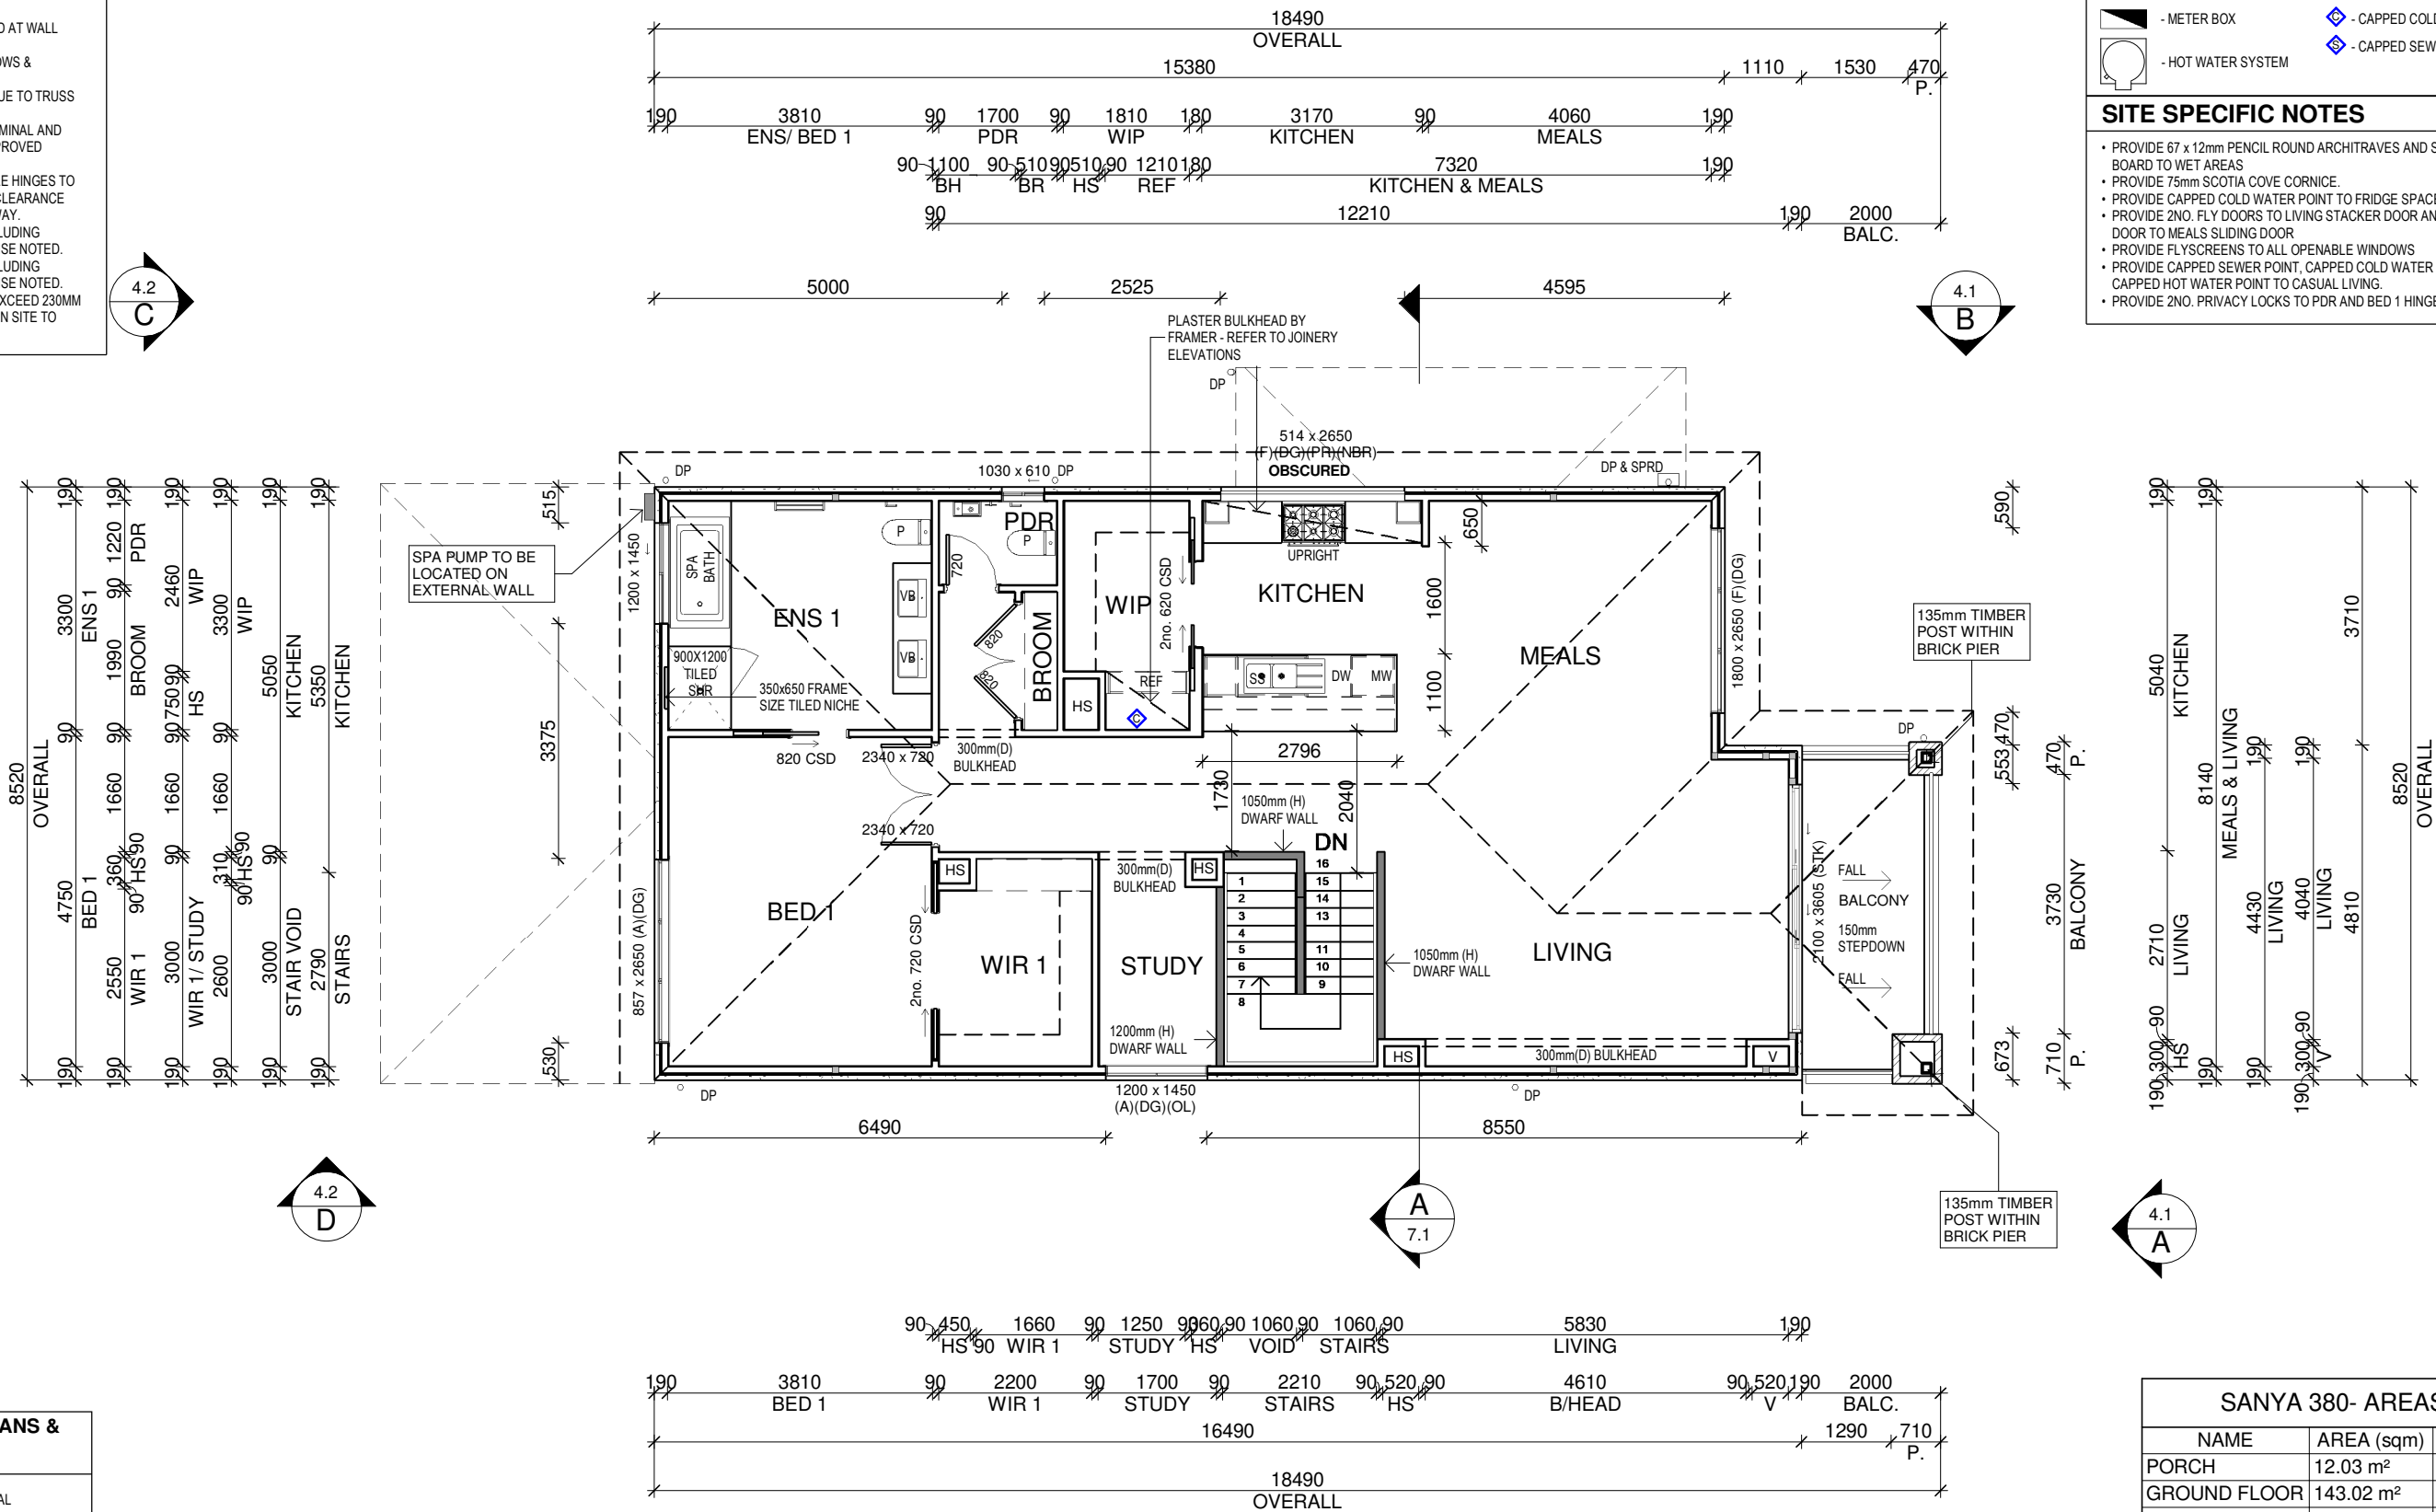

SANYA 380- AREAS		
NAME	AREA (sqm)	SQR
PORCH	12.03 m²	1.30
GROUND FLOOR	143.02 m²	15.40
GARAGE	36.34 m²	3.91
FIRST FLOOR	136.38 m²	14.68
BALCONY	9.38 m²	1.01
Total	337.15 m²	36.29

BRICKY'S NOTES:

- ARTICULATION JOINTS TO ALL INTERNAL CORNERS.
- PERPS AND BEDS TO BE INSTALLED STRICTLY TO AS3700.
- USE INFILLS BESIDE WINDOWS AND DOORS IF NECESSARY.
- CUT BRICKS IF NECESSARY.
- DO NOT UNDER ANY CIRCUMSTANCE COMPROMISE PERPS AND BEDS.
- LIFT WINDOWS TIGHT UNDER SIDE OF LINTEL BEFORE LAYING BRICK SILLS.
- ALL FIRST FLOOR BEDROOM WINDOWS WITH OPENING HEIGHT LESS THAN 1700mm TO BE RESTRICTED TO 125mm OPENING
- LOW EMISSION PAINTS & SEALANTS WILL BE USE FOR INTERNAL AND EXTERNAL PAINTED SURFACES.
- PROVIDE WEEP HOLES AT 1200mm SPACING AROUND BRICK WALLS AND ABOVE OPENING GREATER THAN 1m.

NOTE: BACK FILL

- SITE TO BE BACK FILLED TO REBATE HEIGHT & FALL AWAY FROM DWELLING.

OBSCURE GLAZING

DENOTES CATHEDRAL GLAZING

DENOTES OBSCURED GLASS

ELEVATION A
SCALE 1 : 100




VENTING TO EXHAUST FANS & RANGEHOODS

- ALL EXHAUST FANS ARE TO BE EXTERNAL VENTED VIA ROOF OR EAVES TO THE ATMOSPHERE IN ACCORDANCE WITH THE NCC PART 3.8.7.
- ALL ROOF COWLS ARE NOT TO BE INSTALLED TO PROMINENT STREET VIEWS

NOTE: COROSION PROTECTION

PROVIDE CORROSION PROTECTION TO EXPOSED STEELWORK OF DOUBLE STOREY DWELLING WITH TILED ROOF, REQUIRED DUE TO PROXIMITY OF DWELLING TO THE OCEAN. PROVIDE CORROSION PROTECTION TO EXPOSED METAL ROOF.

ELEVATION B
SCALE 1 : 100

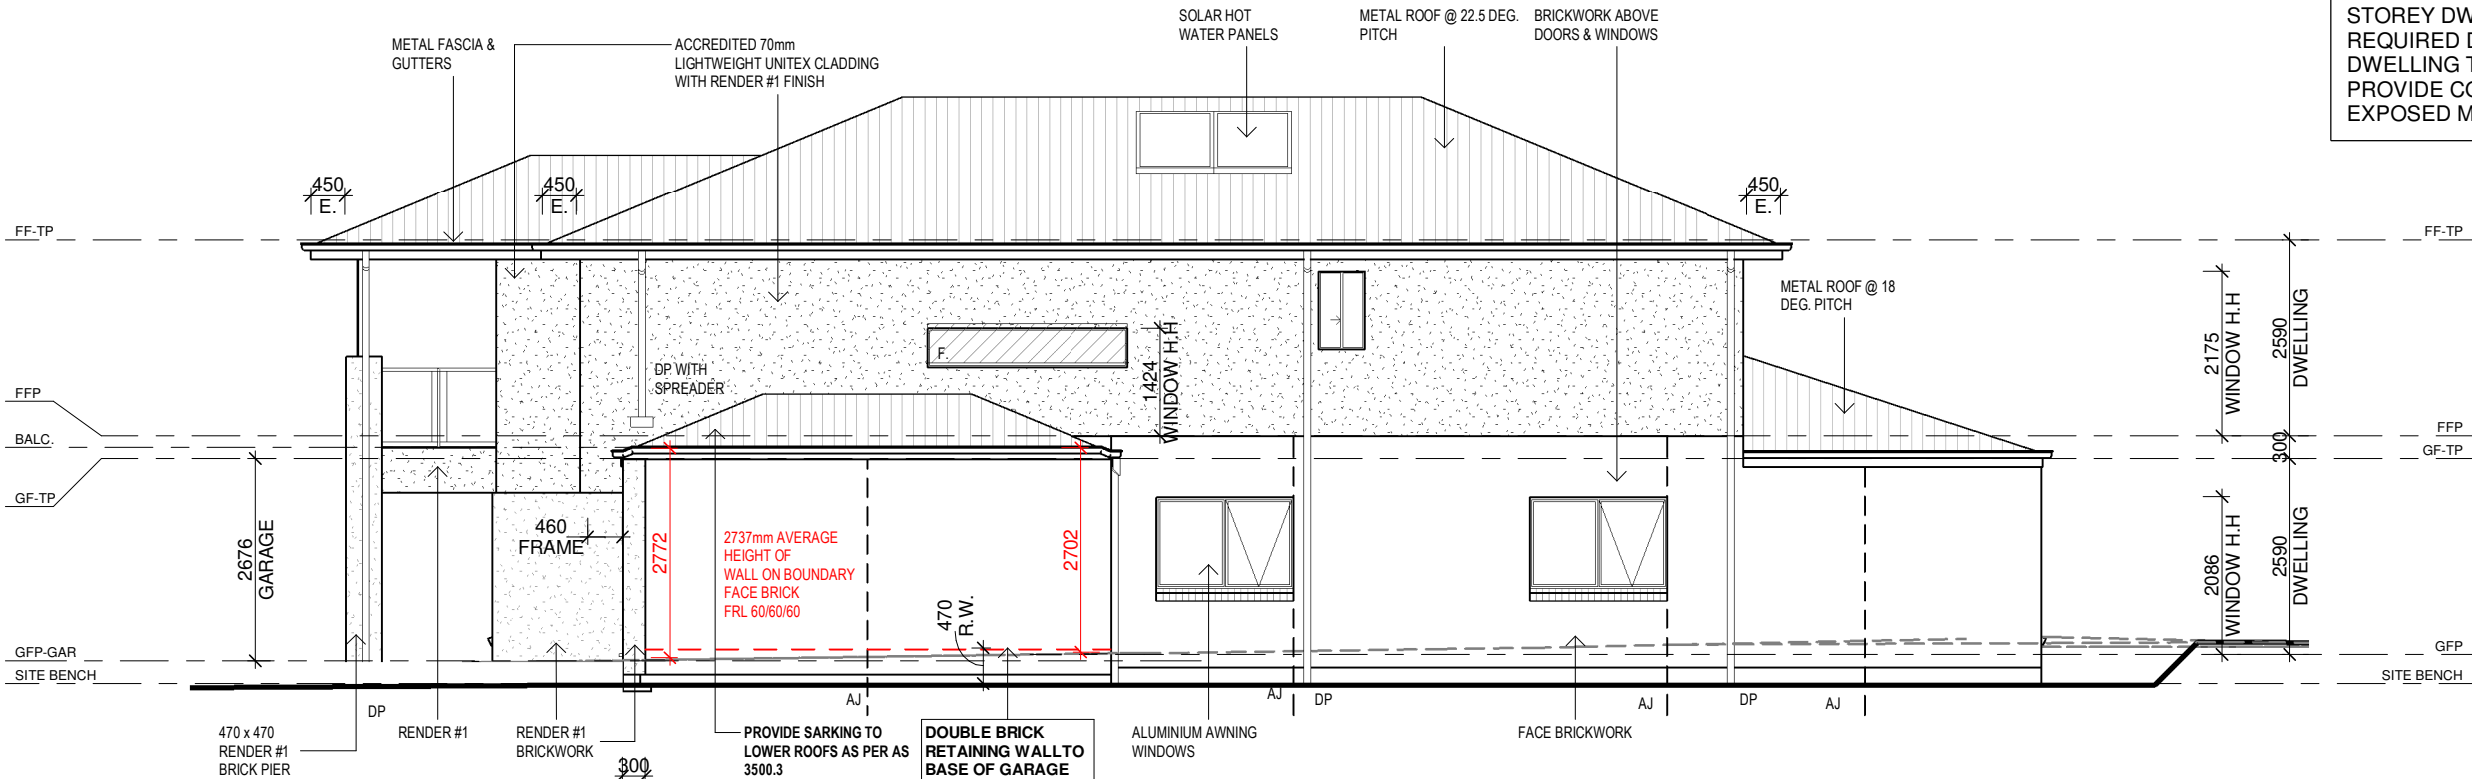

27/10/2021 8:44:52 AM J:\LONG ISLAND JOBS\2251 Skoda Circuit, Point Cook\DRAWING\2251SKO_REV H.rvt



ISLANDER

Long Island Homes Pty. Ltd.
PO BOX 6269
Point Cook, Vic 3030
p. 61 3 9369 6486 (1800 604 011)
f. 61 3 9369 0994
email: admin@longislandhomes.com.au
www.longislandhomes.com.au

© Copyright

THIS DESIGN & DRAWING SHALL REMAIN THE INTELLECTUAL PROPERTY OF LONG ISLAND HOMES PTY. LTD. AND SHALL NOT BE COPIED IN WHOLE OR PART WITHOUT WRITTEN CONSENT FROM LONG ISLAND HOMES PTY LTD.

DB NUMBER

GENERAL NOTES:

- THE CONTRACTOR IS RESPONSIBLE FOR SETTING OUT AND CHECKING ALL LEVELS AND DIMENSIONS ON SITE PRIOR TO COMMENCING ANY SITE WORKS.
- FIGURED DIMENSIONS ARE TO TAKE PREFERENCE OVER SCALE
- DIMENSIONS TO STRUCTURAL TIMBERS & FACE OF BRICKS EXCLUDING BATTENS, PLASTERBOARD ETC.
- ALL DIMENSIONS ON PLAN ARE NOMINAL & MAY VARY TO ACTUAL SIZE
- PROVIDE LOCKS TO ALL OPENABLE WINDOWS & EXTERNAL SLIDING DOORS (KEYED ALIKE).
- MAN HOLE LOCATION MAY BE CHANGED DUE TO TRUSS LAYOUT.
- WINDOW AND DOOR FRAME SIZES ARE NOMINAL AND MAY VARY WITH LONG ISLAND HOMES APPROVED SUPPLIERS.

CLIENT

I / WE.....

CONFIRM THESE DRAWINGS ACCORD WITH OUR REQUIREMENTS AND AUTHORISE THEIR USE FOR NEXT STAGE PURPOSES.

SIGNED..... DATE.....

SIGNED..... DATE.....

SHEET CONTENT:

ELEVATIONS A & B

HOUSE TYPE:
SANYA 380

MIN LOT WIDTH:
12M

PROPERTY ADDRESS:
2251 SKODA CIRCUIT
POINTCOOK

CLIENT:
CLARE FRANSIS & CHRISTPHER
KEVIN GRIFFITHS

NORTH:

FACADE:

SCALE: As indicated

DATE:

SHEET NUMBER:

4.1

JOB NUMBER:

JOB ISSUE:

H

ISSUE	DATE	REVISION DESCRIPTION	INITIALS
A	19.04.21	MASTER	FT
B	29.07.21	R & C	CM
C	04.08.21	R & C ADD AREA	CM
D	20.09.21	COLOUR, PRE CONTRACT CLARIFICATION 06/09/21	CM
E	27.09.21	ENERGY UPGRADES (OPT 2) & CLARIFICATION 27.09.21	CM
F	27.09.21	WIR DOOR	CM
G	29.09.21	ADDED ENGINEERING	CM
H	27.10.21	CONTRACT QUOTE COMMENTS	CM

- ARTICULATION JOINTS TO ALL INTERNAL CORNERS.
- PERPS AND BEDS TO BE INSTALLED STRICTLY TO AS3700.
- USE INFILLS BESIDE WINDOWS AND DOORS IF NECESSARY.
- CUT BRICKS IF NECESSARY.
- DO NOT UNDER ANY CIRCUMSTANCE COMPROMISE PERPS AND BEDS.
- LIFT WINDOWS TIGHT UNDER SIDE OF LINTEL BEFORE LAYING BRICK SILLS.
- ALL FIRST FLOOR BEDROOM WINDOWS WITH OPENING HEIGHT LESS THAN 1700mm TO BE RESTRICTED TO 125mm OPENING
- LOW EMISSION PAINTS & SEALANTS WILL BE USE FOR INTERNAL AND EXTERNAL PAINTED SURFACES.
- PROVIDE WEEP HOLES AT 1200mm SPACING AROUND BRICK WALLS AND ABOVE OPENING GREATER THAN 1m.

- SITE TO BE BACK FILLED TO REBATE HEIGHT & FALL AWAY FROM DWELLING.

 DENOTES CATHEDRAL GLAZING

 DENOTES OBSCURED GLASS



- ALL EXHAUST FANS ARE TO BE EXTERNAL VENTED VIA ROOF OR EAVES TO THE ATMOSPHERE IN ACCORDANCE WITH THE NCC PART 3.8.7.
- ALL ROOF COWLS ARE NOT TO BE INSTALLED TO PROMINENT STREET VIEWS

ELEVATION D

SCALE 1 : 100



© Copyright
THIS DESIGN & DRAWING SHALL REMAIN THE INTELLECTUAL PROPERTY OF
LONG ISLAND HOMES PTY. LTD. AND SHALL NOT BE COPIED IN WHOLE OR
PART WITHOUT WRITTEN CONSENT FROM LONG ISLAND HOMES PTY LTD.
DB NUMBER

THE CONTRACTOR IS RESPONSIBLE FOR SETTING OUT AND CHECKING ALL LEVELS AND DIMENSIONS ON SITE PRIOR TO COMMENCING ANY SITE WORKS.

FIGURED DIMENSIONS ARE TO TAKE PREFERENCE OVER SCALE

DIMENSIONS TO STRUCTURAL TIMBERS & FACE OF BRICKS EXCLUDING BATTENS, PLASTERBOARD ETC.

ALL DIMENSIONS ON PLAN ARE NOMINAL & MAY VARY TO ACTUAL SIZE

PROVIDE LOCKS TO ALL OPENABLE WINDOWS & EXTERNAL SLIDING DOORS (KEYED ALIKE).

MAN HOLE LOCATION MAY BE CHANGED DUE TO TRUSS LAYOUT.

WINDOW AND DOOR FRAME SIZES ARE NOMINAL AND MAY VARY WITH LONG ISLAND HOMES APPROVED SUPPLIERS.

CONFIRM THESE DRAWINGS ACCORD WITH OUR
REQUIREMENTS AND AUTHORISE THEIR USE FOR
NEXT STAGE PURPOSES.

SIGNED..... DATE.....

SIGNED..... DATE.....

CLIENT: CLARE FRANSIS & CHRISTPHER KEVIN GRIFFITHS

REVISIONS	ISSUE	DATE	REVISION DESCRIPTION	INITIALS
	A	19.04.21	MASTER	FT
	B	29.07.21	R & C	CM
	C	04.08.21	R & C ADD AREA	CM
	D	20.09.21	COLOUR, PRE CONTRACT CLARIFICATION 06/09/21	CM
	E	27.09.21	ENERGY UPGRADES (OPT 2) & CLARIFICATION 27.09.21	CM
	F	27.09.21	WIR DOOR	CM
	G	29.09.21	ADDED ENGINEERING	CM
	H	27.10.21	CONTRACT QUOTE COMMENTS	CM

WATTAGE CALCULATIONS			
NCC PART 3.12.5.5 ARTIFICIAL LIGHTING LAMPPOWER DENSITY SHALL NOT EXCEED: • 5W/sq.m FOR CLASS 1 BUILDING • 4W/sq.m FOR VERANDAH, ALFRESCO, PORCH OR BALCONY • 3W/sq.m FOR CLASS 10a BUILDING PERIMETER LIGHTING TO BE CONTROLLED BY A SENSOR OR HAVE A MAXIMUM OF 40 LUMENS PER WATT. • SMOKE DETECTORS TO BE INTERCONNECTED AS PER NCC 2015.			
AREA SPECIFIED	TOTAL AREA	ALLOWABLE WATTAGE	TOTAL WATTAGE
RESIDENCE 5W/sq.m:	279.26 m2	MAX. 1396.30 WATTS	1588.28 W
PORCH & BALCONY 4W/sq.m:	20.74 m2	MAX. 82.96 WATTS	
GARAGE 3W/sq.m:	36.34 m2	MAX. 109.02 WATTS	

ELECTRICAL PACK

- 30 x LED DOWNLIGHTS
- 10 x ADDITIONAL DOUBLE POWER POINTS
- 2 x WALL MOUNTED COACH LIGHTS
- 2 x SENSORS
- 1 x DIMMER TO RUMPUS

ELECTRICAL NOTES

- PROVIDE ENERGY SAVING LIGHT BULBS TO BATTEN LIGHTING THROUGHOUT.
- PROVIDE WHITE COVER PLATES TO SWITCHES.
- PROVIDE LINKED SMOKE DETECTORS, HARDWIRED WITH BATTERY BACKUP.
- PROVIDE CAPPED COLD WATER POINT TO FRIDGE SPACE.
- PROVIDE CAPPED SEWER POINT, CAPPED COLD WATER POINT AND CAPPED HOT WATER POINT TO CASUAL LIVING.

FIBRE OPTIC: NBN BASIC PACK

PROVIDE FIBRE OPTIC IN ACCORDANCE WITH ESTATE REQUIREMENTS. THIS INVOLVES DISTRIBUTION OF DATA, PHONE & TV FROM ONE CENTRE LOCATION.

- 1 X DATA
- 1 X PHONE
- 4 X TELEVISION


NOTE:
- NO PAY TV IN NBN OPTIC NETWORK SERVICE
- CONDUIT AND DRAW WIRE FROM TELECOMMUNICATIONS SUPPLY PIT TO THE TERMINATION POINT.
- IT IS THE OWNER'S RESPONSIBILITY TO ARRANGE CONNECTION OF THE FOLLOWING SERVICES WITH THE APPROPRIATE PROVIDERS AFTER HANDOVER.
- EXCLUDES TV ANTENNA.

HEATING & COOLING

- PROVIDE GAS DUCTED HEATING.
- PROVIDE BRAEMAR EVAPORATIVE COOLING TO 5 OUTLETS. INCLUDES SEPARATE MAGI-Q-TOUCH CONTROLLER.

ELECTRICAL ITEMS

ITEM	TOTAL
DGPO	28
DGPO - EXTERNAL	3
DUCT - COOLING	5
DUCT - HEATING	11
EXHAUSTING FAN	2
FLOOD LIGHT - SINGLE	3
LIGHT - BATTEN	16
LIGHT - EXTERNAL WALL BATTEN	2
LIGHT - LED	42
POINT - DATA	1
POINT - PHONE	1
POINT - TV	4
SGPO	5
SMOKE DETECTOR	4

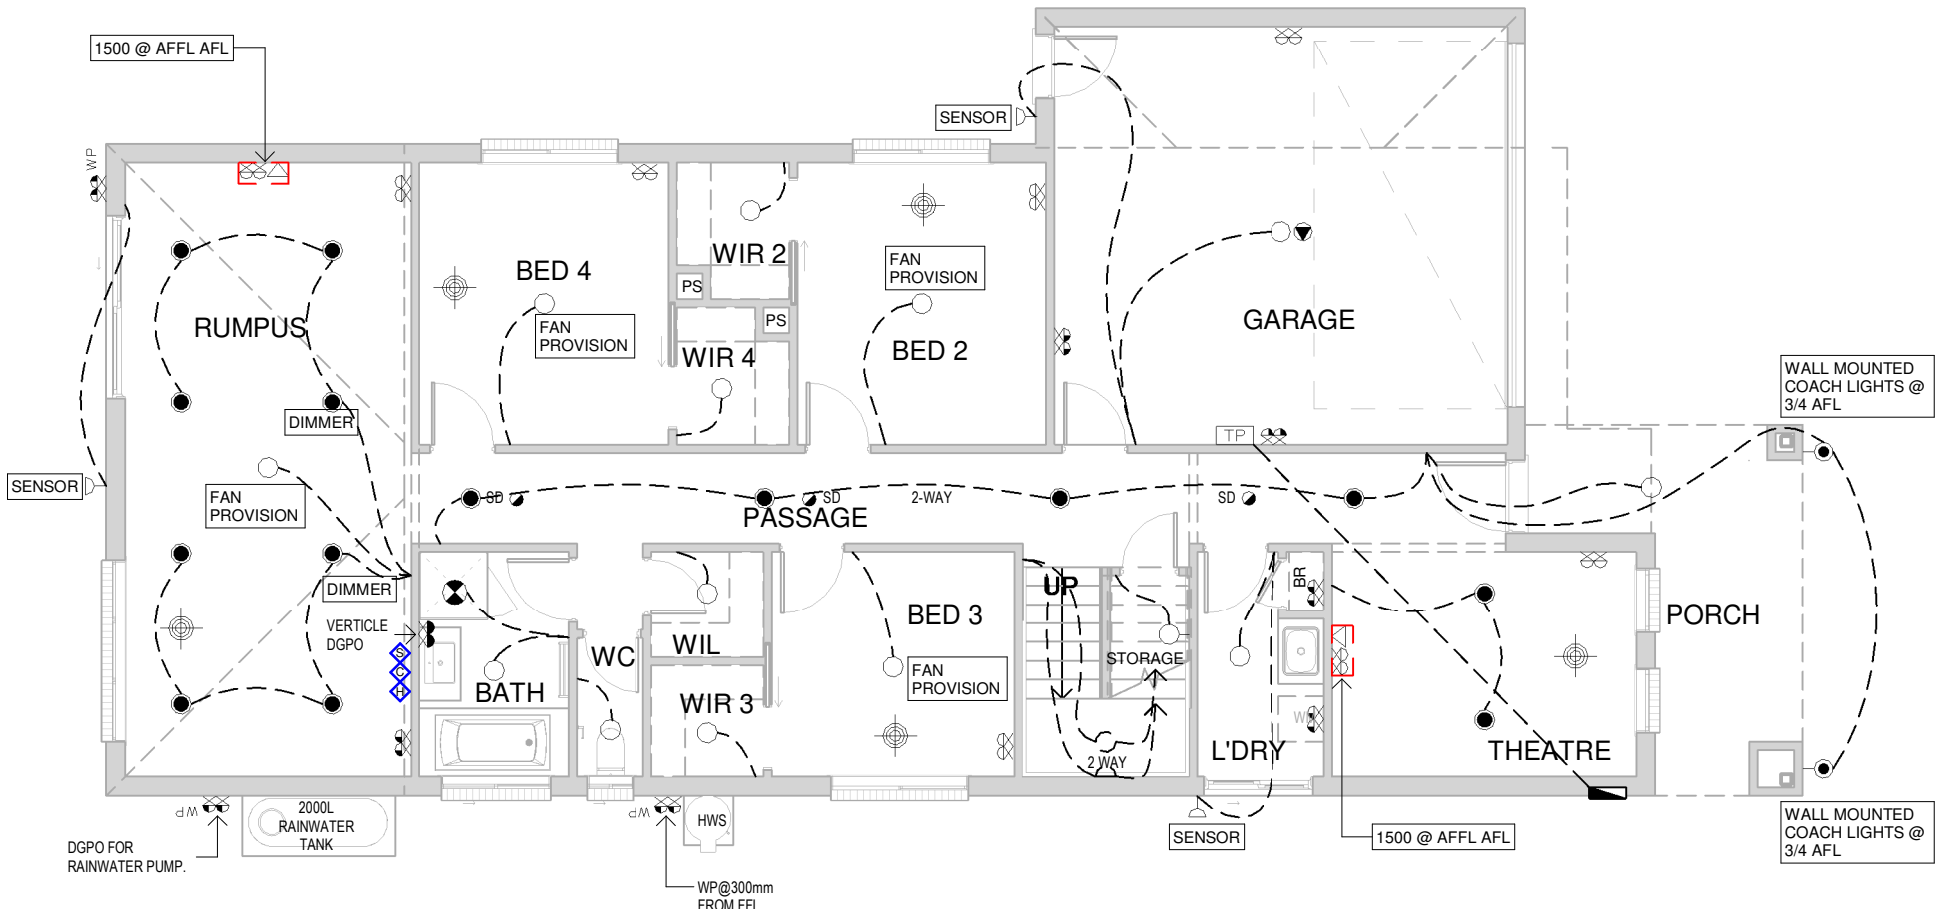

VENTING TO EXHAUST FANS & RANGEHOODS

- ALL EXHAUST FANS ARE TO BE EXTERNAL VENTED VIA ROOF OR EAVES TO THE ATMOSPHERE IN ACCORDANCE WITH THE NCC PART 3.8.7.
- ALL ROOF COWLS ARE NOT TO BE INSTALLED TO PROMINENT STREET VIEWS

ELECTRICAL LEGEND

ALL ELECTRICAL LOCATIONS ARE INDICATIVE ONLY

	STANDARD BATTEN
	LED DOWNLIGHT (AS SELECTED)
	POWERSAVER 133 DOWNLIGHT (AS SELECTED)
	EXTERNAL LIGHT POINT
	FLOOD LIGHT - SINGLE
	FLOOD LIGHT - DOUBLE
	WALL LIGHT BATTEN HOLDER - INTERNAL
	WALL LIGHT BATTEN HOLDER - EXTERNAL
	600 FLUORO - SINGLE
	1200 FLUORO - SINGLE
	CEILING FAN
	CEILING FAN WITH LIGHT
	CEILING EXHAUST FAN
	SINGLE GPO - 300mm
	SINGLE GPO - 1100mm
	SINGLE GPO - 1350mm
	SINGLE GPO - EXTERNAL WEATHERPROOF
	DOUBLE GPO - EXTERNAL WEATHERPROOF
	SINGLE GPO - FOR M/WAVE @ 750mm(H)
	SINGLE GPO - DISHWASHER @ 750mm(H)
	DOUBLE GPO - 300mm
	DOUBLE GPO - 1100mm
	DOUBLE GPO - 1350mm
	TELEVISION POINT
	PAY TV POINT
	SMOKE DETECTOR
	GAS METER
	OYSTER LIGHT
	METER BOX
	EVAPORATIVE COOLING UNIT - INDICATIVE LOCATION
	CEILING HEATING DUCT (APPROX. LOCATION)
	THERMOSTAT
	EVAPORATIVE COOLING DUCT
	RETURN AIR
	HEATING UNIT WITH LIGHT & GPO IN CEILING
	POWER POINT FOR GARAGE REMOTE PANEL DOOR - LOCATE ON CEILING 3300mm FROM DOOR OPENING LINTEL & 200mm OFF DOOR CENTRE.
	20 AMP ISOLATION SWITCH HARD WIRED ON A SEPARATE CIRCUIT FOR AIR-CON. @ 500mm HIGH.
	JUNCTION BOX
	ALARM UNIT (SENSOR & KEYPAD AS PER MANUFACTURERS' SPECIFICATIONS)
	SINGLE GPO - FOR SECURITY SYS.
	HEATER/FAN UNIT - 2 GLOBE
	HEATER/FAN UNIT - 4 GLOBE
	DATA POINT
	HUB POINT
	TERMINATION POINT
	TELEPHONE POINT
	DOOR BELL
	ALARM KEYPAD
	ALARM MONITOR
	ALARM SENSORS (INDICATIVE ONLY)
	GARDEN TAP
	VACUUM DUCT
	VACUUM MOTOR

ELECTRICAL - GROUND FLOOR
SCALE 1 : 100



ISLANDER

Long Island Homes Pty. Ltd.
PO BOX 6269
Point Cook, Vic 3030
p. 61 3 9369 6486 (1800 604 011)
f. 61 3 9369 0994
email: admin@longislandhomes.com.au
www.longislandhomes.com.au

© Copyright
THIS DESIGN & DRAWING SHALL REMAIN THE INTELLECTUAL PROPERTY OF LONG ISLAND HOMES PTY. LTD. AND SHALL NOT BE COPIED IN WHOLE OR PART WITHOUT WRITTEN CONSENT FROM LONG ISLAND HOMES PTY LTD.
DB NUMBER

GENERAL NOTES:

- THE CONTRACTOR IS RESPONSIBLE FOR SETTING OUT AND CHECKING ALL LEVELS AND DIMENSIONS ON SITE PRIOR TO COMMENCING ANY SITE WORKS.
- FIGURED DIMENSIONS ARE TO TAKE PREFERENCE OVER SCALE
- DIMENSIONS TO STRUCTURAL TIMBERS & FACE OF BRICKS EXCLUDING BATTENS, PLASTERBOARD ETC.
- ALL DIMENSIONS ON PLAN ARE NOMINAL & MAY VARY TO ACTUAL SIZE
- PROVIDE LOCKS TO ALL OPENABLE WINDOWS & EXTERNAL SLIDING DOORS (KEYED ALIKE).
- MAN HOLE LOCATION MAY BE CHANGED DUE TO TRUSS LAYOUT.
- WINDOW AND DOOR FRAME SIZES ARE NOMINAL AND MAY VARY WITH LONG ISLAND HOMES APPROVED SUPPLIERS.

CLIENT

I / WE.....

CONFIRM THESE DRAWINGS ACCORD WITH OUR REQUIREMENTS AND AUTHORISE THEIR USE FOR NEXT STAGE PURPOSES.

SIGNED..... DATE.....

SIGNED..... DATE.....

SHEET CONTENT:

ELECTRICAL - GROUND FLOOR

HOUSE TYPE: SANYA 380
MIN LOT WIDTH: 12M

PROPERTY ADDRESS:
2251 SKODA CIRCUIT
POINTCOOK

CLIENT:
CLARE FRANSIS & CHRISTPHER
KEVIN GRIFFITHS

NORTH:

FACADE:

SCALE: As indicated

DATE:

SHEET NUMBER:

5.1

JOB NUMBER:

H

REVISIONS

ISSUE	DATE	REVISION DESCRIPTION	INITIALS
A	19.04.21	MASTER	FT
B	29.07.21	R & C	CM
C	04.08.21	R & C ADD AREA	CM
D	20.09.21	COLOUR, PRE CONTRACT CLARIFICATION 06/09/21	CM
E	27.09.21	ENERGY UPGRADES (OPT 2) & CLARIFICATION 27.09.21	CM
F	27.09.21	WIR DOOR	CM
G	29.09.21	ADDED ENGINEERING	CM
H	27.10.21	CONTRACT QUOTE COMMENTS	CM


27/10/2021 8:44:55 AM J:\LONG ISLAND JOBS\2251 Skoda Circuit, Point Cook\DRAWING\2251SKO_REV H.rvt

FLOOR COVERINGS

-  DENOTES CARPET
-  DENOTES TILES
-  DENOTES NATURAL CONCRETE
-  DENOTES LAMINATE FLOORING
-  DENOTES EXPOSED AGGREGATE
-  DENOTES COLOURED CONCRETE
-  DENOTES STAINED KDHW

NOTES:

- IF FLOOR COVERINGS ARE SUPPLIED BY LONG ISLAND HOMES, THE PATTERNED HATCH SHOWN ON DRAWINGS DOES NOT INDICATE LAYOUT OR DIRECTION OF FINISH.

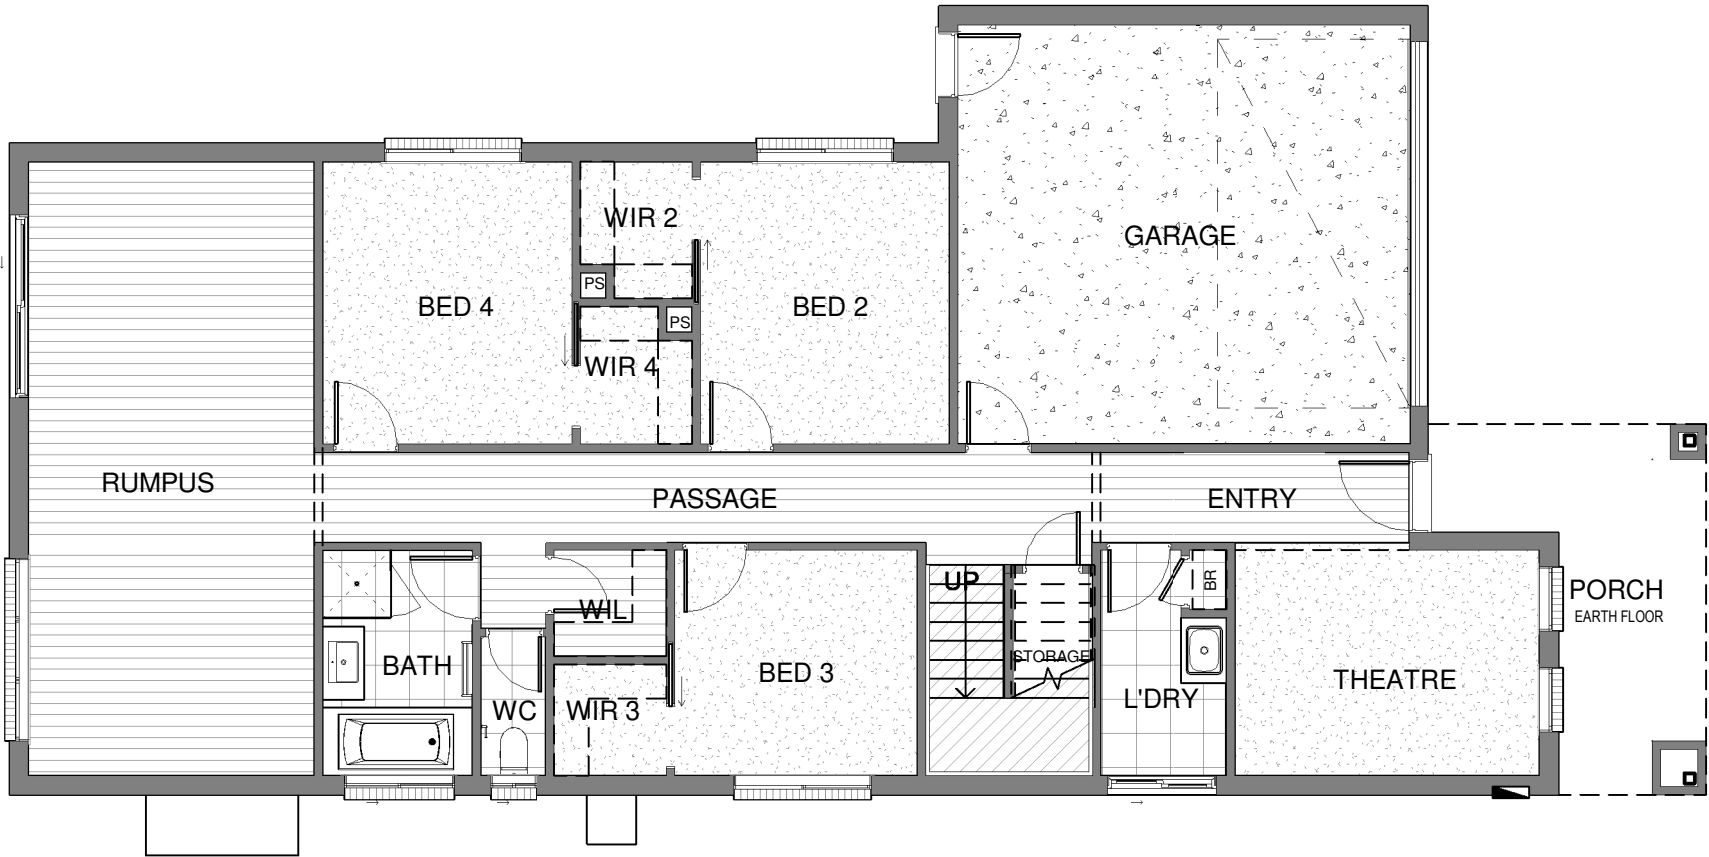

FLOORING - GROUND FLOOR
SCALE 1 : 100



Long Island Homes Pty. Ltd.
PO BOX 6269
Point Cook, Vic 3030
p. 61 3 9369 6486 (1800 604 011)
f. 61 3 9369 0994
email: admin@longislandhomes.com.au
www.longislandhomes.com.au

© Copyright
THIS DESIGN & DRAWING SHALL REMAIN THE INTELLECTUAL PROPERTY OF
LONG ISLAND HOMES PTY. LTD. AND SHALL NOT BE COPIED IN WHOLE OR
PART WITHOUT WRITTEN CONSENT FROM LONG ISLAND HOMES PTY LTD.
DB NUMBER

GENERAL NOTES:

- THE CONTRACTOR IS RESPONSIBLE FOR SETTING OUT AND CHECKING ALL LEVELS AND DIMENSIONS ON SITE PRIOR TO COMMENCING ANY SITE WORKS.
- FIGURED DIMENSIONS ARE TO TAKE PREFERENCE OVER SCALE
- DIMENSIONS TO STRUCTURAL TIMBERS & FACE OF BRICKS EXCLUDING BATTENS, PLASTERBOARD ETC.
- ALL DIMENSIONS ON PLAN ARE NOMINAL & MAY VARY TO ACTUAL SIZE
- PROVIDE LOCKS TO ALL OPENABLE WINDOWS & EXTERNAL SLIDING DOORS (KEYED ALIKE).
- MAN HOLE LOCATION MAY BE CHANGED DUE TO TRUSS LAYOUT.
- WINDOW AND DOOR FRAME SIZES ARE NOMINAL AND MAY VARY WITH LONG ISLAND HOMES APPROVED SUPPLIERS.

CLIENT

I / WE.....

CONFIRM THESE DRAWINGS ACCORD WITH OUR REQUIREMENTS AND AUTHORISE THEIR USE FOR NEXT STAGE PURPOSES.

SIGNED..... DATE.....

SIGNED..... DATE.....

SHEET CONTENT:

FLOORING - GROUND FLOOR

HOUSE TYPE: SANYA 380

MIN LOT WIDTH: 12M

PROPERTY ADDRESS: 2251 SKODA CIRCUIT POINTCOOK

CLIENT: CLARE FRANSIS & CHRISTPHER KEVIN GRIFFITHS

NORTH:

FACADE:

SCALE: 1 : 100

DATE:

SHEET NUMBER: 6.1

JOB NUMBER:

JOB ISSUE: H

REVISIONS


ISSUE	DATE	REVISION DESCRIPTION	INITIALS
A	19.04.21	MASTER	FT
B	29.07.21	R & C	CM
C	04.08.21	R & C ADD AREA	CM
D	20.09.21	COLOUR, PRE CONTRACT CLARIFICATION 06/09/21	CM
E	27.09.21	ENERGY UPGRADES (OPT 2) & CLARIFICATION 27.09.21	CM
F	27.09.21	WIR DOOR	CM
G	29.09.21	ADDED ENGINEERING	CM
H	27.10.21	CONTRACT QUOTE COMMENTS	CM

FLOOR COVERINGS

-  DENOTES CARPET
-  DENOTES TILES
-  DENOTES NATURAL CONCRETE
-  DENOTES LAMINATE FLOORING
-  DENOTES EXPOSED AGGREGATE
-  DENOTES COLOURED CONCRETE
-  DENOTES STAINED KDHW

NOTES:

- IF FLOOR COVERINGS ARE SUPPLIED BY LONG ISLAND HOMES, THE PATTERNED HATCH SHOWN ON DRAWINGS DOES NOT INDICATE LAYOUT OR DIRECTION OF FINISH.

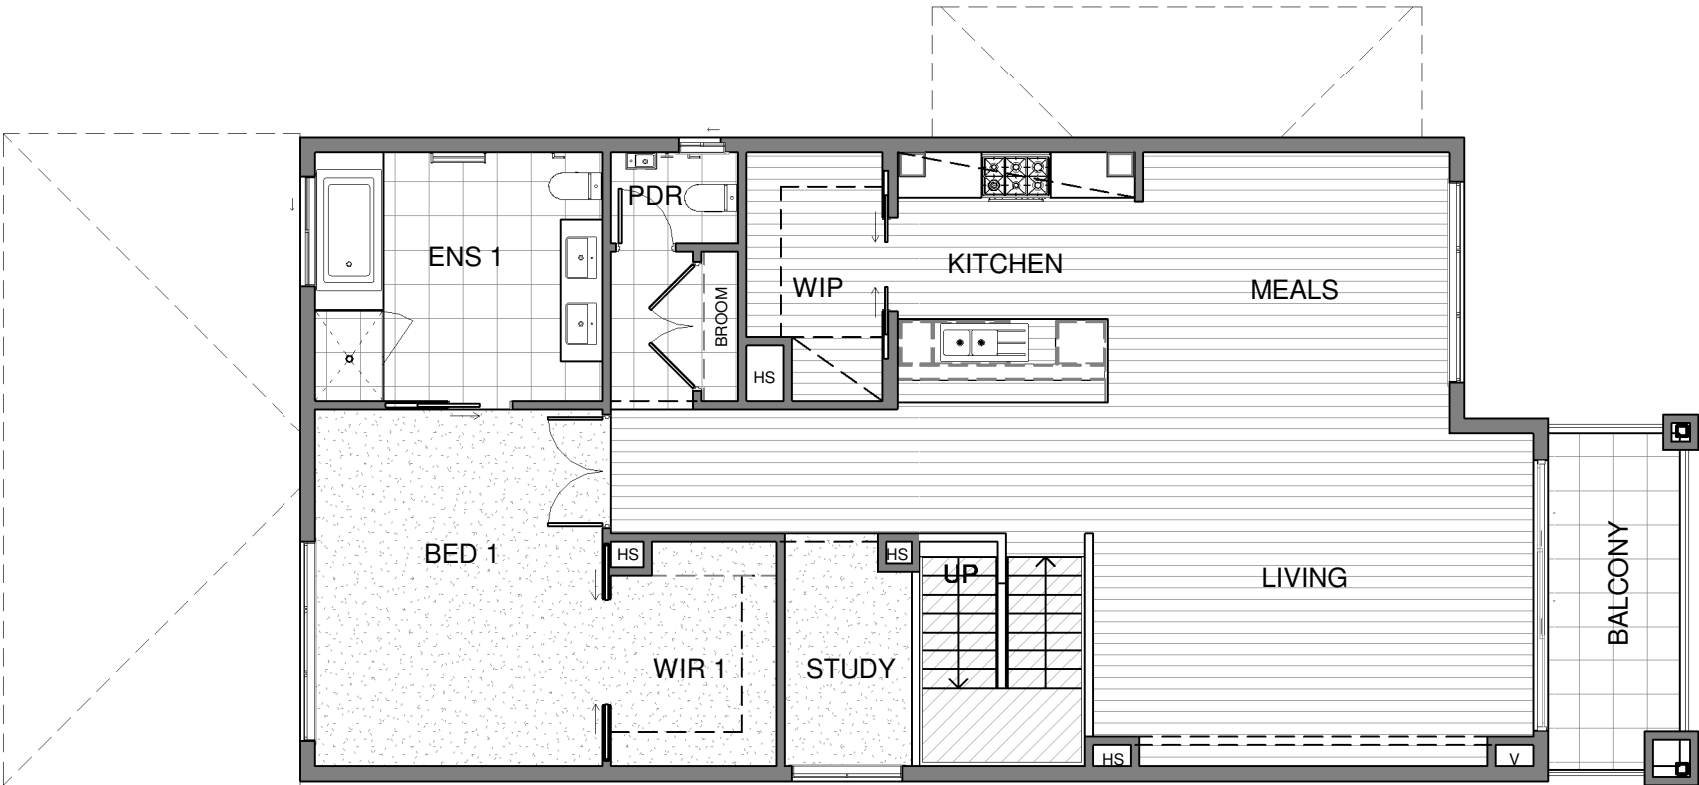

FLOORING - FIRST FLOOR

SCALE 1 : 100



ISLANDER

Long Island Homes Pty. Ltd.
PO BOX 6269
Point Cook, Vic 3030
p. 61 3 9369 6486 (1800 604 011)
f. 61 3 9369 0994
email: admin@longislandhomes.com.au
www.longislandhomes.com.au

© Copyright
THIS DESIGN & DRAWING SHALL REMAIN THE INTELLECTUAL PROPERTY OF
LONG ISLAND HOMES PTY. LTD. AND SHALL NOT BE COPIED IN WHOLE OR
PART WITHOUT WRITTEN CONSENT FROM LONG ISLAND HOMES PTY LTD.
DB NUMBER

GENERAL NOTES:

- THE CONTRACTOR IS RESPONSIBLE FOR SETTING OUT AND CHECKING ALL LEVELS AND DIMENSIONS ON SITE PRIOR TO COMMENCING ANY SITE WORKS.
- FIGURED DIMENSIONS ARE TO TAKE PREFERENCE OVER SCALE
- DIMENSIONS TO STRUCTURAL TIMBERS & FACE OF BRICKS EXCLUDING BATTENS, PLASTERBOARD ETC.
- ALL DIMENSIONS ON PLAN ARE NOMINAL & MAY VARY TO ACTUAL SIZE
- PROVIDE LOCKS TO ALL OPENABLE WINDOWS & EXTERNAL SLIDING DOORS (KEYED ALIKE).
- MAN HOLE LOCATION MAY BE CHANGED DUE TO TRUSS LAYOUT.
- WINDOW AND DOOR FRAME SIZES ARE NOMINAL AND MAY VARY WITH LONG ISLAND HOMES APPROVED SUPPLIERS.

CLIENT

I / WE.....

CONFIRM THESE DRAWINGS ACCORD WITH OUR REQUIREMENTS AND AUTHORISE THEIR USE FOR NEXT STAGE PURPOSES.

SIGNED..... DATE.....

SIGNED..... DATE.....

SHEET CONTENT:

FLOORING - FIRST FLOOR

HOUSE TYPE: SANYA 380 MIN LOT WIDTH: 12M

PROPERTY ADDRESS:
2251 SKODA CIRCUIT
POINTCOOK

CLIENT:
CLARE FRANSIS & CHRISTPHER
KEVIN GRIFFITHS

NORTH:

FACADE:

SCALE: 1 : 100

DATE:

SHEET NUMBER:

6.2


JOB NUMBER:

JOB ISSUE:


H

REVISIONS


ISSUE	DATE	REVISION DESCRIPTION	INITIALS
A	19.04.21	MASTER	FT
B	29.07.21	R & C	CM
C	04.08.21	R & C ADD AREA	CM
D	20.09.21	COLOUR, PRE CONTRACT CLARIFICATION 06/09/21	CM
E	27.09.21	ENERGY UPGRADES (OPT 2) & CLARIFICATION 27.09.21	CM
F	27.09.21	WIR DOOR	CM
G	29.09.21	ADDED ENGINEERING	CM
H	27.10.21	CONTRACT QUOTE COMMENTS	CM

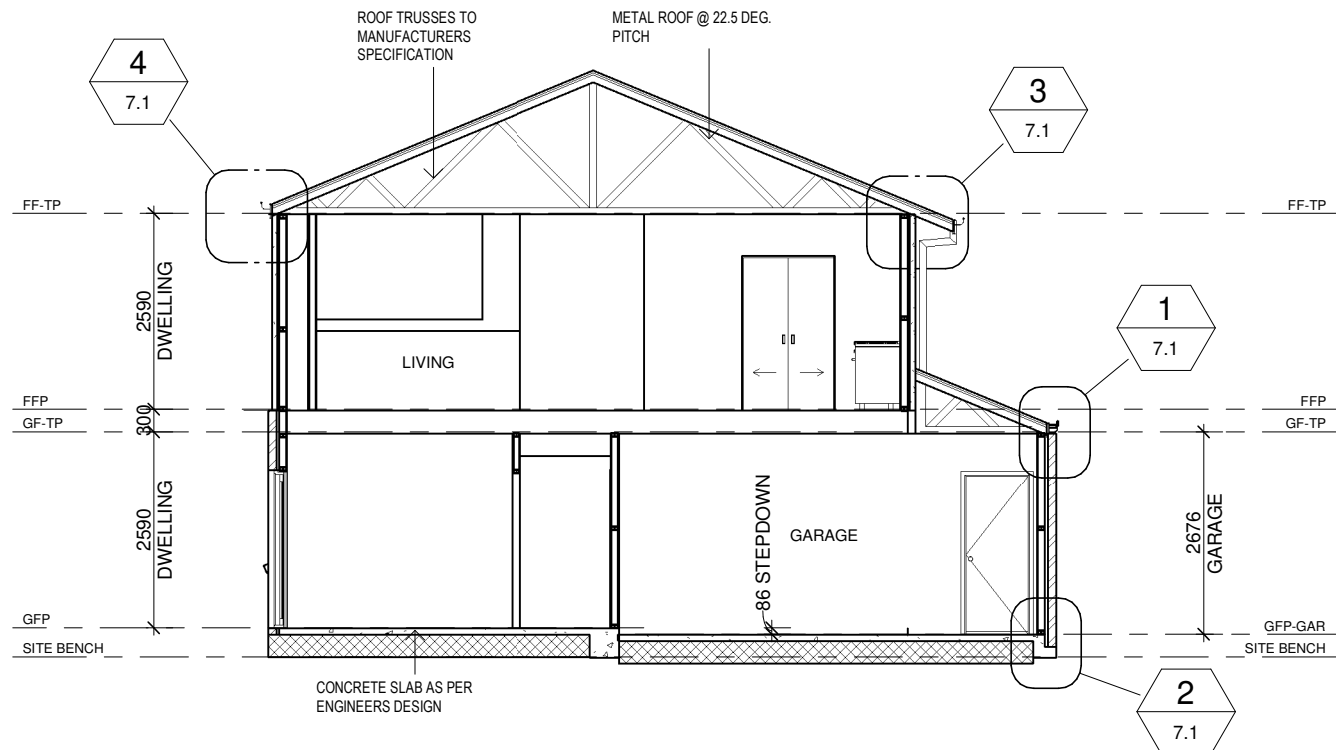


SECTION A
SCALE 1 : 100

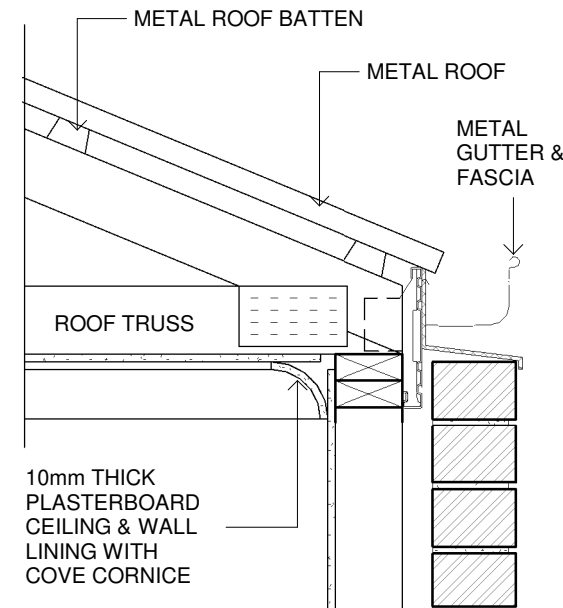


1 GUTTER ON BRICK
1 : 10

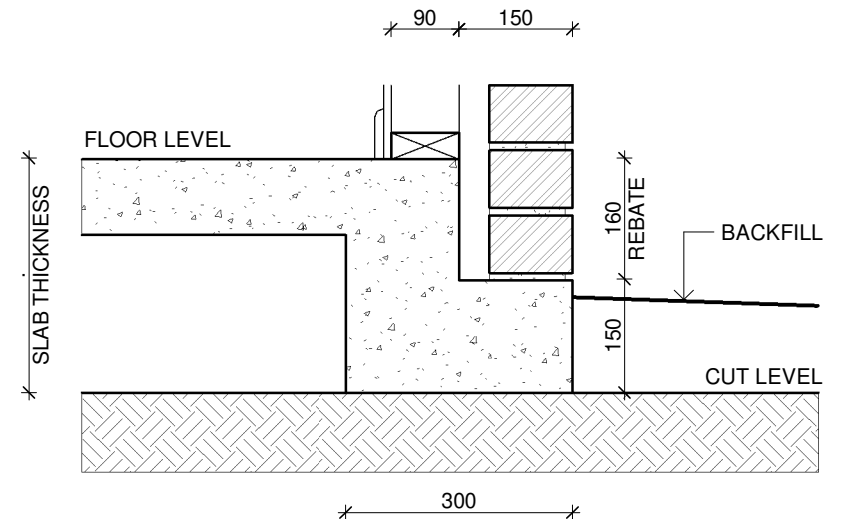

2 BRICK REBATE - TYPICAL
1 : 10

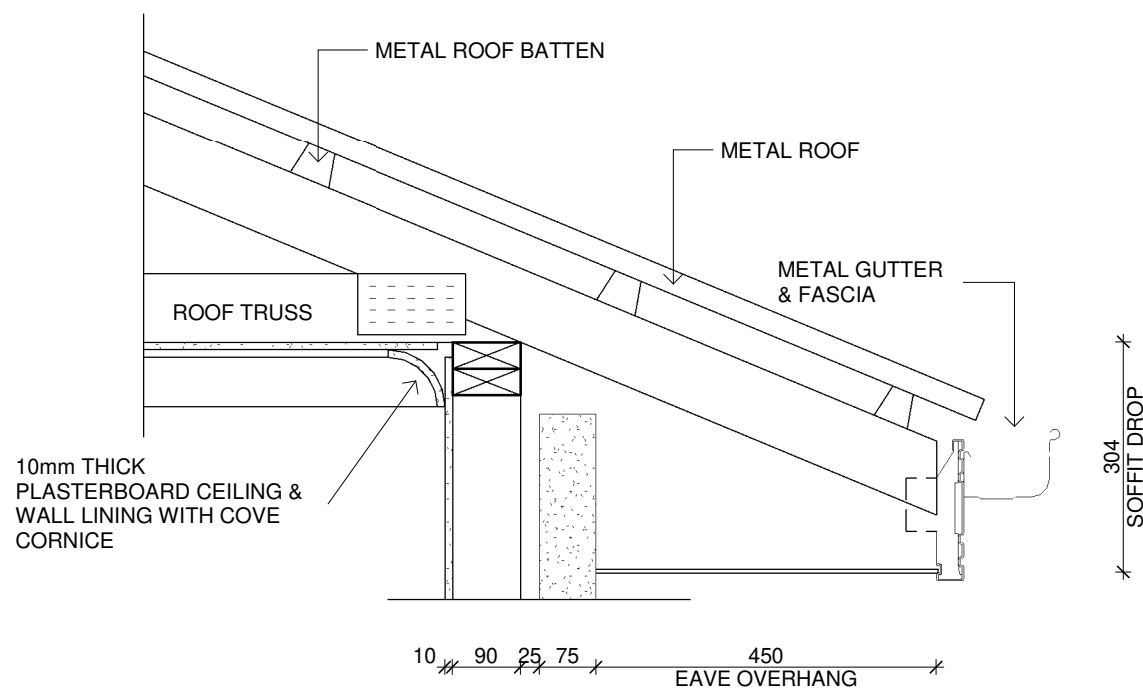

3 450mm EAVE DETAIL
1 : 10

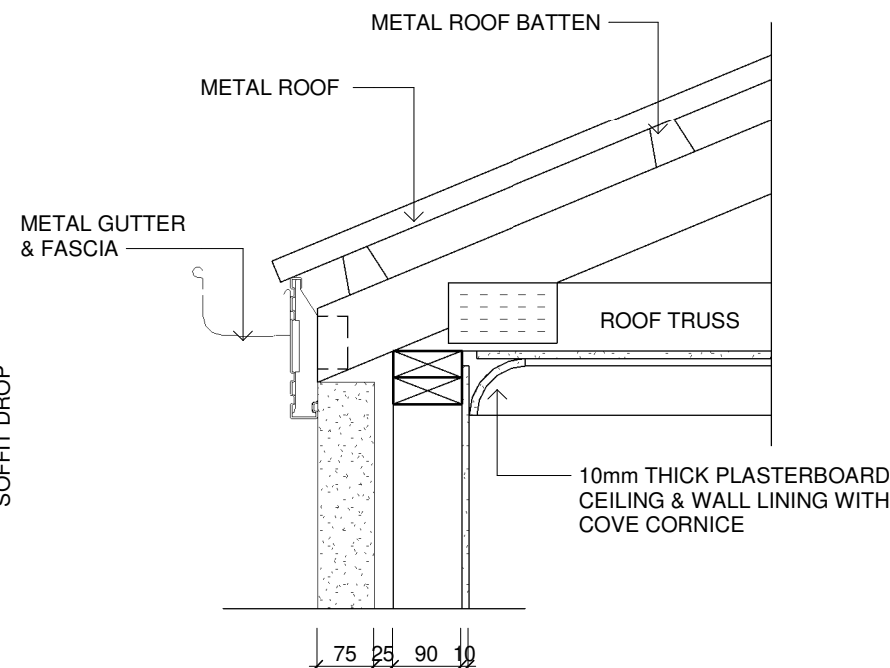

4 NO EAVE DETAIL
1 : 10



Long Island Homes Pty. Ltd.
PO BOX 6269
Point Cook, Vic 3030
p. 61 3 9369 6486 (1800 604 011)
f. 61 3 9369 0994
email: admin@longislandhomes.com.au
www.longislandhomes.com.au

© Copyright
THIS DESIGN & DRAWING SHALL REMAIN THE INTELLECTUAL PROPERTY OF
LONG ISLAND HOMES PTY. LTD. AND SHALL NOT BE COPIED IN WHOLE OR
PART WITHOUT WRITTEN CONSENT FROM LONG ISLAND HOMES PTY LTD.
DB NUMBER

GENERAL NOTES:

- THE CONTRACTOR IS RESPONSIBLE FOR SETTING OUT AND CHECKING ALL LEVELS AND DIMENSIONS ON SITE PRIOR TO COMMENCING ANY SITE WORKS.
- FIGURED DIMENSIONS ARE TO TAKE PREFERENCE OVER SCALE
- DIMENSIONS TO STRUCTURAL TIMBERS & FACE OF BRICKS EXCLUDING BATTENS, PLASTERBOARD ETC.
- ALL DIMENSIONS ON PLAN ARE NOMINAL & MAY VARY TO ACTUAL SIZE
- PROVIDE LOCKS TO ALL OPENABLE WINDOWS & EXTERNAL SLIDING DOORS (KEYED ALIKE).
- MAN HOLE LOCATION MAY BE CHANGED DUE TO TRUSS LAYOUT.
- WINDOW AND DOOR FRAME SIZES ARE NOMINAL AND MAY VARY WITH LONG ISLAND HOMES APPROVED SUPPLIERS.

CLIENT

SIGN OFF

I / WE.....
CONFIRM THESE DRAWINGS ACCORD WITH OUR REQUIREMENTS AND AUTHORISE THEIR USE FOR NEXT STAGE PURPOSES.
SIGNED..... DATE.....
SIGNED..... DATE.....

SHEET CONTENT:

SECTIONS

HOUSE TYPE: **SANYA 380** MIN LOT WIDTH: **12M**
PROPERTY ADDRESS: **2251 SKODA CIRCUIT POINTCOOK**
CLIENT: **CLARE FRANSIS & CHRISTPHER KEVIN GRIFFITHS**

NORTH:

FACADE:
SCALE: As indicated
DATE:

SHEET NUMBER:


7.1

JOB NUMBER:

JOB ISSUE:

H


REVISIONS	ISSUE	DATE	REVISION DESCRIPTION	INITIALS
A	19.04.21		MASTER	FT
B	29.07.21		R & C	CM
C	04.08.21		R & C ADD AREA	CM
D	20.09.21		COLOUR, PRE CONTRACT CLARIFICATION 06/09/21	CM
E	27.09.21		ENERGY UPGRADES (OPT 2) & CLARIFICATION 27.09.21	CM
F	27.09.21		WIR DOOR	CM
G	29.09.21		ADDED ENGINEERING	CM
H	27.10.21		CONTRACT QUOTE COMMENTS	CM

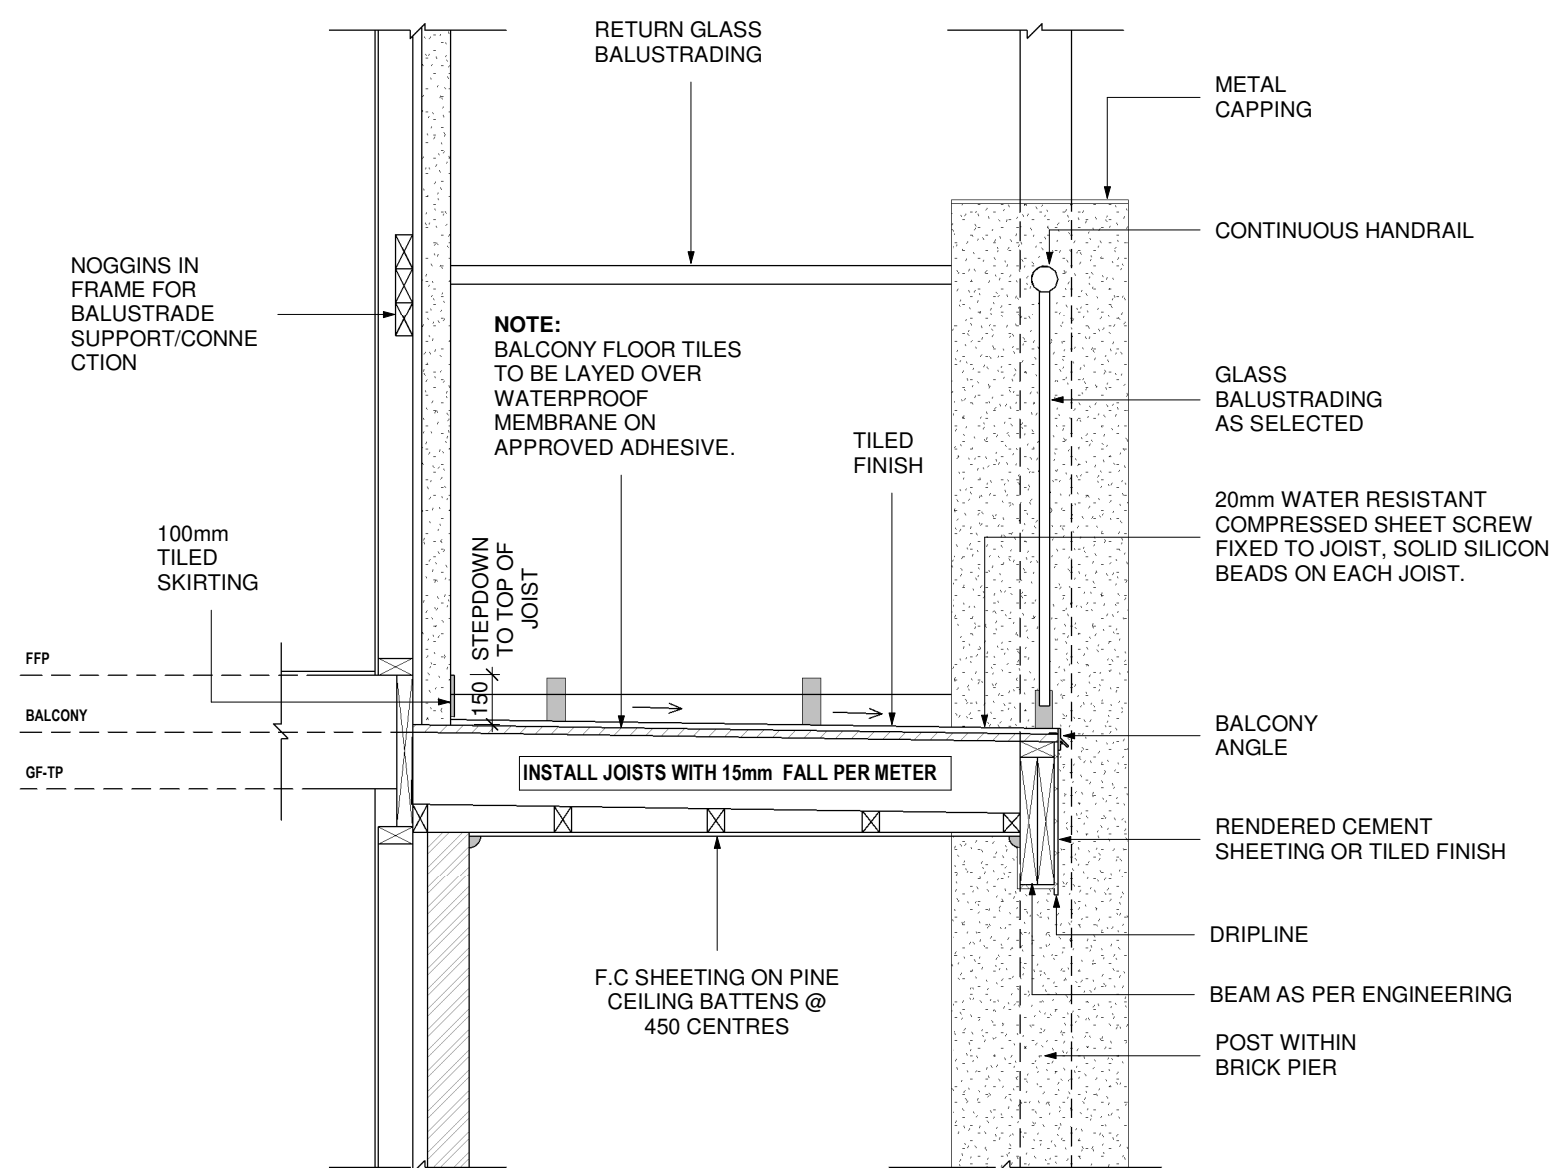

BALCONY DETAIL
SCALE 1 : 20


27/10/2021 8:44:56 AM J:\LONG ISLAND JOBS\2251 Skoda Circuit, Point Cook\DRAWING\2251SKO_REV H.rvt

 ISLANDER	Long Island Homes Pty. Ltd. PO BOX 6269 Point Cook, Vic 3030 p. 61 3 9369 6486 (1800 604 011) f. 61 3 9369 0994 email: admin@longislandhomes.com.au www.longislandhomes.com.au	GENERAL NOTES: - THE CONTRACTOR IS RESPONSIBLE FOR SETTING OUT AND CHECKING ALL LEVELS AND DIMENSIONS ON SITE PRIOR TO COMMENCING ANY SITE WORKS. - FIGURED DIMENSIONS ARE TO TAKE PREFERENCE OVER SCALE - DIMENSIONS TO STRUCTURAL TIMBERS & FACE OF BRICKS EXCLUDING BATTENS, PLASTERBOARD ETC. - ALL DIMENSIONS ON PLAN ARE NOMINAL & MAY VARY TO ACTUAL SIZE - PROVIDE LOCKS TO ALL OPENABLE WINDOWS & EXTERNAL SLIDING DOORS (KEYED ALIKE). - MAN HOLE LOCATION MAY BE CHANGED DUE TO TRUSS LAYOUT. - WINDOW AND DOOR FRAME SIZES ARE NOMINAL AND MAY VARY WITH LONG ISLAND HOMES APPROVED SUPPLIERS.	CLIENT I / WE..... CONFIRM THESE DRAWINGS ACCORD WITH OUR REQUIREMENTS AND AUTHORISE THEIR USE FOR NEXT STAGE PURPOSES. SIGNED..... DATE..... SIGNED..... DATE.....	SHEET CONTENT: BALCONY DETAILS HOUSE TYPE: SANYA 380 MIN LOT WIDTH: 12M PROPERTY ADDRESS: 2251 SKODA CIRCUIT POINTCOOK CLIENT: CLARE FRANSIS & CHRISTPHER KEVIN GRIFFITHS	NORTH: FACADE: SCALE: 1 : 20 DATE:	SHEET NUMBER: 7.3 JOB NUMBER: H	<table><tr><th>ISSUE</th><th>DATE</th><th>REVISION DESCRIPTION</th><th>INITIALS</th></tr><tr><td>A</td><td>19.04.21</td><td>MASTER</td><td>FT</td></tr><tr><td>B</td><td>29.07.21</td><td>R & C</td><td>CM</td></tr><tr><td>C</td><td>04.08.21</td><td>R & C ADD AREA</td><td>CM</td></tr><tr><td>D</td><td>20.09.21</td><td>COLOUR, PRE CONTRACT CLARIFICATION 06/09/21</td><td>CM</td></tr><tr><td>E</td><td>27.09.21</td><td>ENERGY UPGRADES (OPT 2) & CLARIFICATION 27.09.21</td><td>CM</td></tr><tr><td>F</td><td>27.09.21</td><td>WIR DOOR</td><td>CM</td></tr><tr><td>G</td><td>29.09.21</td><td>ADDED ENGINEERING</td><td>CM</td></tr><tr><td>H</td><td>27.10.21</td><td>CONTRACT QUOTE COMMENTS</td><td>CM</td></tr></table>	ISSUE	DATE	REVISION DESCRIPTION	INITIALS	A	19.04.21	MASTER	FT	B	29.07.21	R & C	CM	C	04.08.21	R & C ADD AREA	CM	D	20.09.21	COLOUR, PRE CONTRACT CLARIFICATION 06/09/21	CM	E	27.09.21	ENERGY UPGRADES (OPT 2) & CLARIFICATION 27.09.21	CM	F	27.09.21	WIR DOOR	CM	G	29.09.21	ADDED ENGINEERING	CM	H	27.10.21	CONTRACT QUOTE COMMENTS	CM
	ISSUE	DATE	REVISION DESCRIPTION	INITIALS																																							
	A	19.04.21	MASTER	FT																																							
	B	29.07.21	R & C	CM																																							
	C	04.08.21	R & C ADD AREA	CM																																							
D	20.09.21	COLOUR, PRE CONTRACT CLARIFICATION 06/09/21	CM	
E	27.09.21	ENERGY UPGRADES (OPT 2) & CLARIFICATION 27.09.21	CM	
F	27.09.21	WIR DOOR	CM	
G	29.09.21	ADDED ENGINEERING	CM	
H	27.10.21	CONTRACT QUOTE COMMENTS	CM	
© Copyright THIS DESIGN & DRAWING SHALL REMAIN THE INTELLECTUAL PROPERTY OF LONG ISLAND HOMES PTY. LTD. AND SHALL NOT BE COPIED IN WHOLE OR PART WITHOUT WRITTEN CONSENT FROM LONG ISLAND HOMES PTY LTD. DB NUMBER		SIGN OFF	REVISIONS	

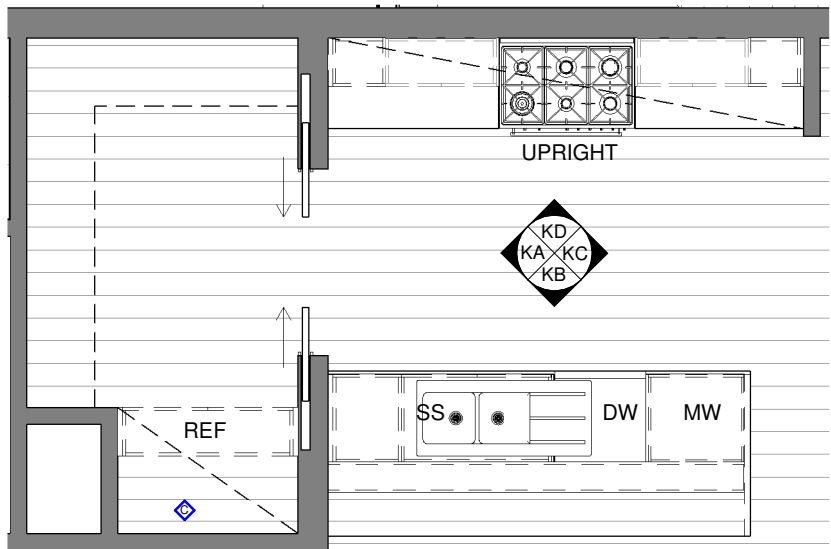


KITCHEN PLAN
SCALE 1 : 50


- NOTE:**
- PROVIDE SOFT CLOSE MECHANISM TO KITCHEN CABINETRY DOORS ONLY
 - PROVIDE 9NO. BLUM SOFT CLOSERS TO KITCHEN DRAWERS
 - PROVIDE 20MM OVERHANG TO KITCHEN AND WIP OVERHEADS CABINETRY ONLY - FINGER PULLS IN LIEU OF HANDLES.
 - PROVIDE CAPPED COLD WATER POINT TO FRIDGE SPACE

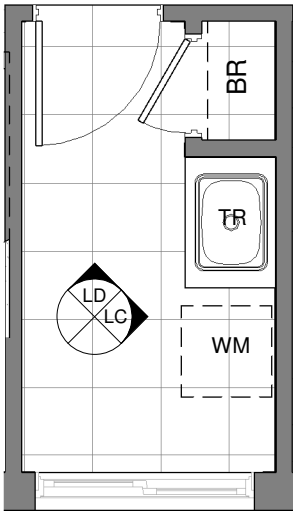


L'DRY PLAN
SCALE 1 : 50

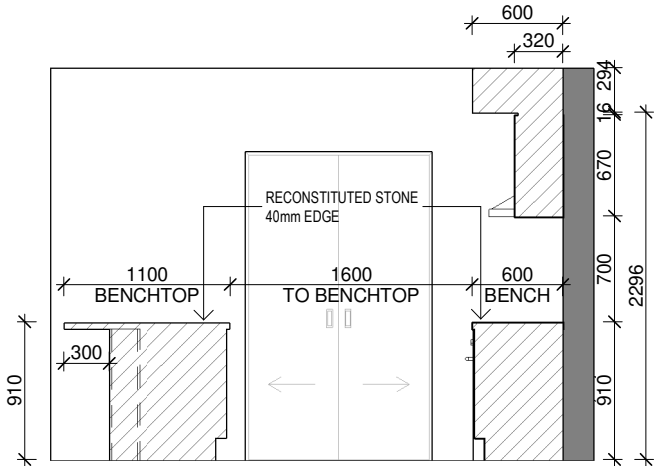


ELEVATION - KA
KITCHEN ELEVATIONS

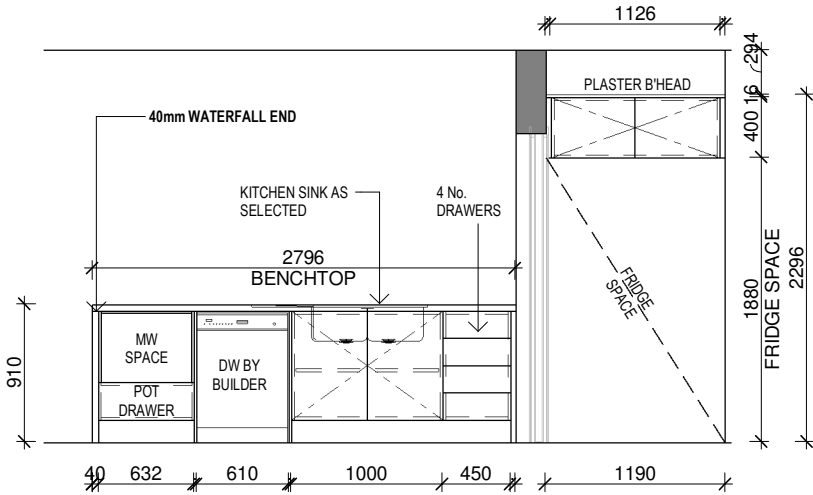


ELEVATION - KB

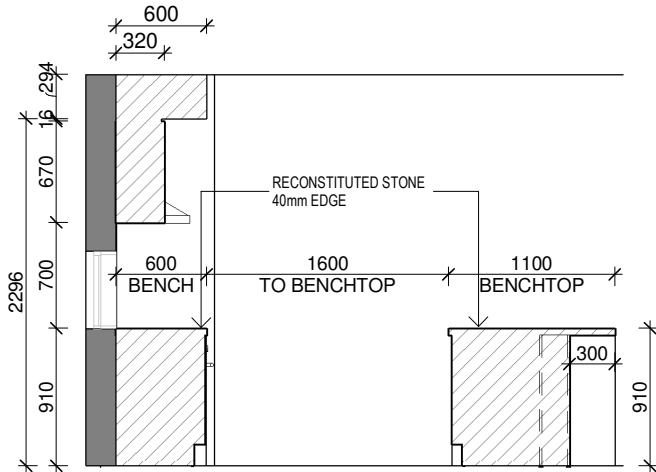


ELEVATION - KC

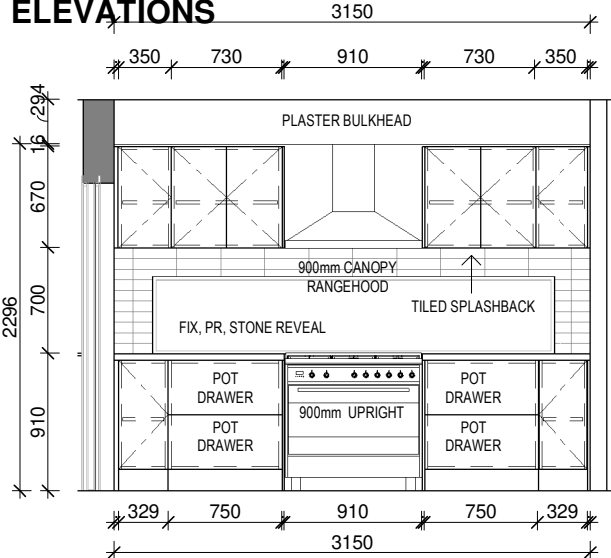


ELEVATION - KD

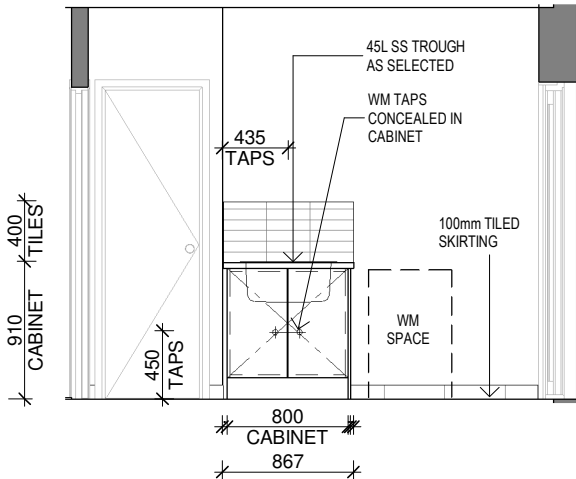

ELEVATION - LC
LAUNDRY ELEVATIONS

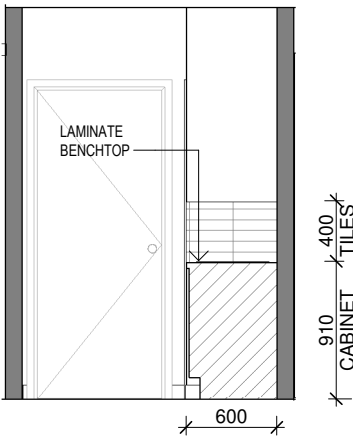

ELEVATION - LD

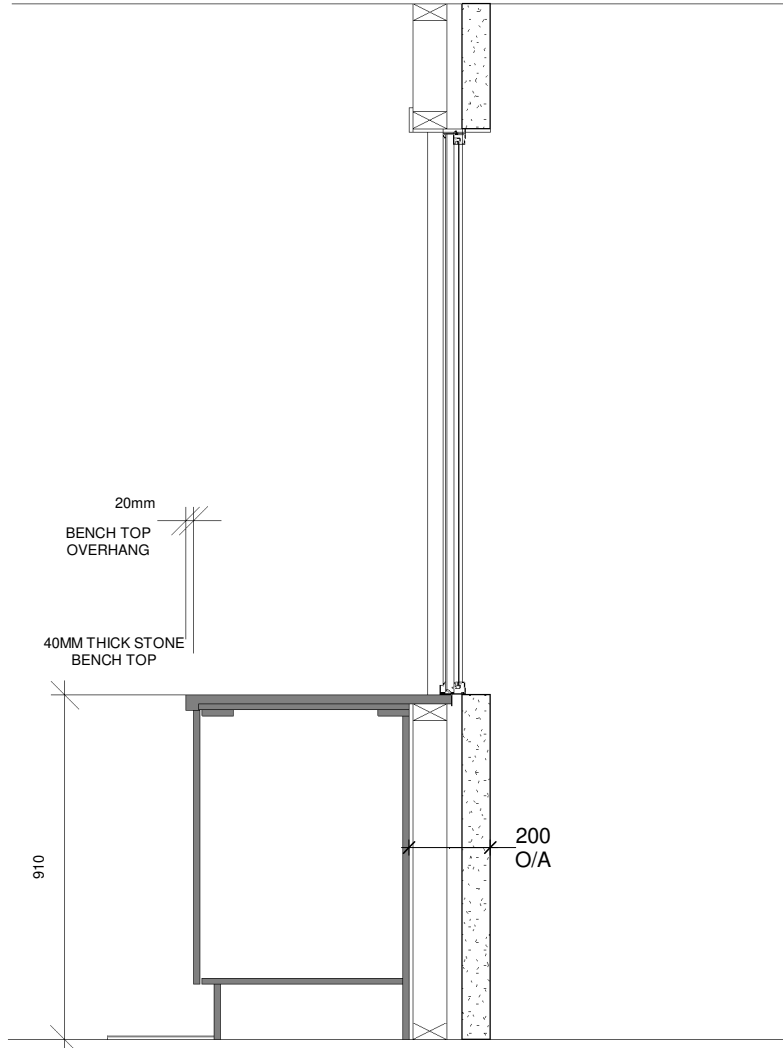

STONE REVEAL DETAIL
SCALE 1 : 20



Long Island Homes Pty. Ltd.
PO BOX 6269
Point Cook, Vic 3030
p. 61 3 9369 6486 (1800 604 011)
f. 61 3 9369 0994
email: admin@longislandhomes.com.au
www.longislandhomes.com.au

© Copyright
THIS DESIGN & DRAWING SHALL REMAIN THE INTELLECTUAL PROPERTY OF
LONG ISLAND HOMES PTY. LTD. AND SHALL NOT BE COPIED IN WHOLE OR
PART WITHOUT WRITTEN CONSENT FROM LONG ISLAND HOMES PTY LTD.
DB NUMBER

GENERAL NOTES:

- THE CONTRACTOR IS RESPONSIBLE FOR SETTING OUT AND CHECKING ALL LEVELS AND DIMENSIONS ON SITE PRIOR TO COMMENCING ANY SITE WORKS.
- FIGURED DIMENSIONS ARE TO TAKE PREFERENCE OVER SCALE
- DIMENSIONS TO STRUCTURAL TIMBERS & FACE OF BRICKS EXCLUDING BATTENS, PLASTERBOARD ETC.
- ALL DIMENSIONS ON PLAN ARE NOMINAL & MAY VARY TO ACTUAL SIZE
- PROVIDE LOCKS TO ALL OPENABLE WINDOWS & EXTERNAL SLIDING DOORS (KEYED ALIKE).
- MAN HOLE LOCATION MAY BE CHANGED DUE TO TRUSS LAYOUT.
- WINDOW AND DOOR FRAME SIZES ARE NOMINAL AND MAY VARY WITH LONG ISLAND HOMES APPROVED SUPPLIERS.

CLIENT

I / WE.....

CONFIRM THESE DRAWINGS ACCORD WITH OUR REQUIREMENTS AND AUTHORISE THEIR USE FOR NEXT STAGE PURPOSES.

SIGNED..... DATE.....

SIGNED..... DATE.....

SHEET CONTENT:


KITCHEN, LAUNDRY

HOUSE TYPE: **SANYA 380** MIN LOT WIDTH: **12M**


PROPERTY ADDRESS: **2251 SKODA CIRCUIT POINTCOOK**

CLIENT: **CLARE FRANSIS & CHRISTPHER KEVIN GRIFFITHS**


NORTH:		FACADE:		SHEET NUMBER: 8.1	JOB NUMBER:
		SCALE: As indicated			JOB ISSUE: H
		DATE:			
REVISIONS	ISSUE	DATE	REVISION DESCRIPTION		INITIALS
	A	19.04.21	MASTER		FT
	B	29.07.21	R & C		CM
	C	04.08.21	R & C ADD AREA		CM
	D	20.09.21	COLOUR, PRE CONTRACT CLARIFICATION 06/09/21		CM
	E	27.09.21	ENERGY UPGRADES (OPT 2) & CLARIFICATION 27.09.21		CM
	F	27.09.21	WIR DOOR		CM
	G	29.09.21	ADDED ENGINEERING		CM
	H	27.10.21	CONTRACT QUOTE COMMENTS		CM

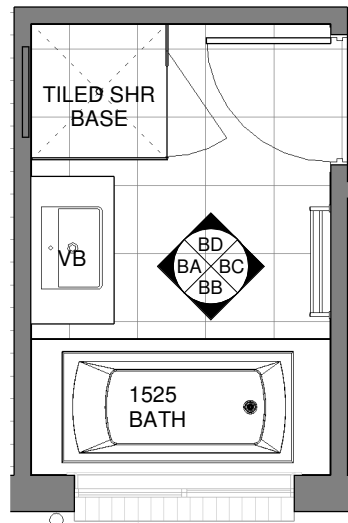


1135
MIRROR APPROX.
870
CABINET
505
HOB
400
TILES

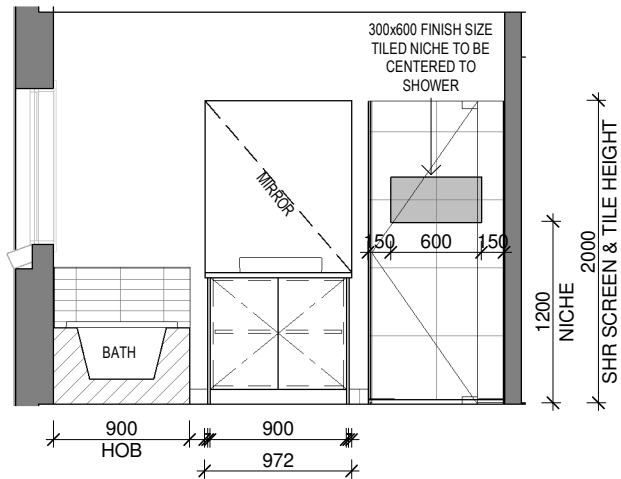


ELEVATION - BA

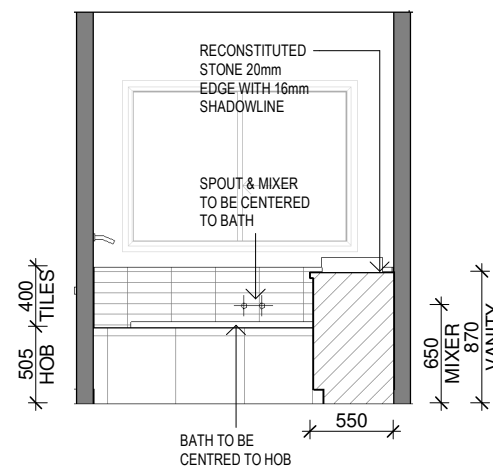

ELEVATION - BB

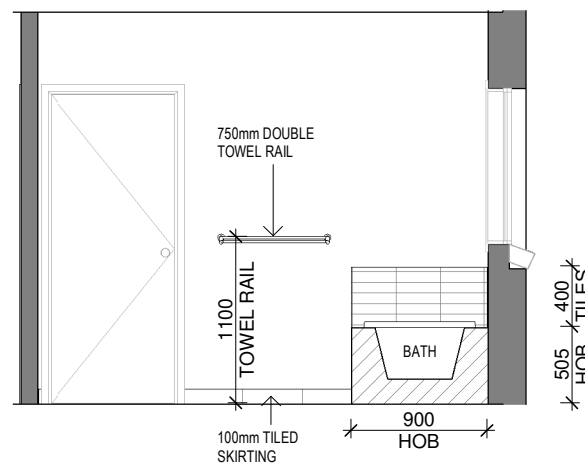



ELEVATION - BC

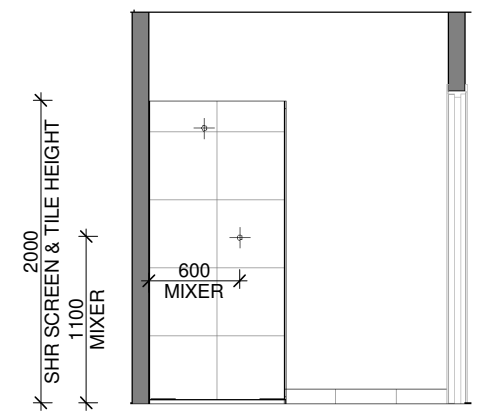


ELEVATION - BD

BATH PLAN SCALE 1 : 50


BATHROOM ELEVATIONS

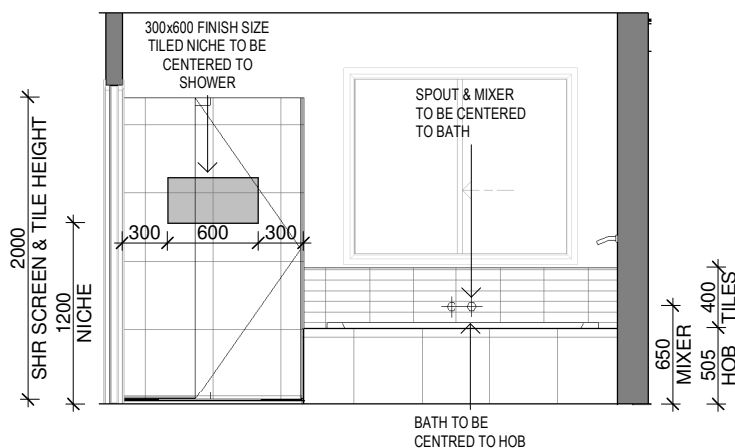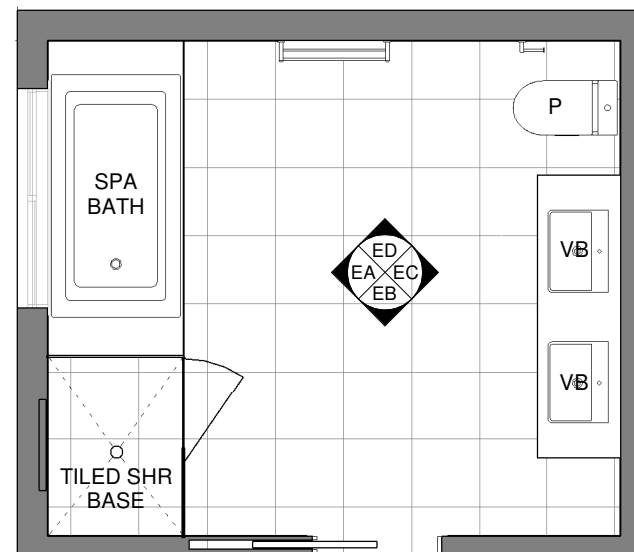

ELEVATION - EA
ENSUITE ELEVATIONS

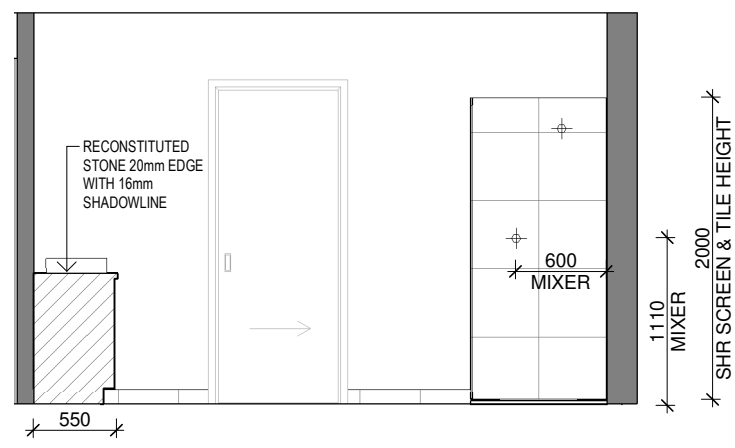


ELEVATION - EB

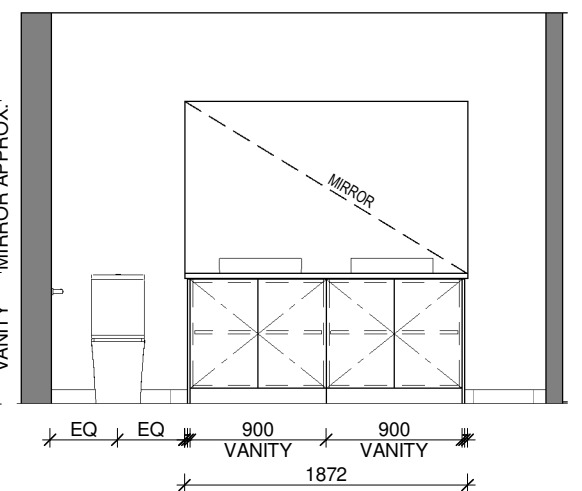


ELEVATION - EC


ENSUITE 1 PLAN SCALE 1 : 50

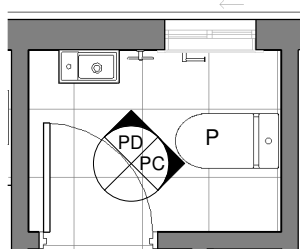


PDR PLAN
SCALE 1 : 50

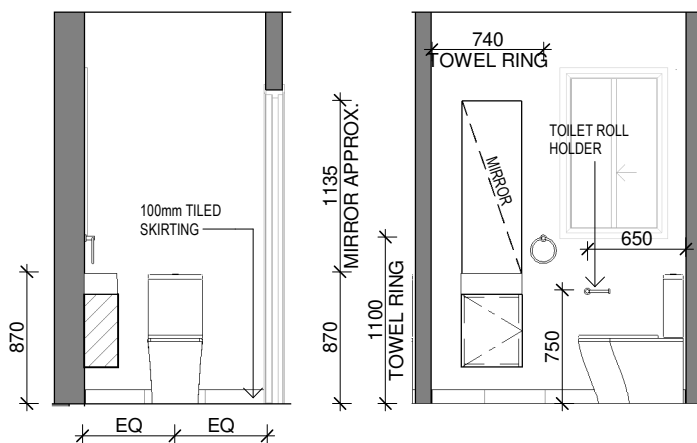

ELEVATION - PC

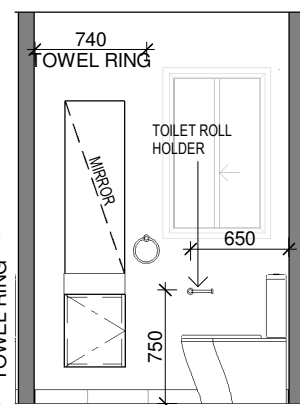

ELEVATION - PD

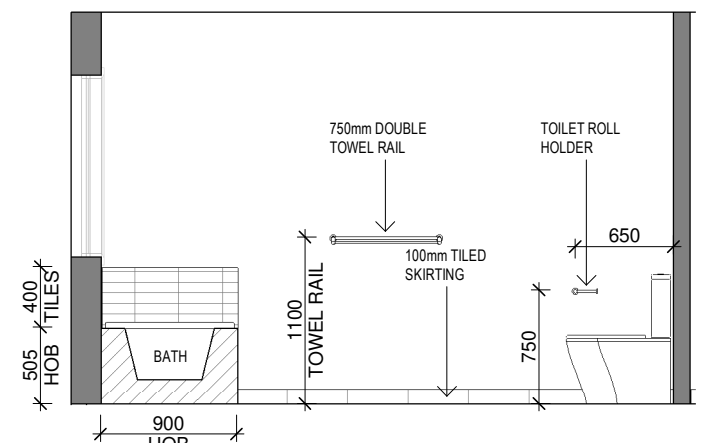

ELEVATION - ED

PDR ELEVATIONS



Long Island Homes Pty. Ltd.
PO BOX 6269
Point Cook, Vic 3030
p. 61 3 9369 6486 (1800 604 011)
f. 61 3 9369 0994
email: admin@longislandhomes.com.au
www.longislandhomes.com.au

© Copyright
THIS DESIGN & DRAWING SHALL REMAIN THE INTELLECTUAL PROPERTY OF
LONG ISLAND HOMES PTY. LTD. AND SHALL NOT BE COPIED IN WHOLE OR
PART WITHOUT WRITTEN CONSENT FROM LONG ISLAND HOMES PTY LTD.
DB NUMBER

GENERAL NOTES:

- THE CONTRACTOR IS RESPONSIBLE FOR SETTING OUT AND CHECKING ALL LEVELS AND DIMENSIONS ON SITE PRIOR TO COMMENCING ANY SITE WORKS.
- FIGURED DIMENSIONS ARE TO TAKE PREFERENCE OVER SCALE
- DIMENSIONS TO STRUCTURAL TIMBERS & FACE OF BRICKS EXCLUDING BATTENS, PLASTERBOARD ETC.
- ALL DIMENSIONS ON PLAN ARE NOMINAL & MAY VARY TO ACTUAL SIZE
- PROVIDE LOCKS TO ALL OPENABLE WINDOWS & EXTERNAL SLIDING DOORS (KEYED ALIKE).
- MAN HOLE LOCATION MAY BE CHANGED DUE TO TRUSS LAYOUT.
- WINDOW AND DOOR FRAME SIZES ARE NOMINAL AND MAY VARY WITH LONG ISLAND HOMES APPROVED SUPPLIERS.

CLIENT

I / WE.....
CONFIRM THESE DRAWINGS ACCORD WITH OUR REQUIREMENTS AND AUTHORISE THEIR USE FOR NEXT STAGE PURPOSES.
SIGNED..... DATE.....
SIGNED..... DATE.....

SHEET CONTENT:

BATH, ENS1 & PDR

HOUSE TYPE:
SANYA 380

MIN LOT WIDTH:
12M

PROPERTY ADDRESS:
2251 SKODA CIRCUIT
POINTCOOK

CLIENT:

CLARE FRANSIS & CHRISTPHER
KEVIN GRIFFITHS

NORTH:

FACADE:

SCALE: 1 : 50

DATE:

SHEET NUMBER:


8.2

JOB NUMBER:


JOB ISSUE:

H


ISSUE	DATE	REVISION DESCRIPTION	INITIALS
A	19.04.21	MASTER	FT
B	29.07.21	R & C	CM
C	04.08.21	R & C ADD AREA	CM
D	20.09.21	COLOUR, PRE CONTRACT CLARIFICATION 06/09/21	CM
E	27.09.21	ENERGY UPGRADES (OPT 2) & CLARIFICATION 27.09.21	CM
F	27.09.21	WIR DOOR	CM
G	29.09.21	ADDED ENGINEERING	CM
H	27.10.21	CONTRACT QUOTE COMMENTS	CM

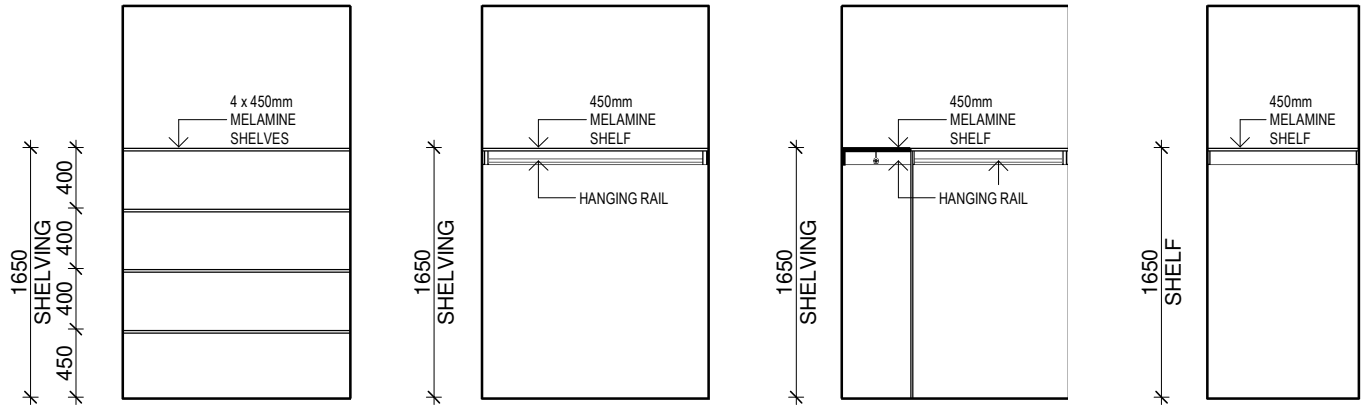


PANTRY / LINEN
ROBE
TYPICAL INTERNAL ELEVATIONS

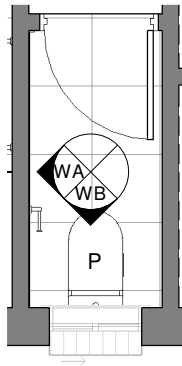

WC PLAN
SCALE 1 : 50

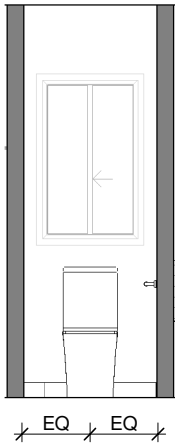

ELEVATION - WB
WC ELEVATIONS

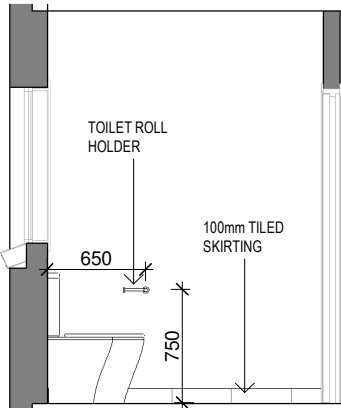

ELEVATION - WA



Long Island Homes Pty. Ltd.
PO BOX 6269
Point Cook, Vic 3030
p. 61 3 9369 6486 (1800 604 011)
f. 61 3 9369 0994
email: admin@longislandhomes.com.au
www.longislandhomes.com.au

© Copyright
THIS DESIGN & DRAWING SHALL REMAIN THE INTELLECTUAL PROPERTY OF
LONG ISLAND HOMES PTY. LTD. AND SHALL NOT BE COPIED IN WHOLE OR
PART WITHOUT WRITTEN CONSENT FROM LONG ISLAND HOMES PTY LTD.
DB NUMBER

GENERAL NOTES:

- THE CONTRACTOR IS RESPONSIBLE FOR SETTING OUT AND CHECKING ALL LEVELS AND DIMENSIONS ON SITE PRIOR TO COMMENCING ANY SITE WORKS.
- FIGURED DIMENSIONS ARE TO TAKE PREFERENCE OVER SCALE
- DIMENSIONS TO STRUCTURAL TIMBERS & FACE OF BRICKS EXCLUDING BATTENS, PLASTERBOARD ETC.
- ALL DIMENSIONS ON PLAN ARE NOMINAL & MAY VARY TO ACTUAL SIZE
- PROVIDE LOCKS TO ALL OPENABLE WINDOWS & EXTERNAL SLIDING DOORS (KEYED ALIKE).
- MAN HOLE LOCATION MAY BE CHANGED DUE TO TRUSS LAYOUT.
- WINDOW AND DOOR FRAME SIZES ARE NOMINAL AND MAY VARY WITH LONG ISLAND HOMES APPROVED SUPPLIERS.

CLIENT

I / WE.....

CONFIRM THESE DRAWINGS ACCORD WITH OUR REQUIREMENTS AND AUTHORISE THEIR USE FOR NEXT STAGE PURPOSES.

SIGNED..... DATE.....

SIGNED..... DATE.....

SHEET CONTENT:

WC & TYPICAL


HOUSE TYPE: SANYA 380 MIN LOT WIDTH: 12M

PROPERTY ADDRESS: 2251 SKODA CIRCUIT POINTCOOK

CLIENT: CLARE FRANSIS & CHRISTPHER KEVIN GRIFFITHS

NORTH:		FACADE:		SHEET NUMBER: 8.3	JOB NUMBER:
		SCALE: 1 : 50			JOB ISSUE: H
		DATE:			
REVISIONS	ISSUE	DATE	REVISION DESCRIPTION		INITIALS
	E	27.09.21	ENERGY UPGRADES (OPT 2) & CLARIFICATION 27.09.21		CM
	F	27.09.21	WIR DOOR		CM
	G	29.09.21	ADDED ENGINEERING		CM
	H	27.10.21	CONTRACT QUOTE COMMENTS		CM


LANDSCAPE LEGEND

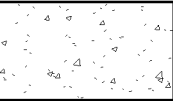


DENOTES PLAIN CONCRETE



DENOTES COLOURED CONCRETE

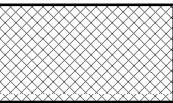


DENOTES EXPOSED AGGREGATE

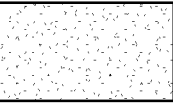

DENOTES DROUGHT TOLERANT PLANTS AND MULCH



DENOTES TOPSOIL / GRASS SEED

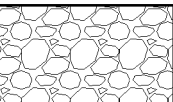


DENOTES CRUSHED ROCK



DENOTES CONCRETE PAVERS

PLANT SCHEDULE

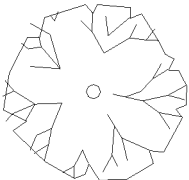

-(MS) MAGNOLIA SOULANGEANA "MAGNOLIA"
45 LITRE, 1.8M HIGH X 1





-(LD) LAVANDULA DENTATA "FRENCH LAVENDER"
150 MM POT SIZE x 9



-(LS) LAVANDULA STOECHAS "LAVENDER DWARF
WINTER PURPLE" 150 MM POT SIZE x 10



-(A0) AGAPANTHUS ORIENTALIS "AGAPANTHUS
DWARF (WHITE)" 150MM POT SIZE x 10

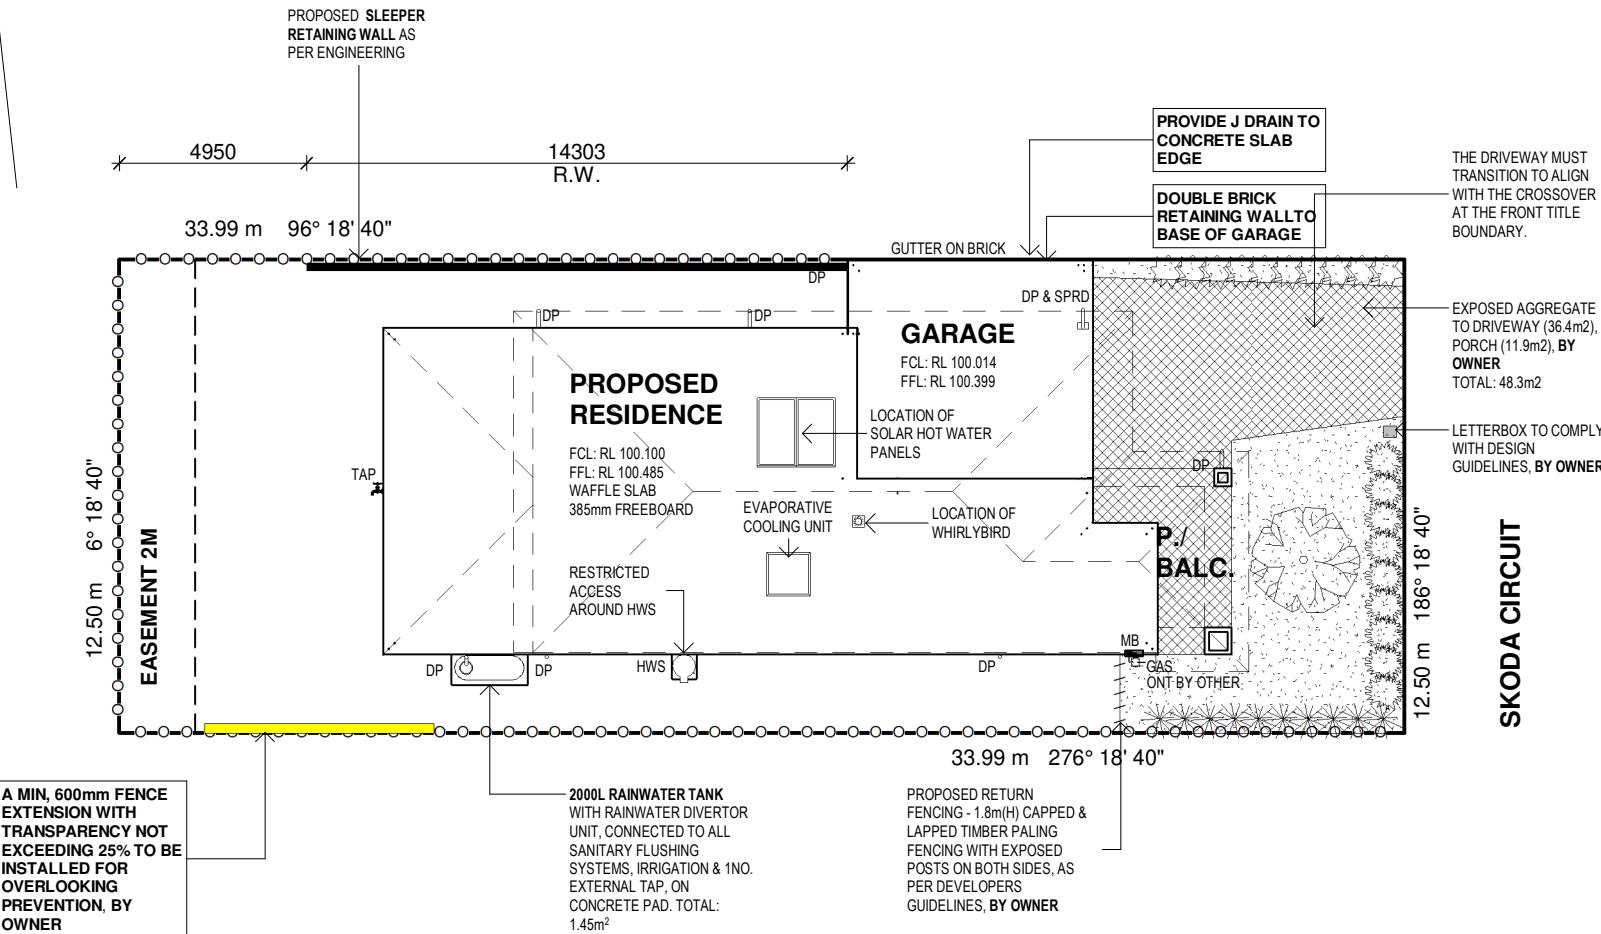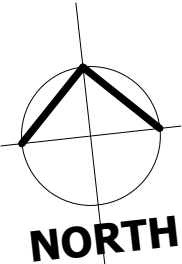

LANDSCAPE PLAN
SCALE 1 : 200



ISLANDER

Long Island Homes Pty. Ltd.
PO BOX 6269
Point Cook, Vic 3030
p. 61 3 9369 6486 (1800 604 011)
f. 61 3 9369 0994
email: admin@longislandhomes.com.au
www.longislandhomes.com.au

© Copyright
THIS DESIGN & DRAWING SHALL REMAIN THE INTELLECTUAL PROPERTY OF
LONG ISLAND HOMES PTY. LTD. AND SHALL NOT BE COPIED IN WHOLE OR
PART WITHOUT WRITTEN CONSENT FROM LONG ISLAND HOMES PTY LTD.
DB NUMBER

GENERAL NOTES:
- THE CONTRACTOR IS RESPONSIBLE FOR SETTING OUT AND CHECKING ALL LEVELS AND DIMENSIONS ON SITE PRIOR TO COMMENCING ANY SITE WORKS.
- FIGURED DIMENSIONS ARE TO TAKE PREFERENCE OVER SCALE
- DIMENSIONS TO STRUCTURAL TIMBERS & FACE OF BRICKS EXCLUDING BATTENS, PLASTERBOARD ETC.
- ALL DIMENSIONS ON PLAN ARE NOMINAL & MAY VARY TO ACTUAL SIZE
- PROVIDE LOCKS TO ALL OPENABLE WINDOWS & EXTERNAL SLIDING DOORS (KEYED ALIKE).
- MAN HOLE LOCATION MAY BE CHANGED DUE TO TRUSS LAYOUT.
- WINDOW AND DOOR FRAME SIZES ARE NOMINAL AND MAY VARY WITH LONG ISLAND HOMES APPROVED SUPPLIERS.

CLIENT

I / WE.....

CONFIRM THESE DRAWINGS ACCORD WITH OUR REQUIREMENTS AND AUTHORISE THEIR USE FOR NEXT STAGE PURPOSES.

SIGNED..... DATE.....

SIGNED..... DATE.....

SHEET CONTENT:


LANDSCAPE PLAN

HOUSE TYPE: SANYA 380 MIN LOT WIDTH: 12M

PROPERTY ADDRESS: 2251 SKODA CIRCUIT POINTCOOK

CLIENT: CLARE FRANSIS & CHRISTPHER KEVIN GRIFFITHS

NORTH:		FACADE:		SHEET NUMBER: 9.1	JOB NUMBER:
		SCALE: As indicated			JOB ISSUE: H
		DATE:			
REVISIONS	ISSUE	DATE	REVISION DESCRIPTION		INITIALS
	A	19.04.21	MASTER		FT
	B	29.07.21	R & C		CM
	C	04.08.21	R & C ADD AREA		CM
	D	20.09.21	COLOUR, PRE CONTRACT CLARIFICATION 06/09/21		CM
	E	27.09.21	ENERGY UPGRADES (OPT 2) & CLARIFICATION 27.09.21		CM
	F	27.09.21	WIR DOOR		CM
	G	29.09.21	ADDED ENGINEERING		CM
	H	27.10.21	CONTRACT QUOTE COMMENTS		CM

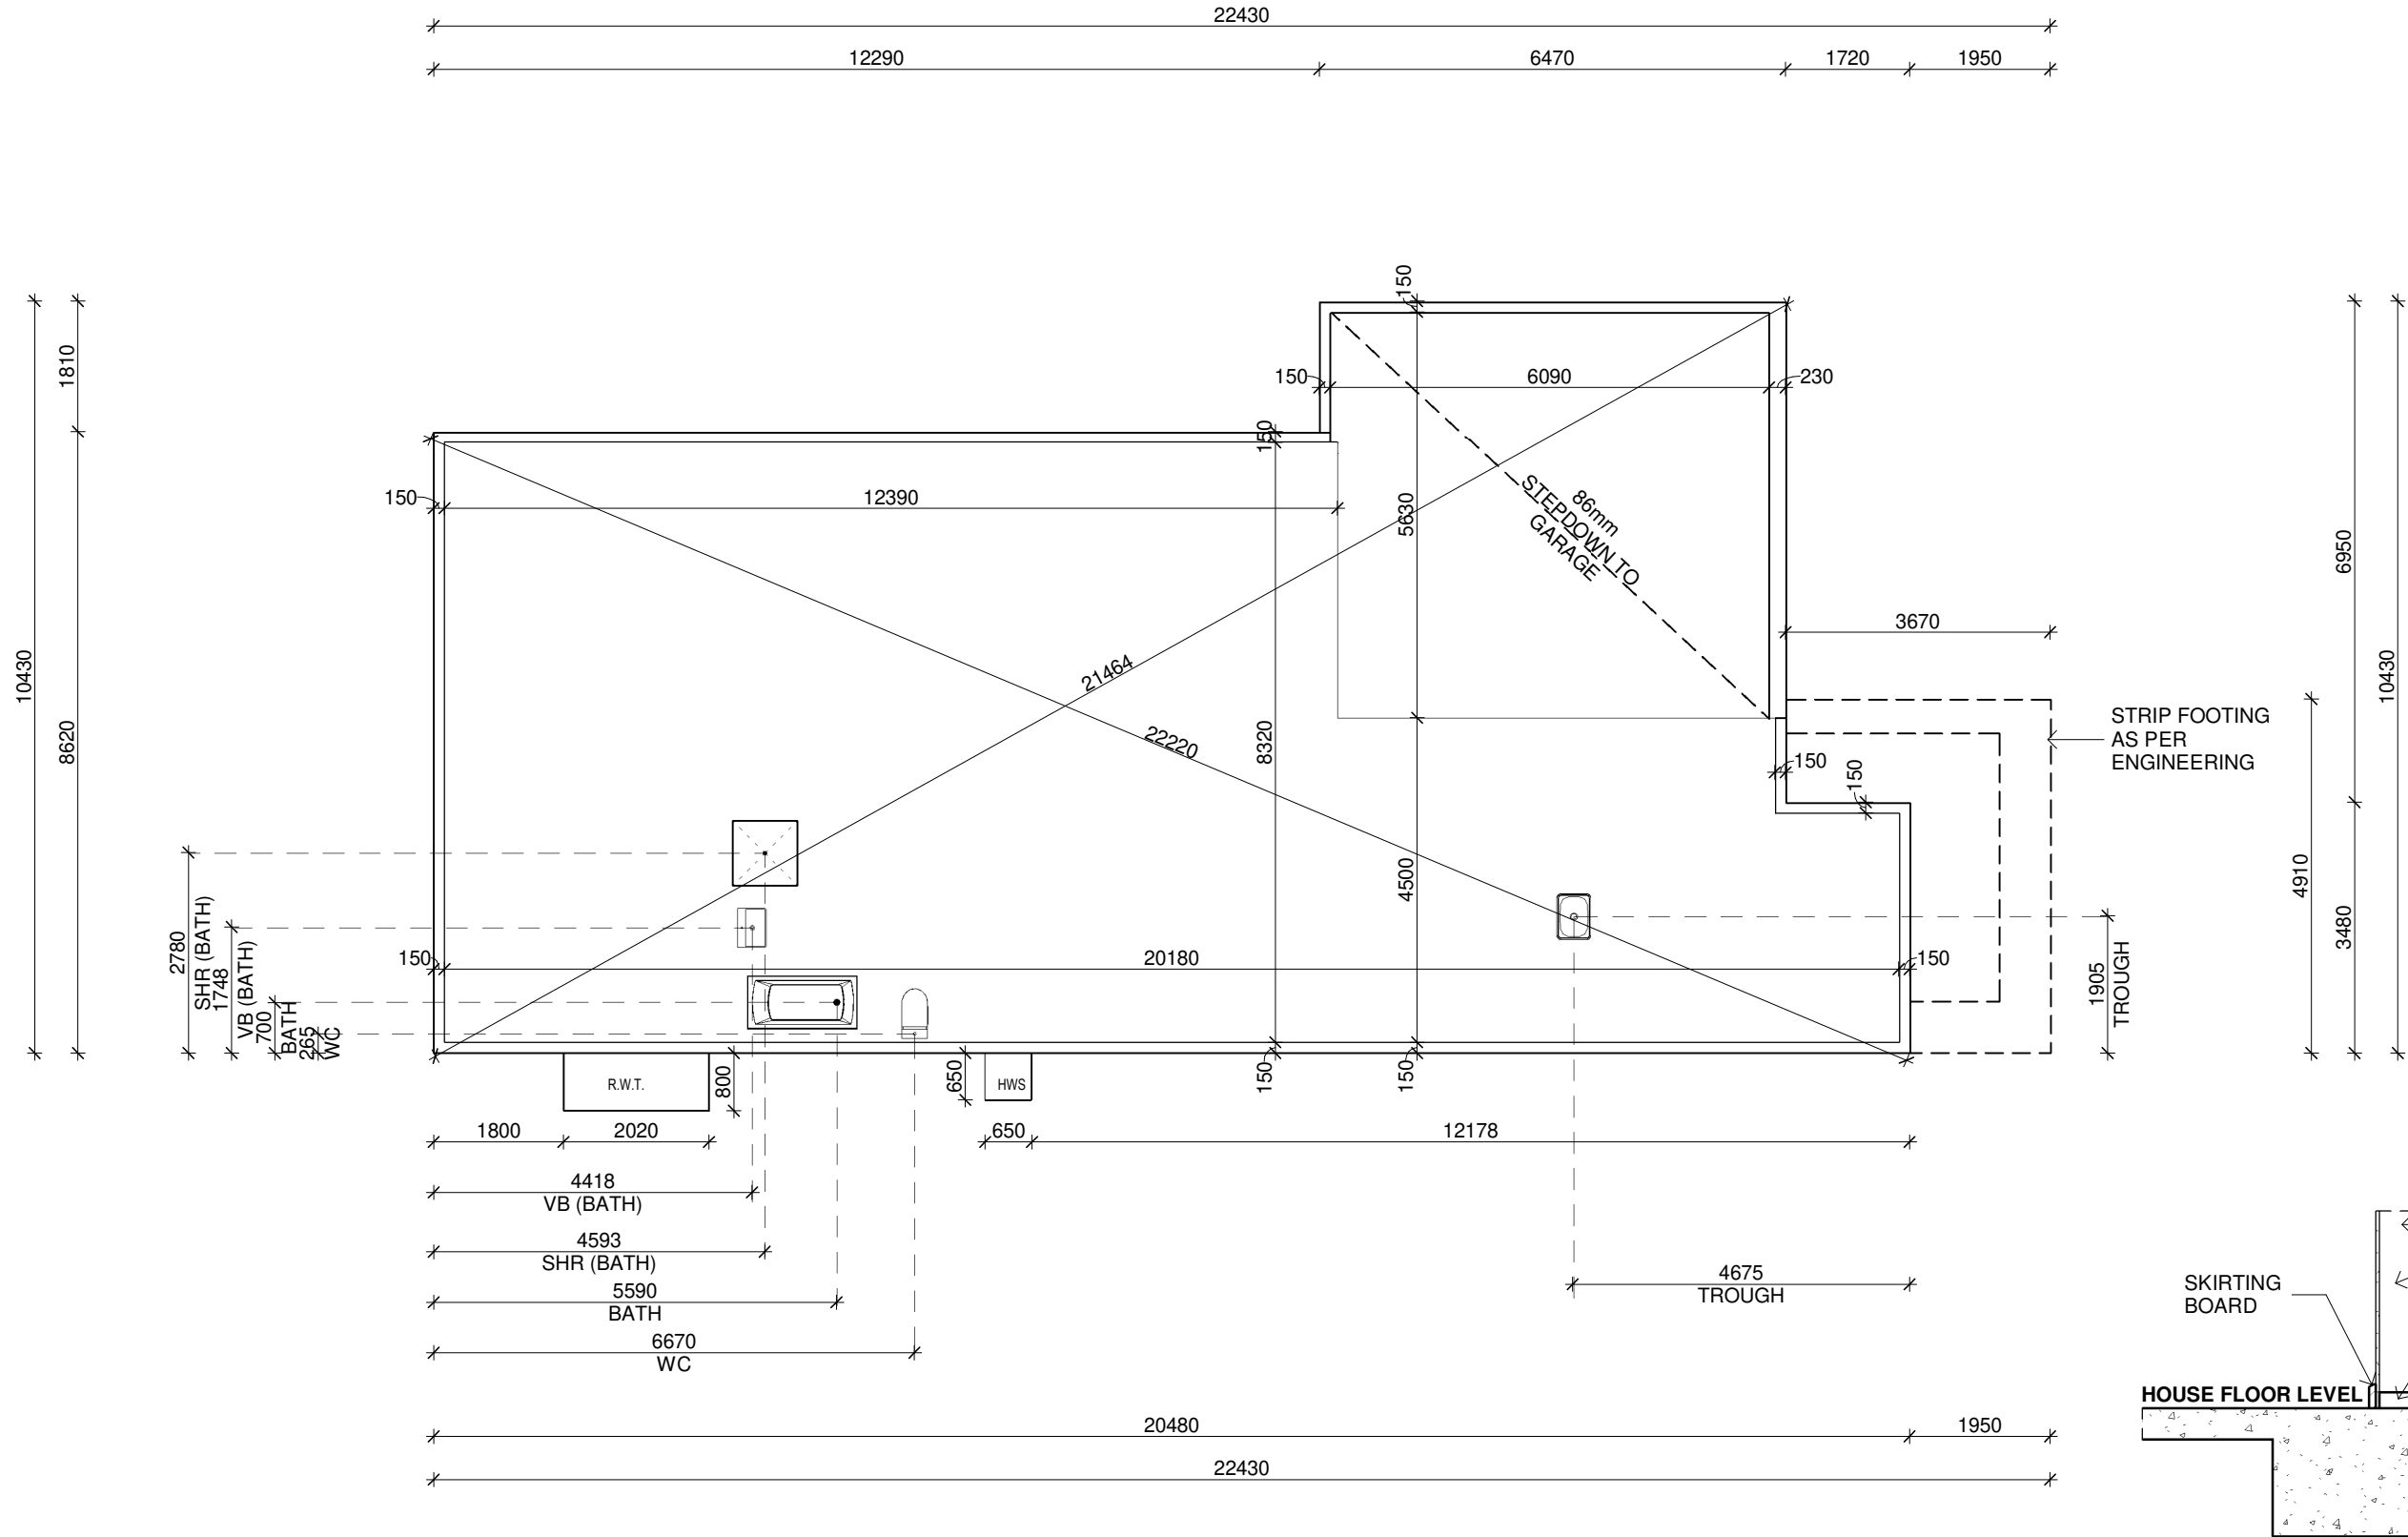

SLAB LAYOUT
SCALE 1 : 100

GARAGE STEPDOWN DETAIL
SCALE 1 : 20



ISLANDER

Long Island Homes Pty. Ltd.
PO BOX 6269
Point Cook, Vic 3030
p. 61 3 9369 6486 (1800 604 011)
f. 61 3 9369 0994
email: admin@longislandhomes.com.au
www.longislandhomes.com.au

© Copyright
THIS DESIGN & DRAWING SHALL REMAIN THE INTELLECTUAL PROPERTY OF
LONG ISLAND HOMES PTY. LTD. AND SHALL NOT BE COPIED IN WHOLE OR
PART WITHOUT WRITTEN CONSENT FROM LONG ISLAND HOMES PTY LTD.
DB NUMBER

GENERAL NOTES:

- THE CONTRACTOR IS RESPONSIBLE FOR SETTING OUT AND CHECKING ALL LEVELS AND DIMENSIONS ON SITE PRIOR TO COMMENCING ANY SITE WORKS.
- FIGURED DIMENSIONS ARE TO TAKE PREFERENCE OVER SCALE
- DIMENSIONS TO STRUCTURAL TIMBERS & FACE OF BRICKS EXCLUDING BATTENS, PLASTERBOARD ETC.
- ALL DIMENSIONS ON PLAN ARE NOMINAL & MAY VARY TO ACTUAL SIZE
- PROVIDE LOCKS TO ALL OPENABLE WINDOWS & EXTERNAL SLIDING DOORS (KEYED ALIKE).
- MAN HOLE LOCATION MAY BE CHANGED DUE TO TRUSS LAYOUT.
- WINDOW AND DOOR FRAME SIZES ARE NOMINAL AND MAY VARY WITH LONG ISLAND HOMES APPROVED SUPPLIERS.

CLIENT

I / WE.....

CONFIRM THESE DRAWINGS ACCORD WITH OUR REQUIREMENTS AND AUTHORISE THEIR USE FOR NEXT STAGE PURPOSES.

SIGNED..... DATE.....

SIGNED..... DATE.....

SHEET CONTENT:

SLAB LAYOUT

HOUSE TYPE: SANYA 380 MIN LOT WIDTH: 12M

PROPERTY ADDRESS: 2251 SKODA CIRCUIT POINTCOOK

CLIENT: CLARE FRANSIS & CHRISTPHER KEVIN GRIFFITHS

NORTH:

FACADE:

SCALE: As indicated

DATE:


SHEET NUMBER: 10.1

JOB NUMBER:


JOB ISSUE: H

ISSUE	DATE	REVISION DESCRIPTION	INITIALS
A	19.04.21	MASTER	FT
B	29.07.21	R & C	CM
C	04.08.21	R & C ADD AREA	CM
D	20.09.21	COLOUR, PRE CONTRACT CLARIFICATION 06/09/21	CM
E	27.09.21	ENERGY UPGRADES (OPT 2) & CLARIFICATION 27.09.21	CM
F	27.09.21	WIR DOOR	CM
G	29.09.21	ADDED ENGINEERING	CM
H	27.10.21	CONTRACT QUOTE COMMENTS	CM


27/10/2021 8:45:00 AM J:\LONG ISLAND JOBS\2251 Skoda Circuit, Point Cook\DRAWING\2251SKO_REV H.rvt

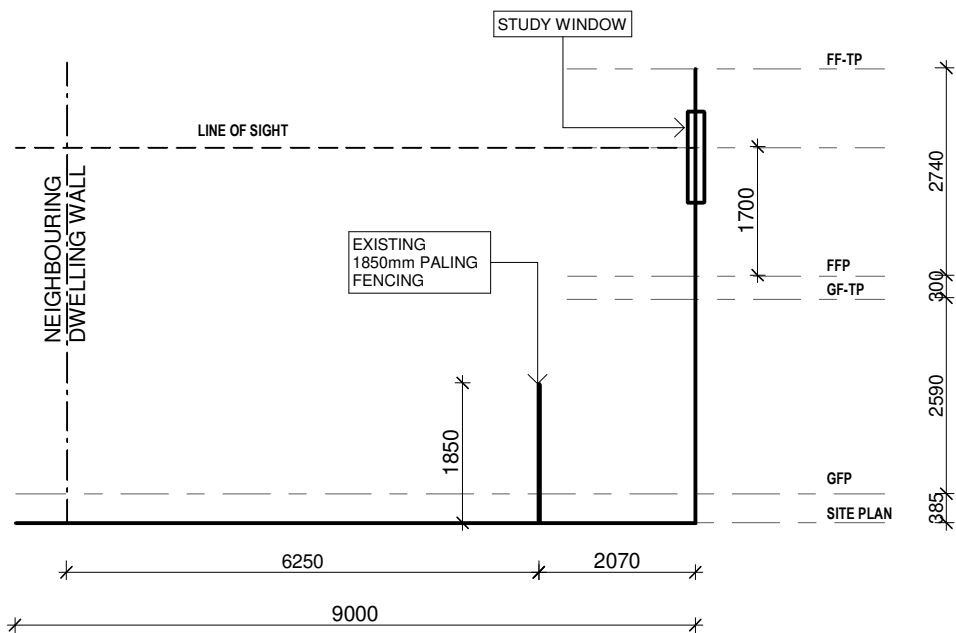

OVERLOOKING DIAGRAM 1
SCALE 1 : 100

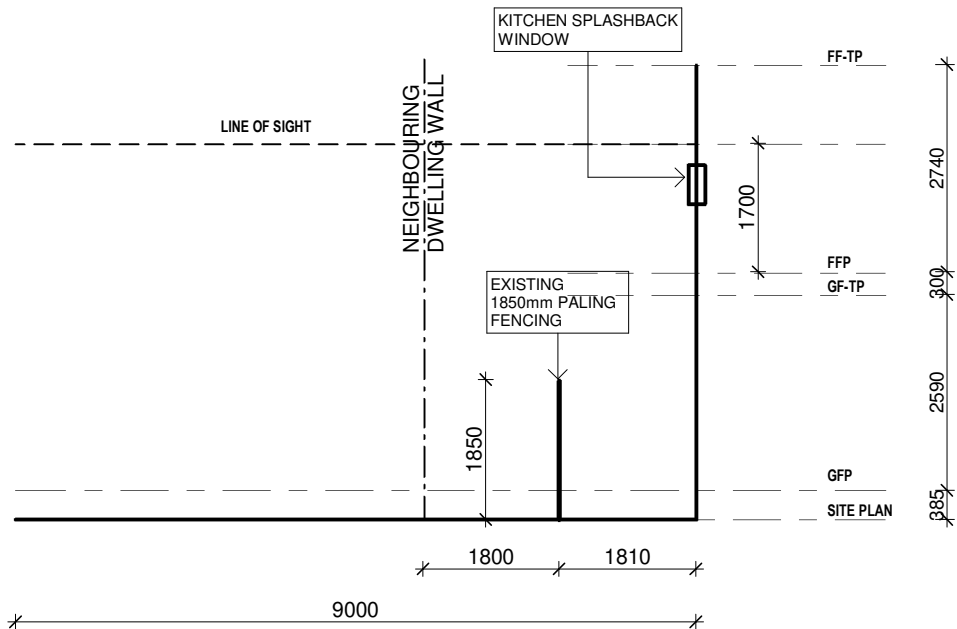

OVERLOOKING DIAGRAM 2
SCALE 1 : 100

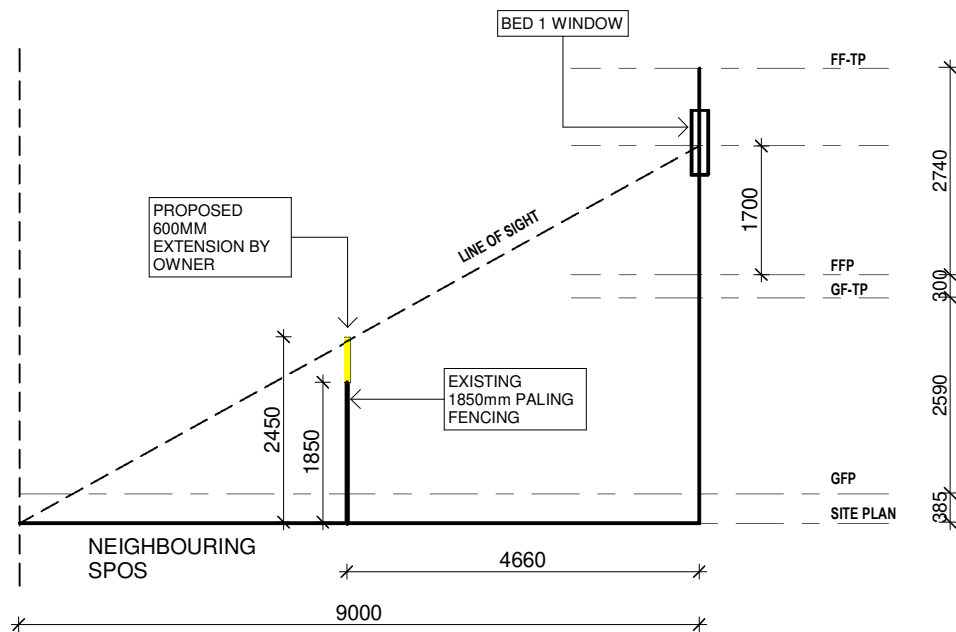

OVERLOOKING DIAGRAM 3
SCALE 1 : 100



Long Island Homes Pty. Ltd.
PO BOX 6269
Point Cook, Vic 3030
p. 61 3 9369 6486 (1800 604 011)
f. 61 3 9369 0994
email: admin@longislandhomes.com.au
www.longislandhomes.com.au

© Copyright
THIS DESIGN & DRAWING SHALL REMAIN THE INTELLECTUAL PROPERTY OF
LONG ISLAND HOMES PTY. LTD. AND SHALL NOT BE COPIED IN WHOLE OR
PART WITHOUT WRITTEN CONSENT FROM LONG ISLAND HOMES PTY LTD.
DB NUMBER

GENERAL NOTES:

- THE CONTRACTOR IS RESPONSIBLE FOR SETTING OUT AND CHECKING ALL LEVELS AND DIMENSIONS ON SITE PRIOR TO COMMENCING ANY SITE WORKS.
- FIGURED DIMENSIONS ARE TO TAKE PREFERENCE OVER SCALE
- DIMENSIONS TO STRUCTURAL TIMBERS & FACE OF BRICKS EXCLUDING BATTENS, PLASTERBOARD ETC.
- ALL DIMENSIONS ON PLAN ARE NOMINAL & MAY VARY TO ACTUAL SIZE
- PROVIDE LOCKS TO ALL OPENABLE WINDOWS & EXTERNAL SLIDING DOORS (KEYED ALIKE).
- MAN HOLE LOCATION MAY BE CHANGED DUE TO TRUSS LAYOUT.
- WINDOW AND DOOR FRAME SIZES ARE NOMINAL AND MAY VARY WITH LONG ISLAND HOMES APPROVED SUPPLIERS.

CLIENT

I / WE.....

CONFIRM THESE DRAWINGS ACCORD WITH OUR REQUIREMENTS AND AUTHORISE THEIR USE FOR NEXT STAGE PURPOSES.

SIGNED..... DATE.....

SIGNED..... DATE.....

SHEET CONTENT:

OVERLOOKING DIAGRAMS

HOUSE TYPE:

SANYA 380

MIN LOT WIDTH:

12M

PROPERTY ADDRESS:

2251 SKODA CIRCUIT
POINTCOOK

CLIENT:

CLARE FRANSIS & CHRISTPHER
KEVIN GRIFFITHS

NORTH:

FACADE:

SCALE: 1 : 100

DATE:

SHEET NUMBER:


10.2

JOB NUMBER:

JOB ISSUE:

H

ISSUE	DATE	REVISION DESCRIPTION	INITIALS
C	04.08.21	R & C ADD AREA	CM
D	20.09.21	COLOUR, PRE CONTRACT CLARIFICATION 06/09/21	CM
E	27.09.21	ENERGY UPGRADES (OPT 2) & CLARIFICATION 27.09.21	CM
F	27.09.21	WIR DOOR	CM
G	29.09.21	ADDED ENGINEERING	CM
H	27.10.21	CONTRACT QUOTE COMMENTS	CM

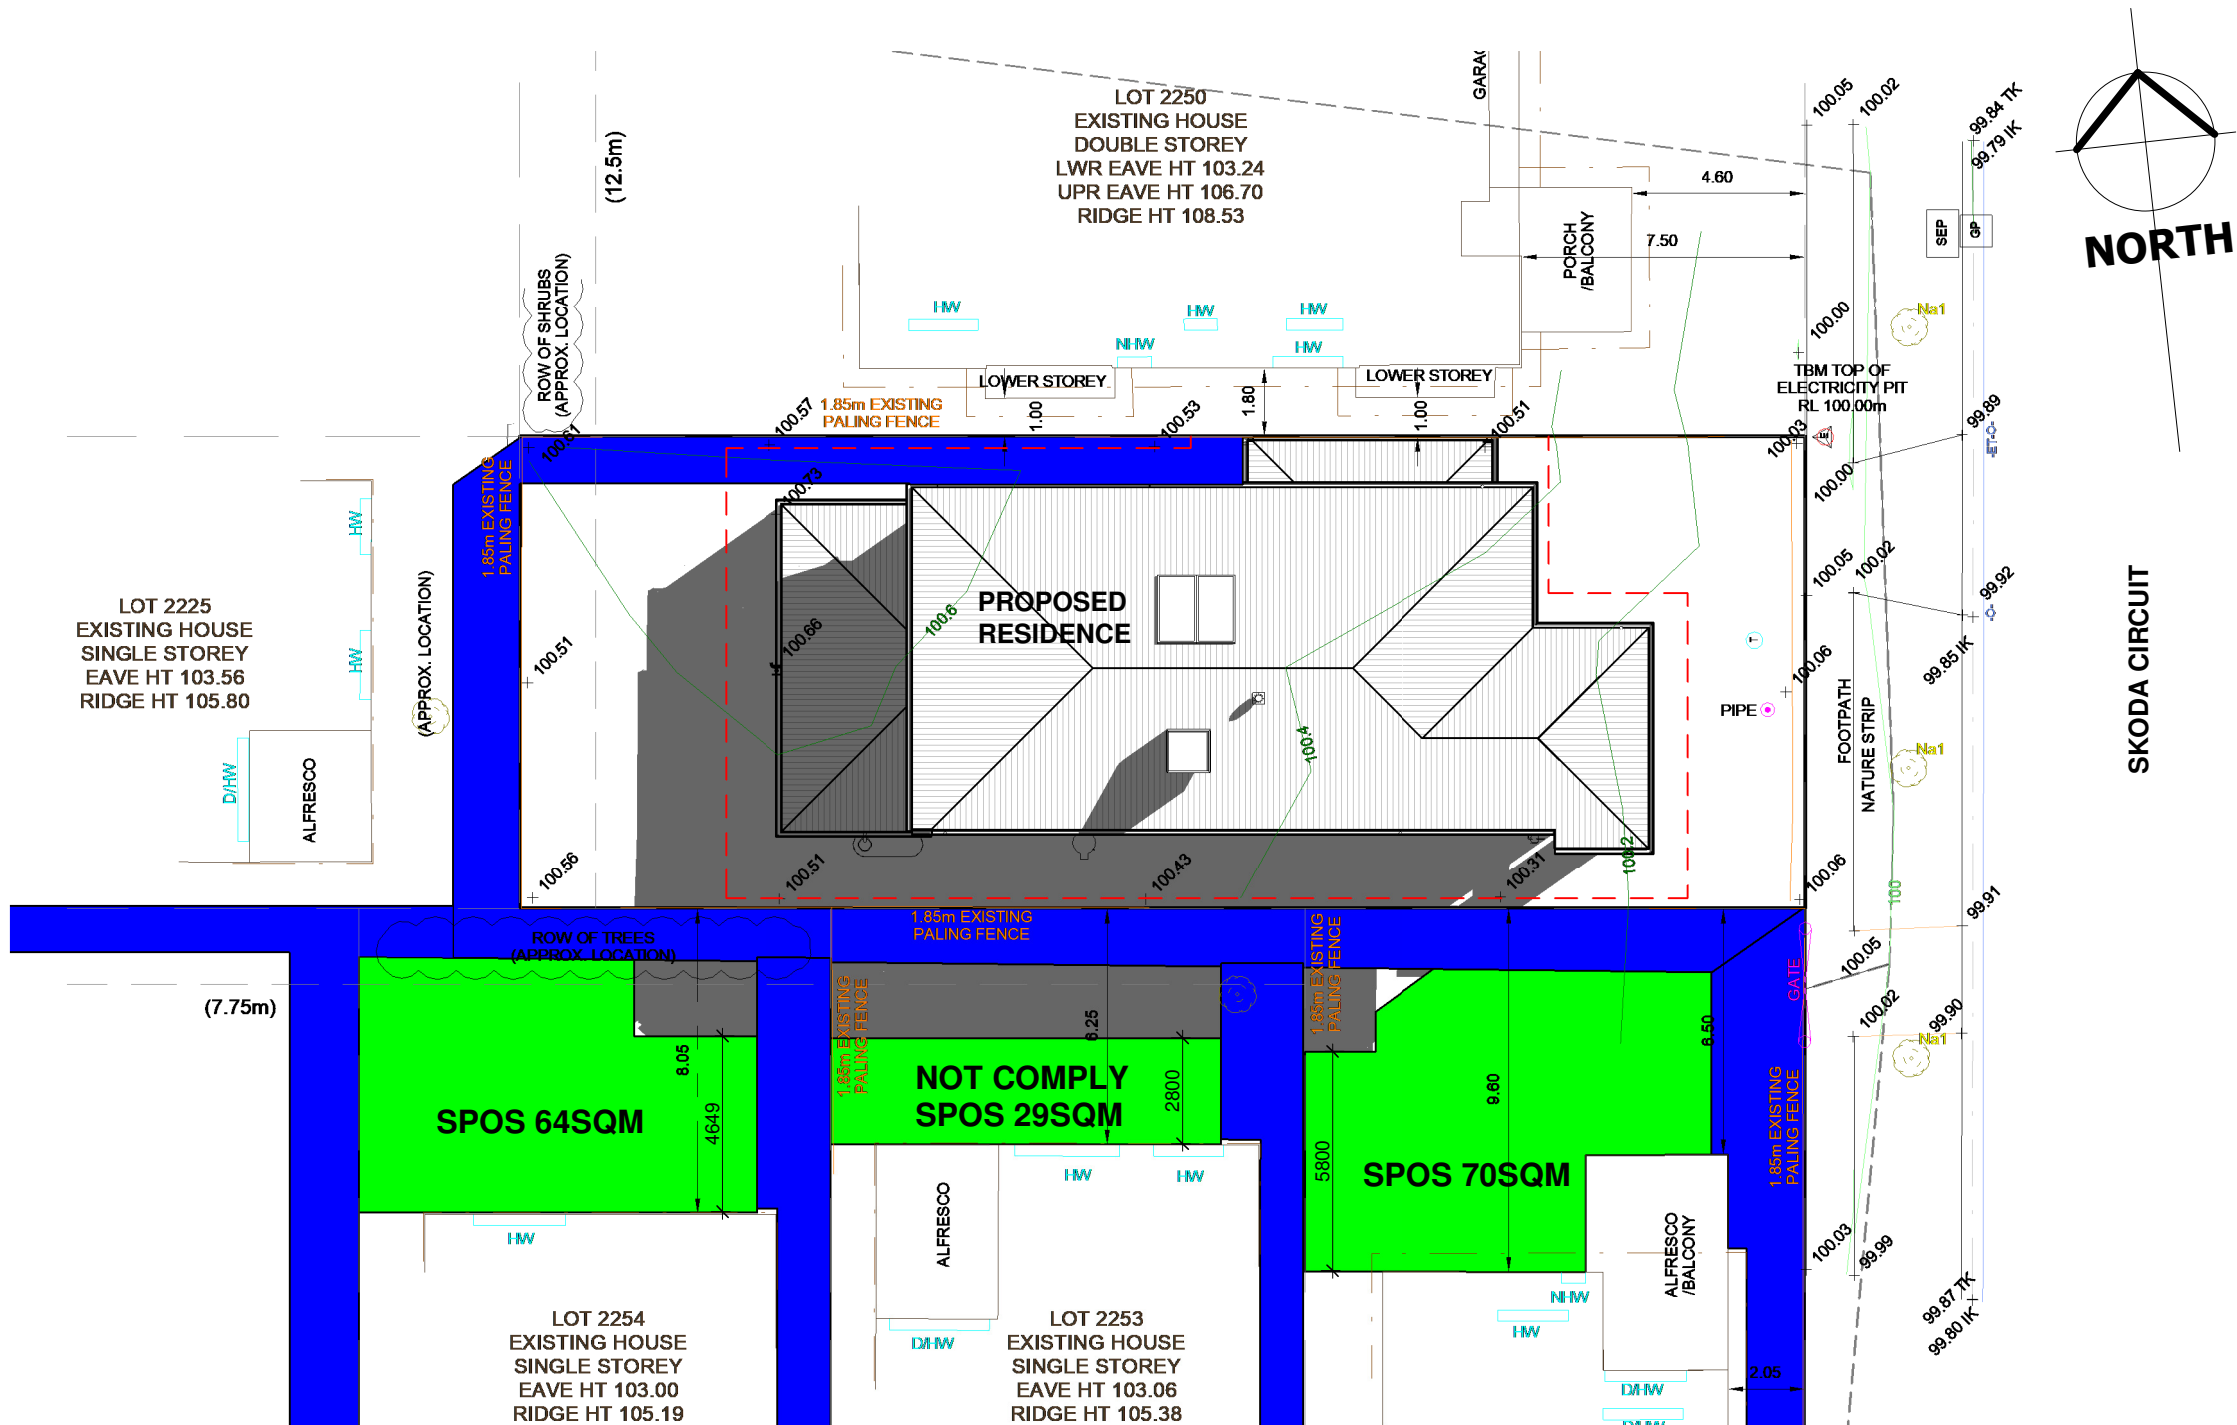

ISLANDER

Long Island Homes Pty. Ltd.
PO BOX 6269
Point Cook, Vic 3030
p. 61 3 9369 6486 (1800 604 011)
f. 61 3 9369 0994
email: admin@longislandhomes.com.au
www.longislandhomes.com.au


© Copyright
THIS DESIGN & DRAWING SHALL REMAIN THE INTELLECTUAL PROPERTY OF
LONG ISLAND HOMES PTY. LTD. AND SHALL NOT BE COPIED IN WHOLE OR
PART WITHOUT WRITTEN CONSENT FROM LONG ISLAND HOMES PTY LTD.
DB NUMBER

GENERAL NOTES:
- THE CONTRACTOR IS RESPONSIBLE FOR SETTING OUT AND CHECKING ALL LEVELS AND DIMENSIONS ON SITE PRIOR TO COMMENCING ANY SITE WORKS.
- FIGURED DIMENSIONS ARE TO TAKE PREFERENCE OVER SCALE
- DIMENSIONS TO STRUCTURAL TIMBERS & FACE OF BRICKS EXCLUDING BATTENS, PLASTERBOARD ETC.
- ALL DIMENSIONS ON PLAN ARE NOMINAL & MAY VARY TO ACTUAL SIZE
- PROVIDE LOCKS TO ALL OPENABLE WINDOWS & EXTERNAL SLIDING DOORS (KEYED ALIKE).
- MAN HOLE LOCATION MAY BE CHANGED DUE TO TRUSS LAYOUT.
- WINDOW AND DOOR FRAME SIZES ARE NOMINAL AND MAY VARY WITH LONG ISLAND HOMES APPROVED SUPPLIERS.

CLIENT
I / WE.....
CONFIRM THESE DRAWINGS ACCORD WITH OUR REQUIREMENTS AND AUTHORISE THEIR USE FOR NEXT STAGE PURPOSES.
SIGNED..... DATE.....
SIGNED..... DATE.....

SHEET CONTENT:
SHADOW DIAGRAM - 9AM
HOUSE TYPE:
SANYA 380
MIN LOT WIDTH:
12M
PROPERTY ADDRESS:
2251 SKODA CIRCUIT
POINTCOOK
CLIENT:
CLARE FRANSIS & CHRISTPHER
KEVIN GRIFFITHS

NORTH:		FACADE:		SHEET NUMBER: 11.1	JOB NUMBER:
		SCALE: 1 : 200			JOB ISSUE: H
		DATE:			
REVISIONS	ISSUE	DATE	REVISION DESCRIPTION		INITIALS
	B	29.07.21	R & C		CM
	C	04.08.21	R & C ADD AREA		CM
	D	20.09.21	COLOUR, PRE CONTRACT CLARIFICATION 06/09/21		CM
	E	27.09.21	ENERGY UPGRADES (OPT 2) & CLARIFICATION 27.09.21		CM
	F	27.09.21	WIR DOOR		CM
	G	29.09.21	ADDED ENGINEERING		CM
	H	27.10.21	CONTRACT QUOTE COMMENTS		CM

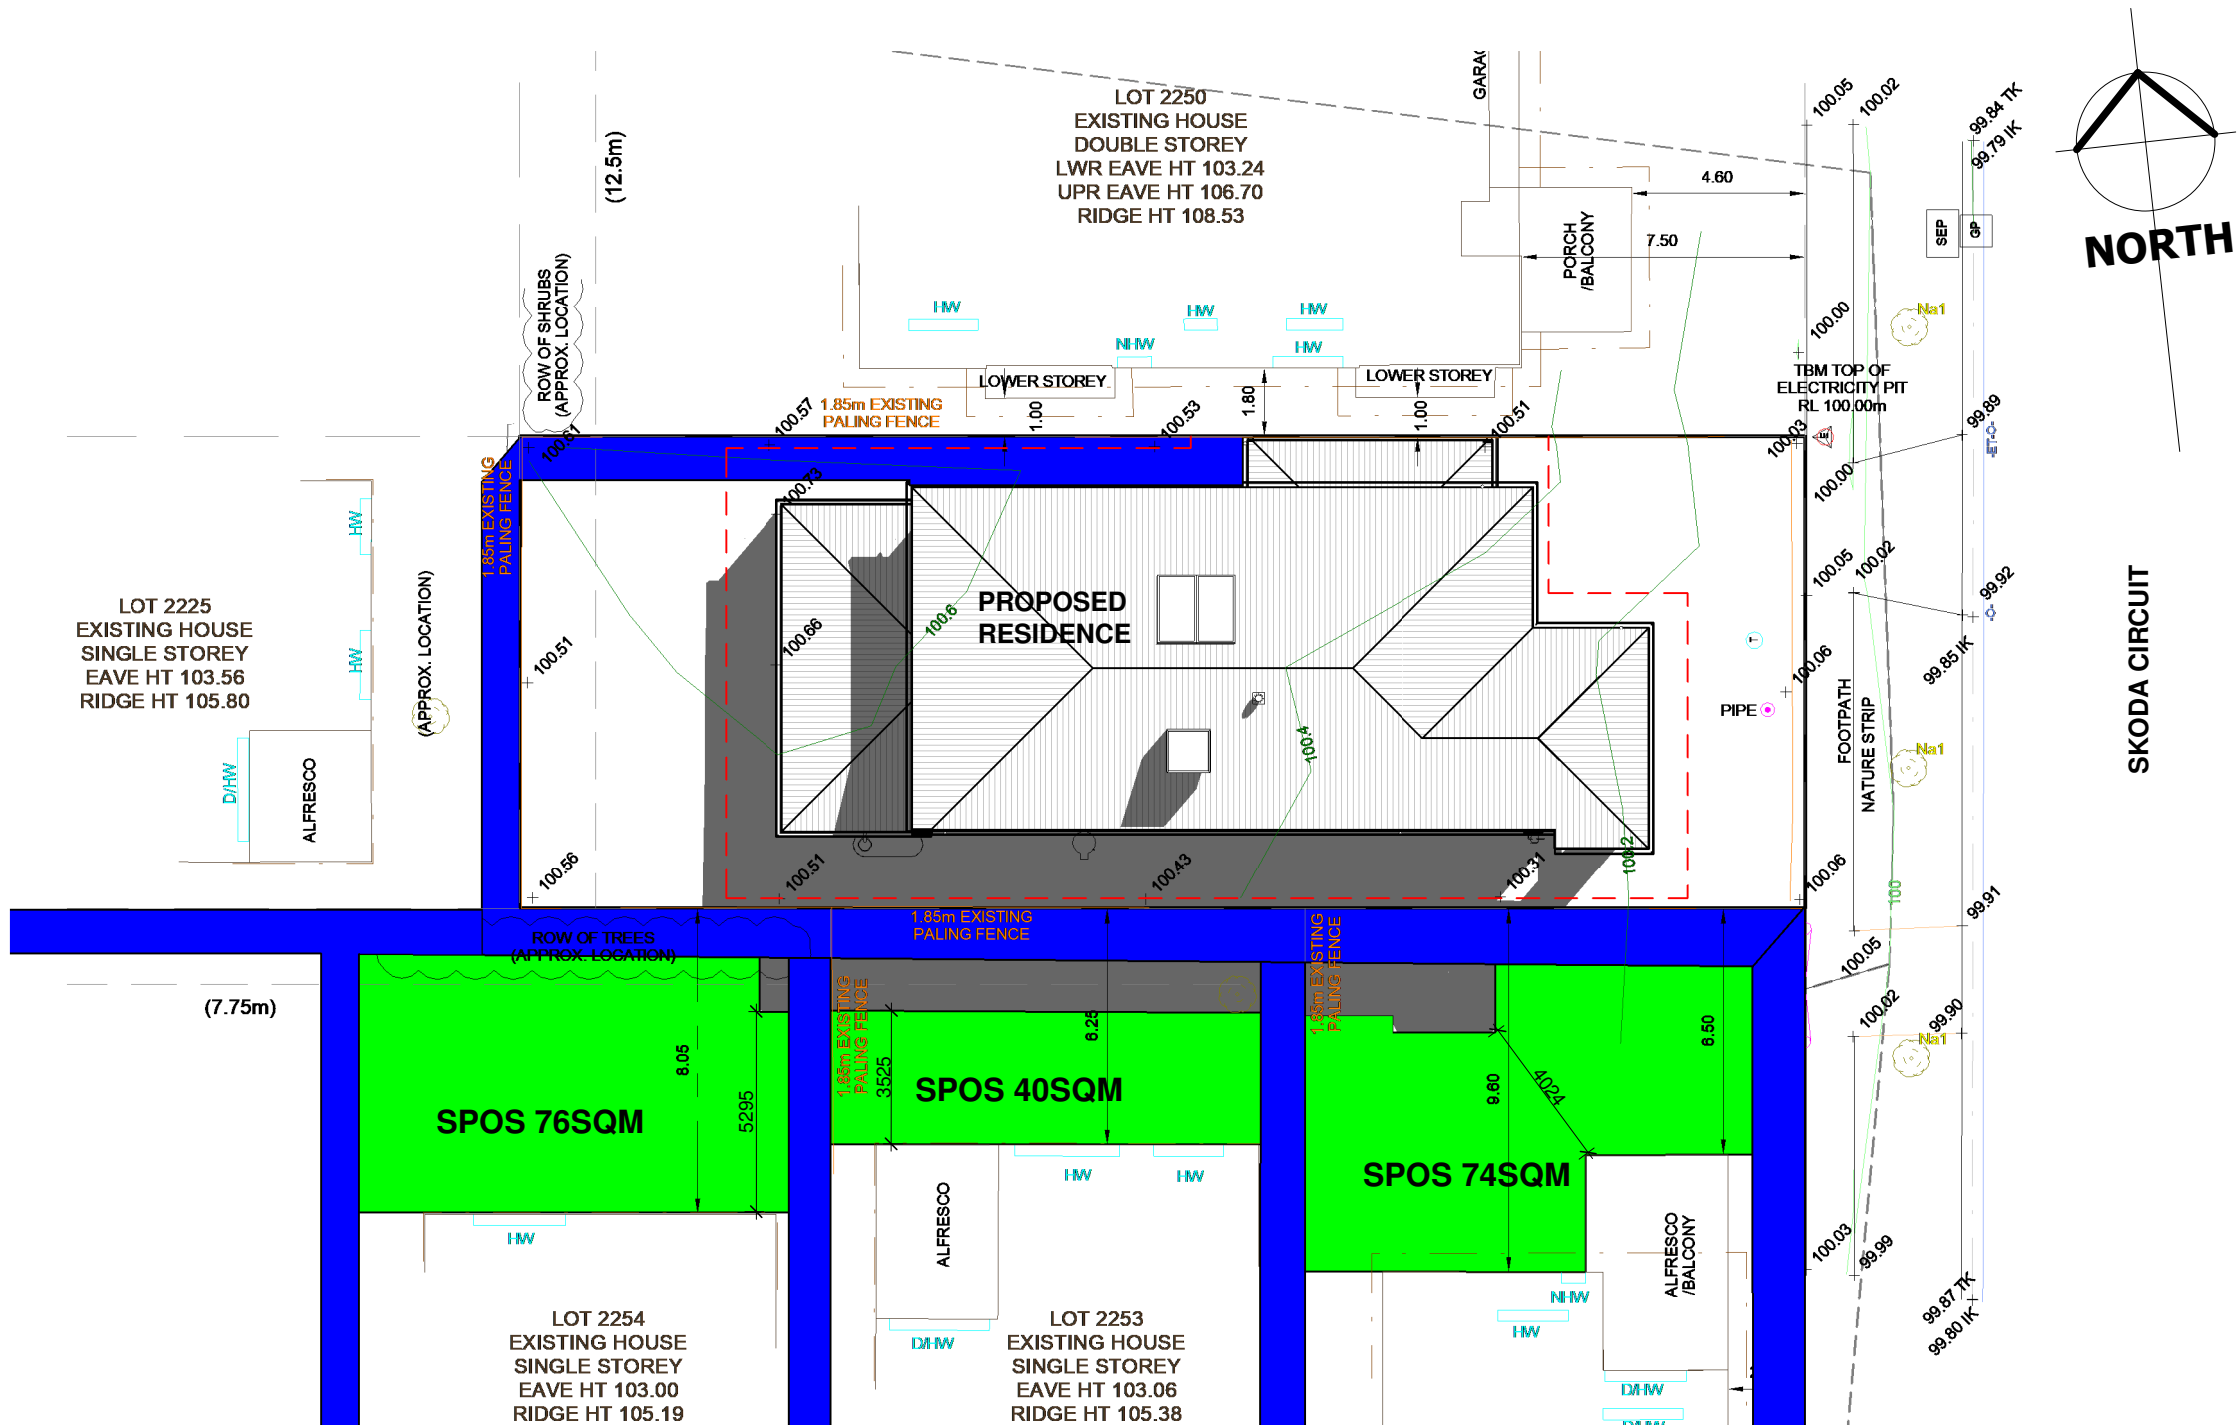

Long Island Homes Pty. Ltd.
PO BOX 6269
Point Cook, Vic 3030
p. 61 3 9369 6486 (1800 604 011)
f. 61 3 9369 0994
email: admin@longislandhomes.com.au
www.longislandhomes.com.au

© Copyright
THIS DESIGN & DRAWING SHALL REMAIN THE INTELLECTUAL PROPERTY OF
LONG ISLAND HOMES PTY. LTD. AND SHALL NOT BE COPIED IN WHOLE OR
PART WITHOUT WRITTEN CONSENT FROM LONG ISLAND HOMES PTY LTD.
DB NUMBER

GENERAL NOTES:

- THE CONTRACTOR IS RESPONSIBLE FOR SETTING OUT AND CHECKING ALL LEVELS AND DIMENSIONS ON SITE PRIOR TO COMMENCING ANY SITE WORKS.
- FIGURED DIMENSIONS ARE TO TAKE PREFERENCE OVER SCALE
- DIMENSIONS TO STRUCTURAL TIMBERS & FACE OF BRICKS EXCLUDING BATTENS, PLASTERBOARD ETC.
- ALL DIMENSIONS ON PLAN ARE NOMINAL & MAY VARY TO ACTUAL SIZE
- PROVIDE LOCKS TO ALL OPENABLE WINDOWS & EXTERNAL SLIDING DOORS (KEYED ALIKE).
- MAN HOLE LOCATION MAY BE CHANGED DUE TO TRUSS LAYOUT.
- WINDOW AND DOOR FRAME SIZES ARE NOMINAL AND MAY VARY WITH LONG ISLAND HOMES APPROVED SUPPLIERS.

CLIENT

I / WE.....

CONFIRM THESE DRAWINGS ACCORD WITH OUR REQUIREMENTS AND AUTHORISE THEIR USE FOR NEXT STAGE PURPOSES.

SIGNED..... DATE.....

SIGNED..... DATE.....

SIGN OFF

SHEET CONTENT:

SHADOW DIAGRAM - 10AM

HOUSE TYPE: SANYA 380 MIN LOT WIDTH: 12M

PROPERTY ADDRESS:
2251 SKODA CIRCUIT
POINTCOOK

CLIENT:

CLARE FRANSIS & CHRISTPHER
KEVIN GRIFFITHS

NORTH:

FACADE:

SCALE: 1 : 200

DATE:

SHEET NUMBER:


11.2

JOB NUMBER:

JOB ISSUE:

H

REVISIONS	ISSUE	DATE	REVISION DESCRIPTION	INITIALS
B	29.07.21	R & C		CM
C	04.08.21	R & C ADD AREA		CM
D	20.09.21	COLOUR, PRE CONTRACT CLARIFICATION 06/09/21		CM
E	27.09.21	ENERGY UPGRADES (OPT 2) & CLARIFICATION 27.09.21		CM
F	27.09.21	WIR DOOR		CM
G	29.09.21	ADDED ENGINEERING		CM
H	27.10.21	CONTRACT QUOTE COMMENTS		CM

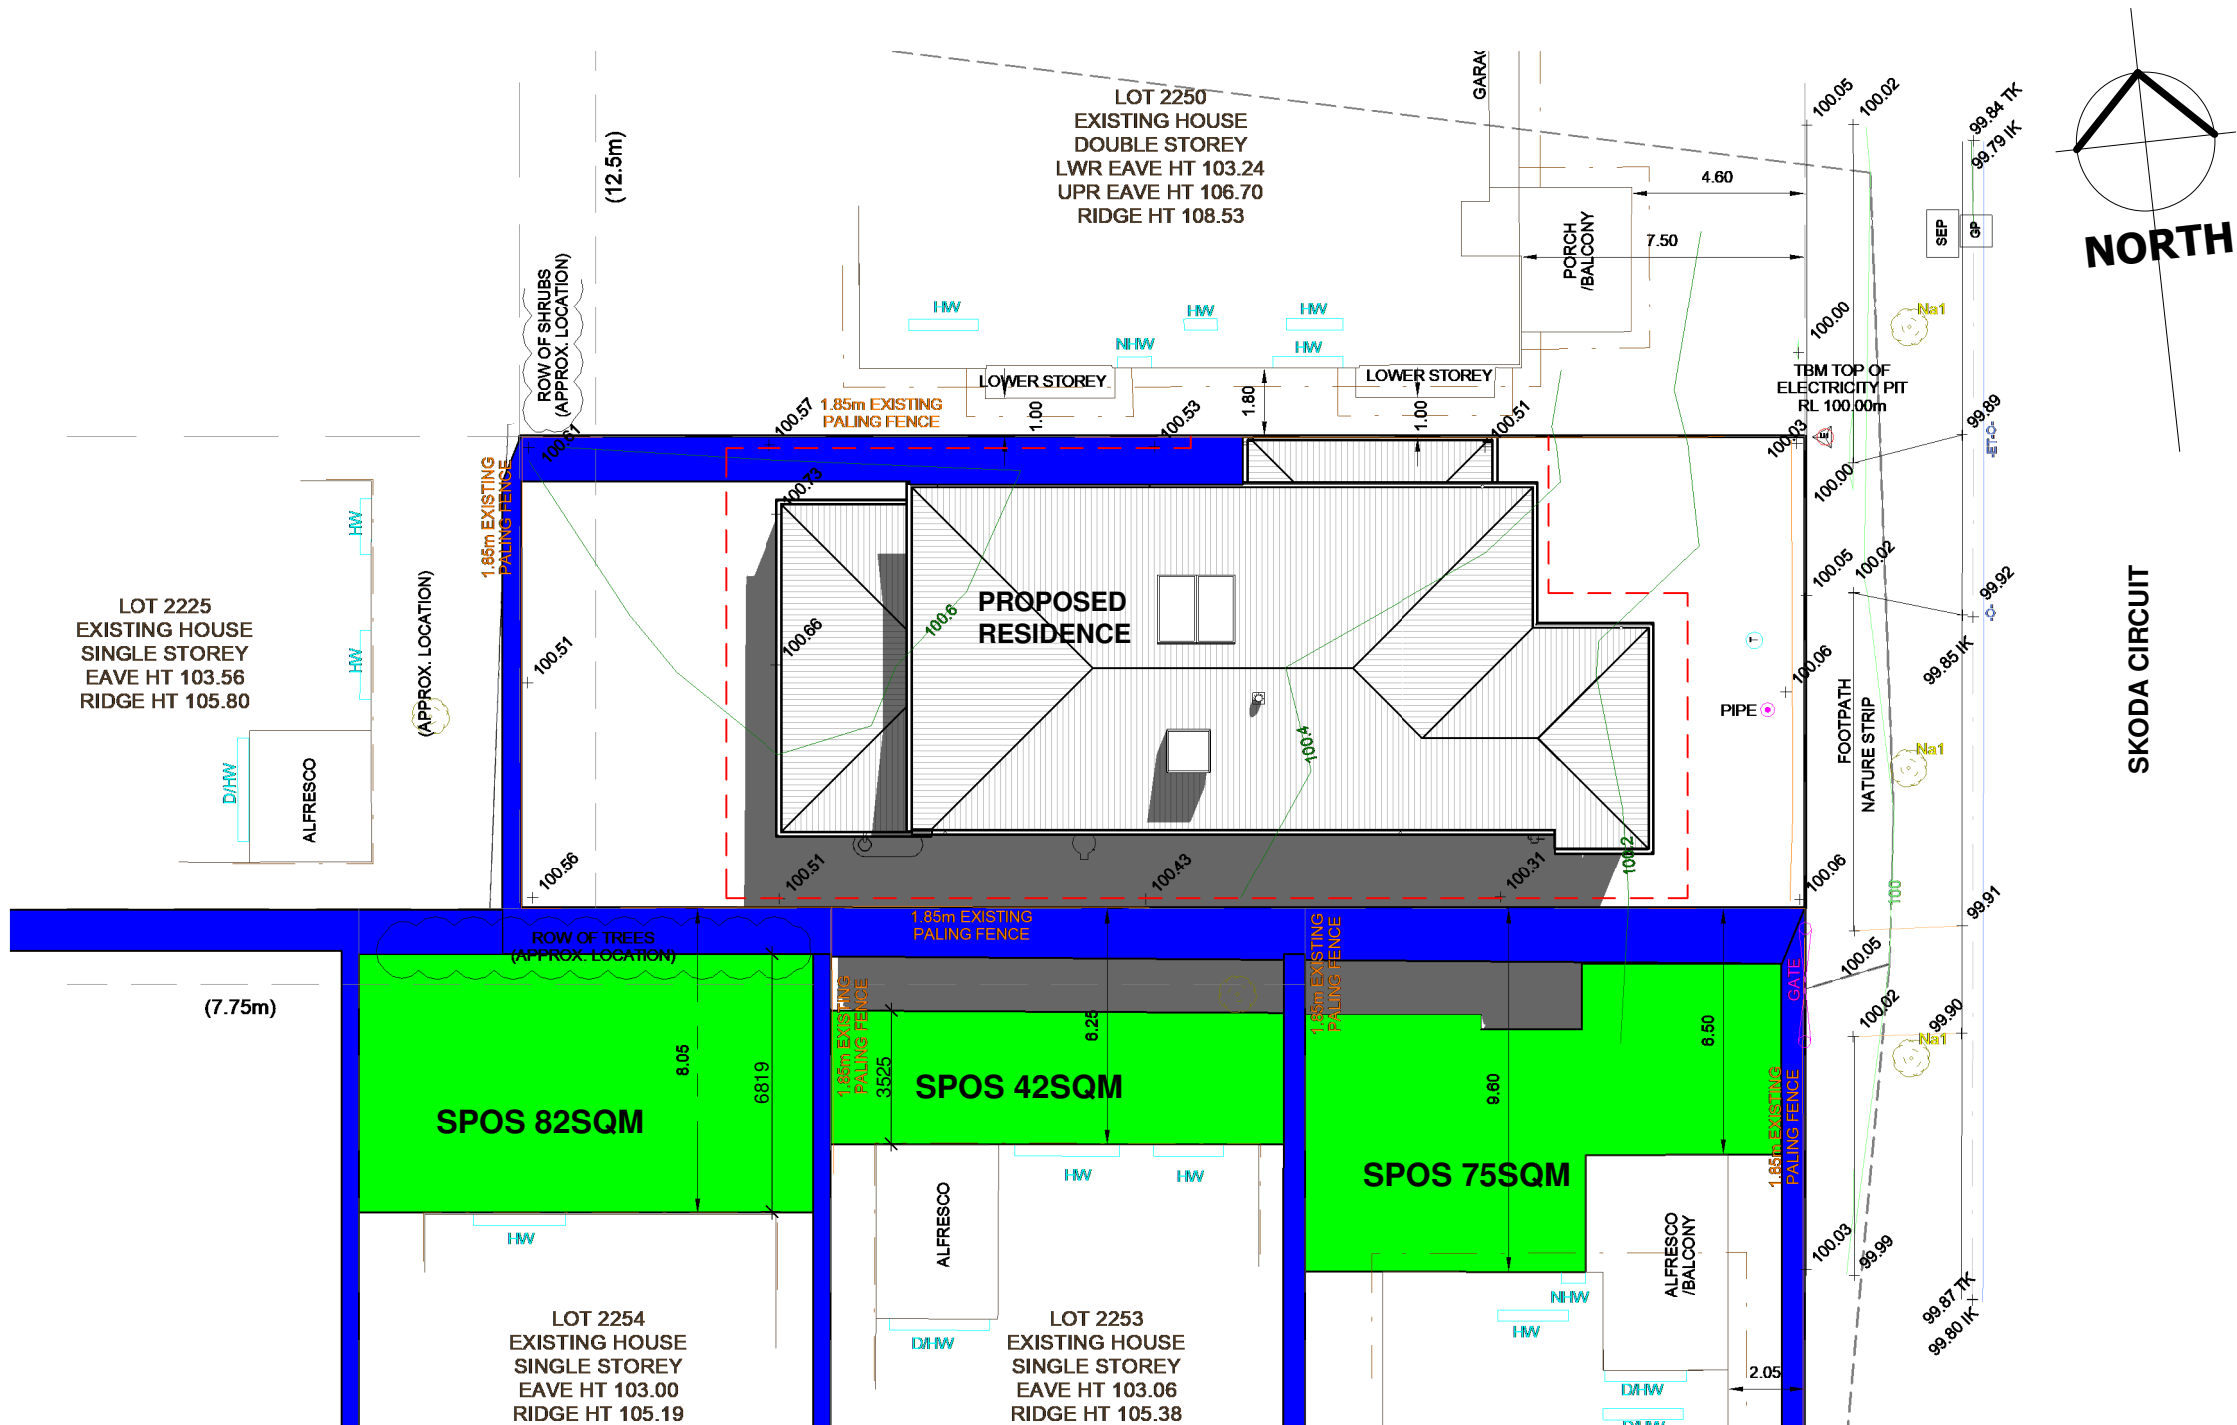

Long Island Homes Pty. Ltd.
PO BOX 6269
Point Cook, Vic 3030
p. 61 3 9369 6486 (1800 604 011)
f. 61 3 9369 0994
email: admin@longislandhomes.com.au
www.longislandhomes.com.au


© Copyright
THIS DESIGN & DRAWING SHALL REMAIN THE INTELLECTUAL PROPERTY OF
LONG ISLAND HOMES PTY. LTD. AND SHALL NOT BE COPIED IN WHOLE OR
PART WITHOUT WRITTEN CONSENT FROM LONG ISLAND HOMES PTY LTD.
DB NUMBER

GENERAL NOTES:
- THE CONTRACTOR IS RESPONSIBLE FOR SETTING OUT AND CHECKING ALL LEVELS AND DIMENSIONS ON SITE PRIOR TO COMMENCING ANY SITE WORKS.
- FIGURED DIMENSIONS ARE TO TAKE PREFERENCE OVER SCALE
- DIMENSIONS TO STRUCTURAL TIMBERS & FACE OF BRICKS EXCLUDING BATTENS, PLASTERBOARD ETC.
- ALL DIMENSIONS ON PLAN ARE NOMINAL & MAY VARY TO ACTUAL SIZE
- PROVIDE LOCKS TO ALL OPENABLE WINDOWS & EXTERNAL SLIDING DOORS (KEYED ALIKE).
- MAN HOLE LOCATION MAY BE CHANGED DUE TO TRUSS LAYOUT.
- WINDOW AND DOOR FRAME SIZES ARE NOMINAL AND MAY VARY WITH LONG ISLAND HOMES APPROVED SUPPLIERS.

CLIENT
I / WE.....
CONFIRM THESE DRAWINGS ACCORD WITH OUR REQUIREMENTS AND AUTHORISE THEIR USE FOR NEXT STAGE PURPOSES.
SIGNED..... DATE.....
SIGNED..... DATE.....

SHEET CONTENT:
SHADOW DIAGRAM - 11AM
HOUSE TYPE: SANYA 380 MIN LOT WIDTH: 12M
PROPERTY ADDRESS: 2251 SKODA CIRCUIT POINTCOOK
CLIENT: CLARE FRANSIS & CHRISTPHER KEVIN GRIFFITHS

NORTH:		FACADE:		SHEET NUMBER: 11.3	JOB NUMBER:
		SCALE: 1 : 200			JOB ISSUE: H
		DATE:			
REVISIONS	ISSUE	DATE	REVISION DESCRIPTION		INITIALS
	B	29.07.21	R & C		CM
	C	04.08.21	R & C ADD AREA		CM
	D	20.09.21	COLOUR, PRE CONTRACT CLARIFICATION 06/09/21		CM
	E	27.09.21	ENERGY UPGRADES (OPT 2) & CLARIFICATION 27.09.21		CM
	F	27.09.21	WIR DOOR		CM
	G	29.09.21	ADDED ENGINEERING		CM
	H	27.10.21	CONTRACT QUOTE COMMENTS		CM

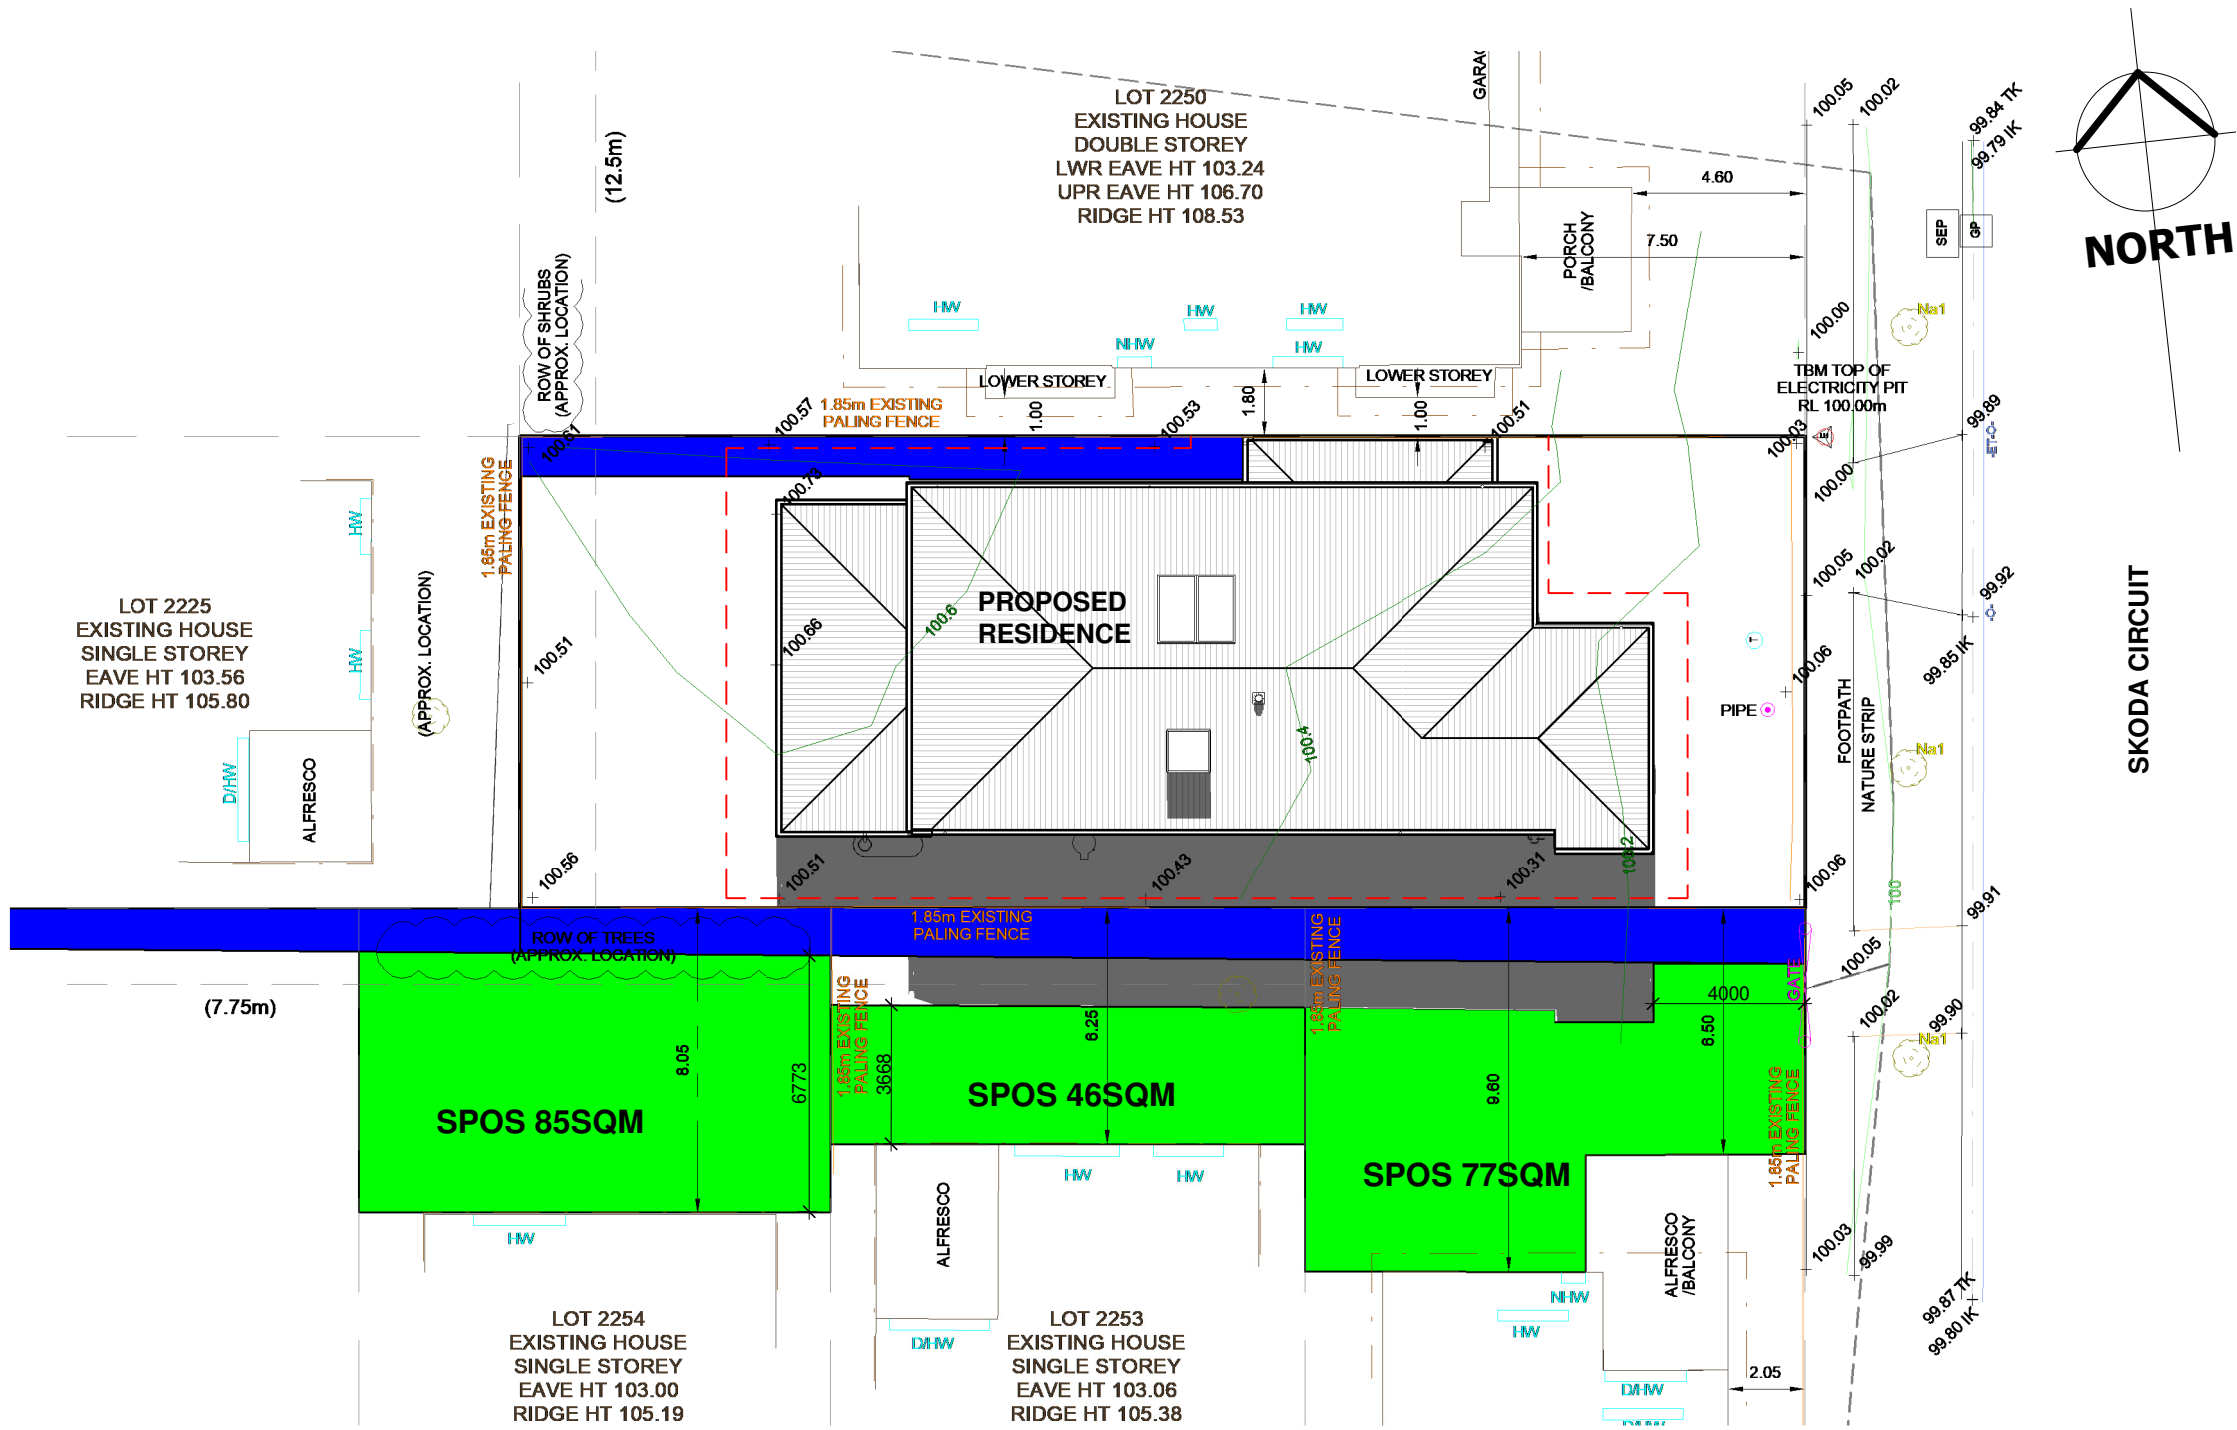

Long Island Homes Pty. Ltd.
PO BOX 6269
Point Cook, Vic 3030
p. 61 3 9369 6486 (1800 604 011)
f. 61 3 9369 0994
email: admin@longislandhomes.com.au
www.longislandhomes.com.au

© Copyright
THIS DESIGN & DRAWING SHALL REMAIN THE INTELLECTUAL PROPERTY OF
LONG ISLAND HOMES PTY. LTD. AND SHALL NOT BE COPIED IN WHOLE OR
PART WITHOUT WRITTEN CONSENT FROM LONG ISLAND HOMES PTY LTD.
DB NUMBER

GENERAL NOTES:

- THE CONTRACTOR IS RESPONSIBLE FOR SETTING OUT AND CHECKING ALL LEVELS AND DIMENSIONS ON SITE PRIOR TO COMMENCING ANY SITE WORKS.
- FIGURED DIMENSIONS ARE TO TAKE PREFERENCE OVER SCALE
- DIMENSIONS TO STRUCTURAL TIMBERS & FACE OF BRICKS EXCLUDING BATTENS, PLASTERBOARD ETC.
- ALL DIMENSIONS ON PLAN ARE NOMINAL & MAY VARY TO ACTUAL SIZE
- PROVIDE LOCKS TO ALL OPENABLE WINDOWS & EXTERNAL SLIDING DOORS (KEYED ALIKE).
- MAN HOLE LOCATION MAY BE CHANGED DUE TO TRUSS LAYOUT.
- WINDOW AND DOOR FRAME SIZES ARE NOMINAL AND MAY VARY WITH LONG ISLAND HOMES APPROVED SUPPLIERS.

CLIENT

I / WE.....

CONFIRM THESE DRAWINGS ACCORD WITH OUR REQUIREMENTS AND AUTHORISE THEIR USE FOR NEXT STAGE PURPOSES.

SIGNED..... DATE.....

SIGNED..... DATE.....

SHEET CONTENT:

SHADOW DIAGRAM - 12PM

HOUSE TYPE:

SANYA 380

MIN LOT WIDTH:

12M

PROPERTY ADDRESS:

2251 SKODA CIRCUIT
POINTCOOK

CLIENT:

CLARE FRANSIS & CHRISTPHER
KEVIN GRIFFITHS

NORTH:

FACADE:

SCALE: 1 : 200

DATE:

SHEET NUMBER:


11.4

JOB NUMBER:

JOB ISSUE:

H

REVISIONS	ISSUE	DATE	REVISION DESCRIPTION	INITIALS
B	29.07.21		R & C	CM
C	04.08.21		R & C ADD AREA	CM
D	20.09.21		COLOUR, PRE CONTRACT CLARIFICATION 06/09/21	CM
E	27.09.21		ENERGY UPGRADES (OPT 2) & CLARIFICATION 27.09.21	CM
F	27.09.21		WIR DOOR	CM
G	29.09.21		ADDED ENGINEERING	CM
H	27.10.21		CONTRACT QUOTE COMMENTS	CM

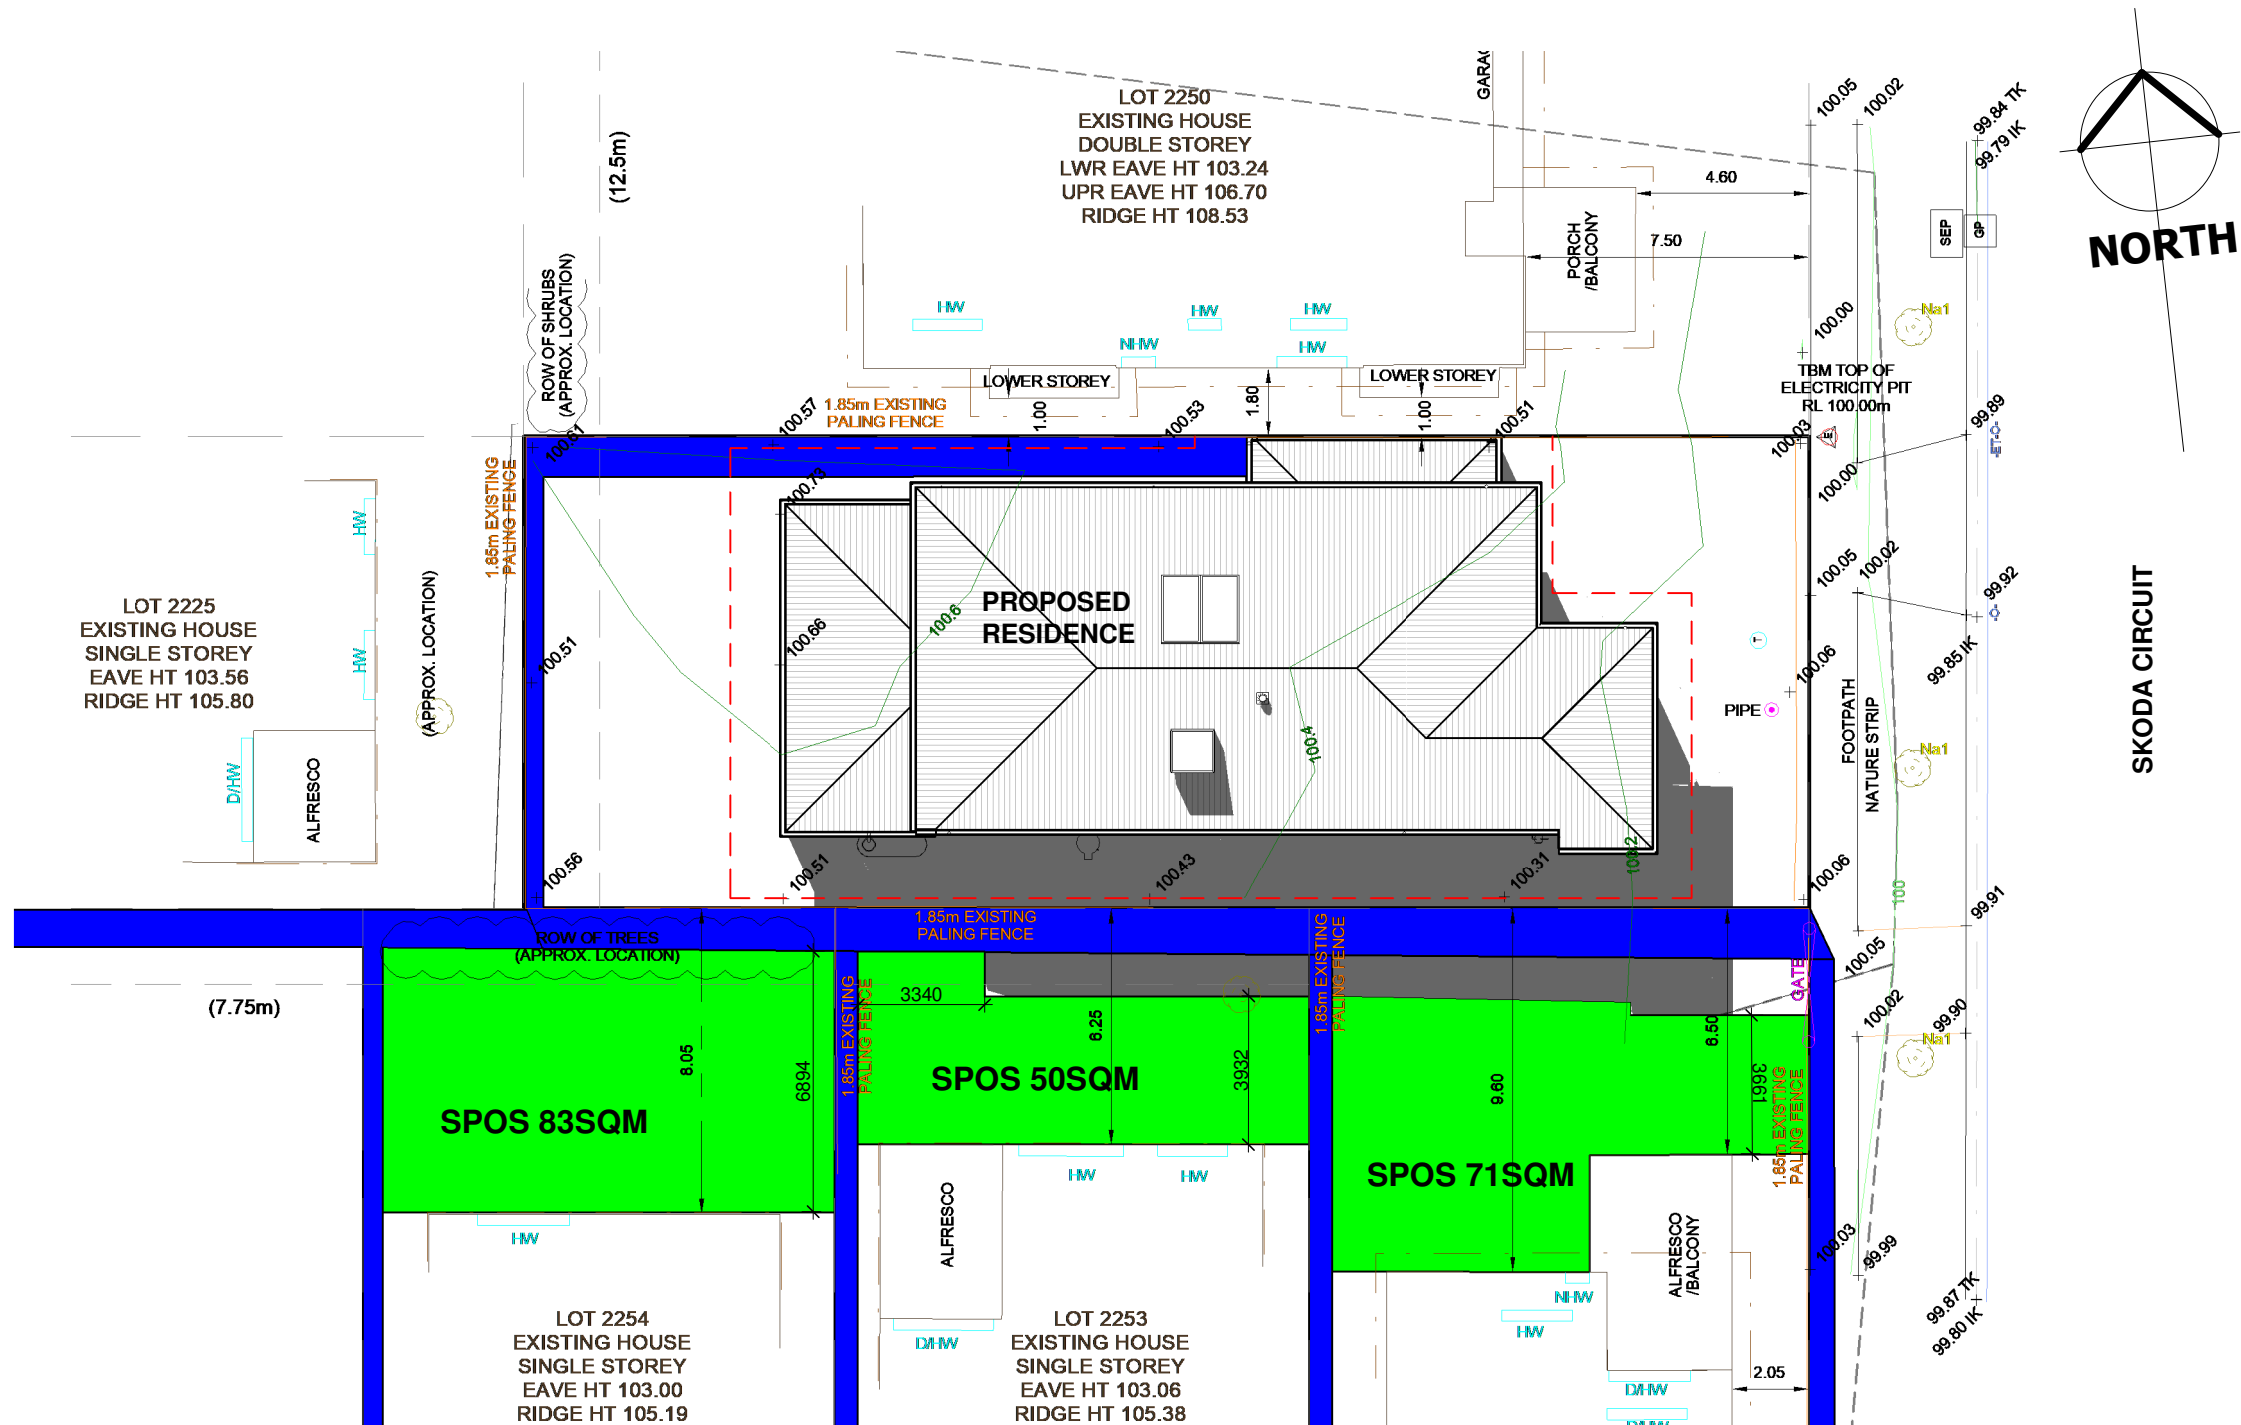

Long Island Homes Pty. Ltd.
PO BOX 6269
Point Cook, Vic 3030
p. 61 3 9369 6486 (1800 604 011)
f. 61 3 9369 0994
email: admin@longislandhomes.com.au
www.longislandhomes.com.au


© Copyright
THIS DESIGN & DRAWING SHALL REMAIN THE INTELLECTUAL PROPERTY OF
LONG ISLAND HOMES PTY. LTD. AND SHALL NOT BE COPIED IN WHOLE OR
PART WITHOUT WRITTEN CONSENT FROM LONG ISLAND HOMES PTY LTD.
DB NUMBER

GENERAL NOTES:
- THE CONTRACTOR IS RESPONSIBLE FOR SETTING OUT AND CHECKING ALL LEVELS AND DIMENSIONS ON SITE PRIOR TO COMMENCING ANY SITE WORKS.
- FIGURED DIMENSIONS ARE TO TAKE PREFERENCE OVER SCALE
- DIMENSIONS TO STRUCTURAL TIMBERS & FACE OF BRICKS EXCLUDING BATTENS, PLASTERBOARD ETC.
- ALL DIMENSIONS ON PLAN ARE NOMINAL & MAY VARY TO ACTUAL SIZE
- PROVIDE LOCKS TO ALL OPENABLE WINDOWS & EXTERNAL SLIDING DOORS (KEYED ALIKE).
- MAN HOLE LOCATION MAY BE CHANGED DUE TO TRUSS LAYOUT.
- WINDOW AND DOOR FRAME SIZES ARE NOMINAL AND MAY VARY WITH LONG ISLAND HOMES APPROVED SUPPLIERS.

CLIENT
I / WE.....
CONFIRM THESE DRAWINGS ACCORD WITH OUR REQUIREMENTS AND AUTHORISE THEIR USE FOR NEXT STAGE PURPOSES.
SIGNED..... DATE.....
SIGNED..... DATE.....

SHEET CONTENT:
SHADOW DIAGRAM - 1PM
HOUSE TYPE:
SANYA 380
MIN LOT WIDTH:
12M
PROPERTY ADDRESS:
2251 SKODA CIRCUIT
POINTCOOK
CLIENT:
CLARE FRANSIS & CHRISTPHER
KEVIN GRIFFITHS

NORTH:		FACADE:		SHEET NUMBER: 11.5	JOB NUMBER:
		SCALE: 1 : 200			
		DATE:			JOB ISSUE: H
REVISIONS	ISSUE	DATE	REVISION DESCRIPTION		INITIALS
	B	29.07.21	R & C		CM
	C	04.08.21	R & C ADD AREA		CM
	D	20.09.21	COLOUR, PRE CONTRACT CLARIFICATION 06/09/21		CM
	E	27.09.21	ENERGY UPGRADES (OPT 2) & CLARIFICATION 27.09.21		CM
	F	27.09.21	WIR DOOR		CM
	G	29.09.21	ADDED ENGINEERING		CM
	H	27.10.21	CONTRACT QUOTE COMMENTS		CM

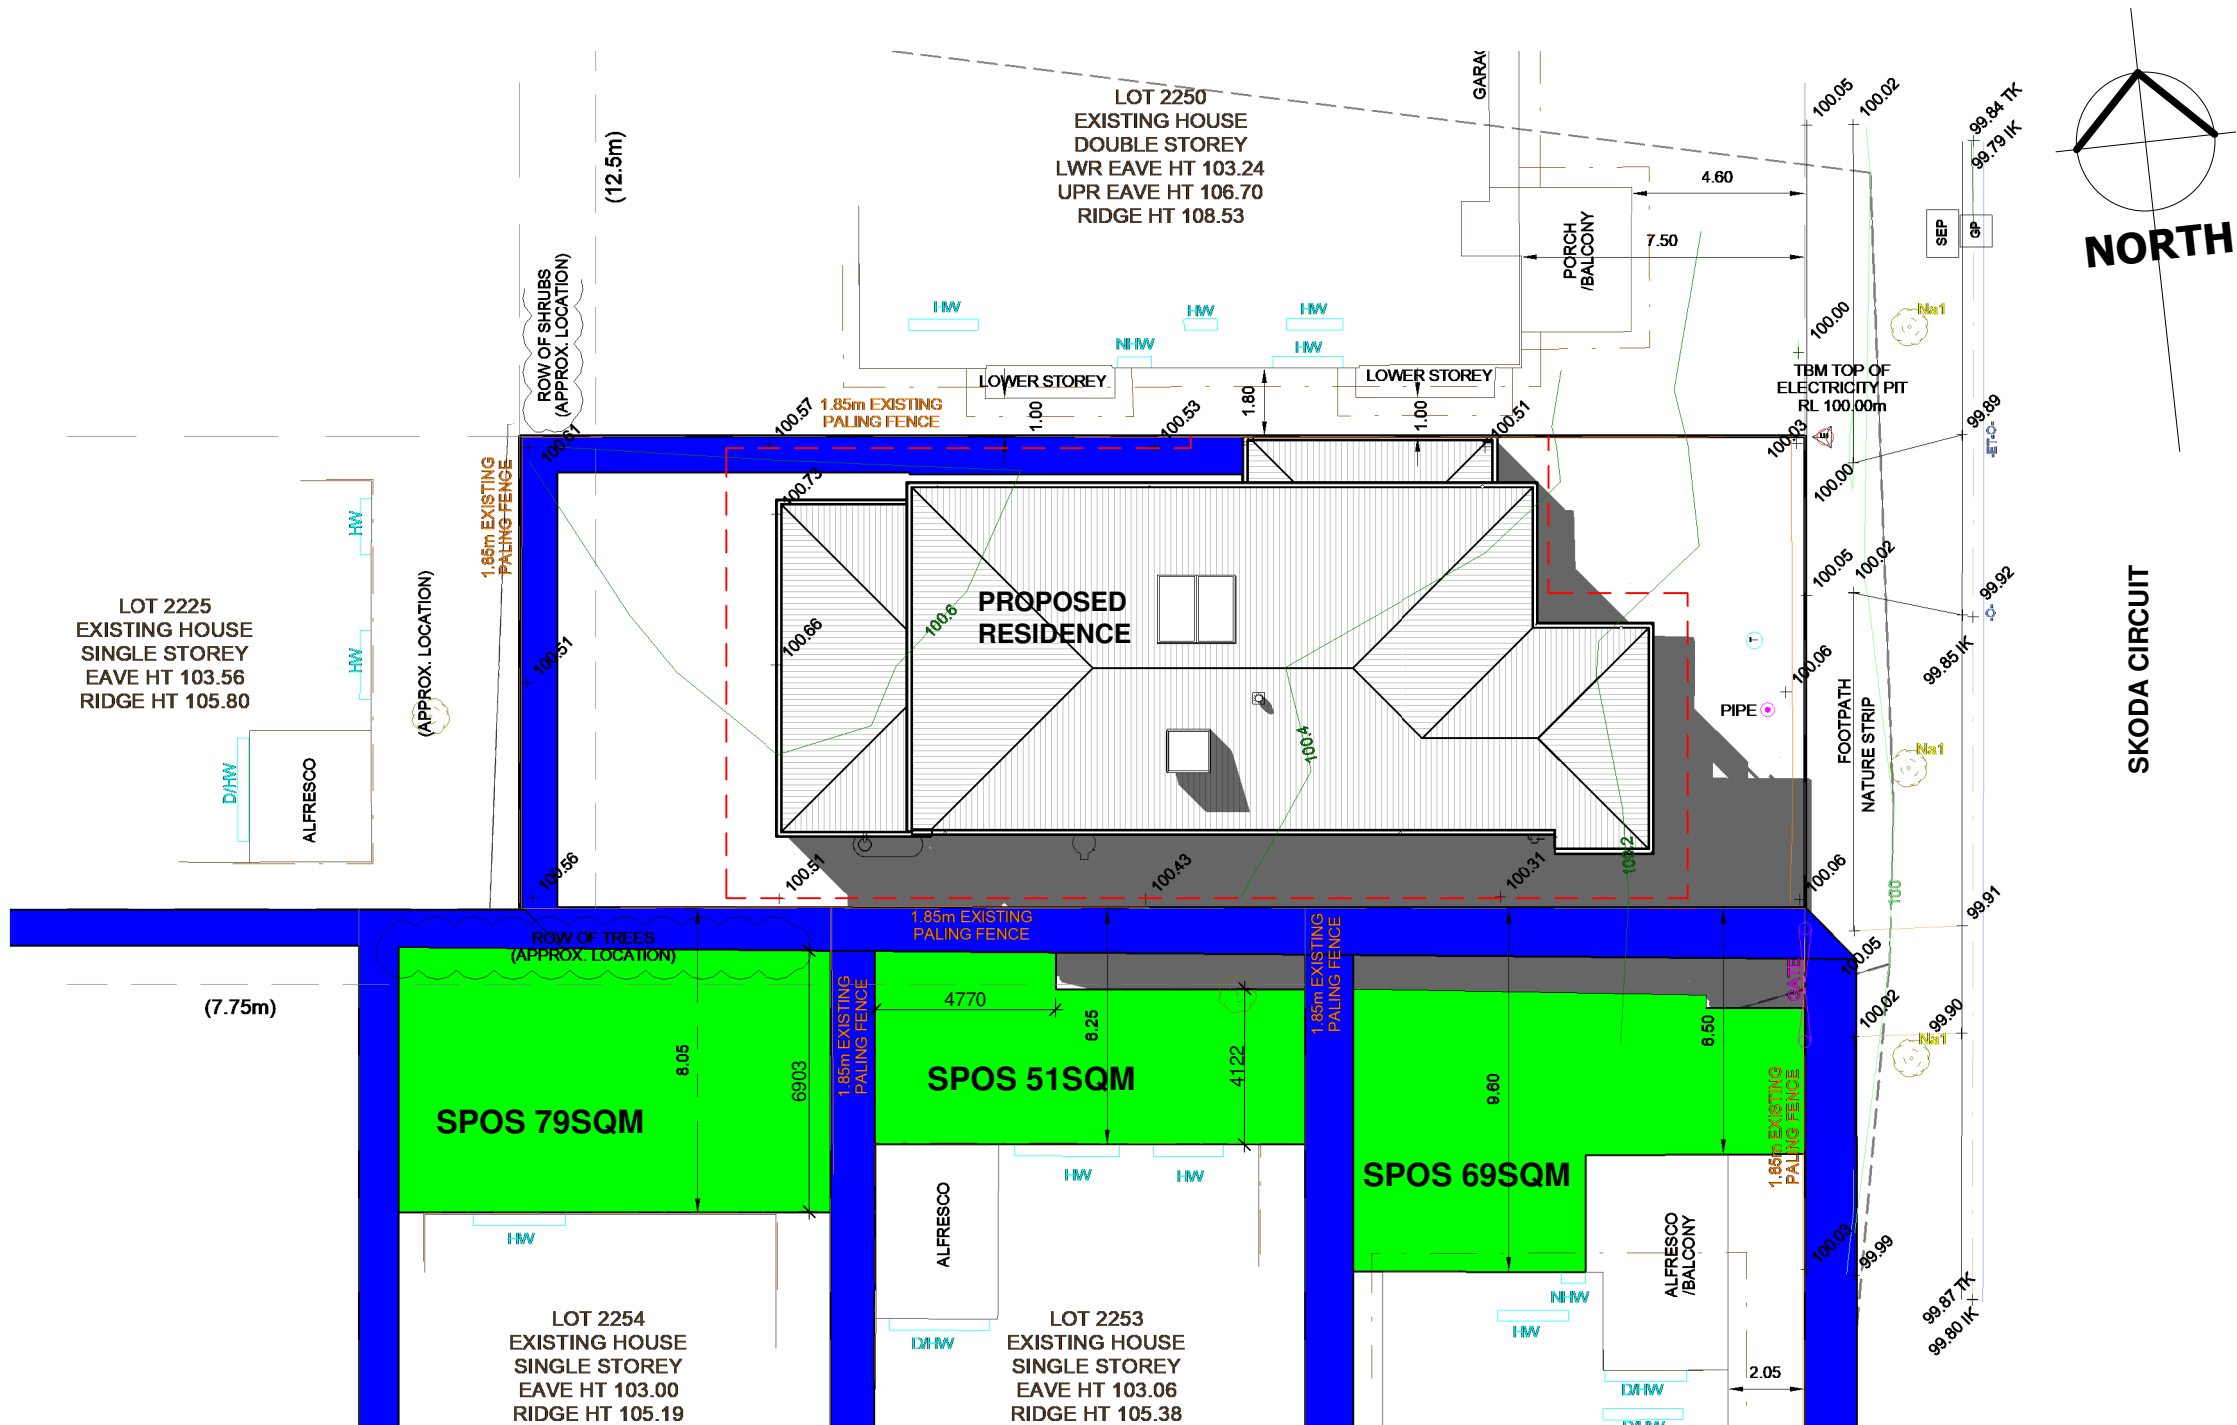

Long Island Homes Pty. Ltd.
PO BOX 6269
Point Cook, Vic 3030
p. 61 3 9369 6486 (1800 604 011)
f. 61 3 9369 0994
email: admin@longislandhomes.com.au
www.longislandhomes.com.au


© Copyright
THIS DESIGN & DRAWING SHALL REMAIN THE INTELLECTUAL PROPERTY OF
LONG ISLAND HOMES PTY. LTD. AND SHALL NOT BE COPIED IN WHOLE OR
PART WITHOUT WRITTEN CONSENT FROM LONG ISLAND HOMES PTY LTD.
DB NUMBER

GENERAL NOTES:
- THE CONTRACTOR IS RESPONSIBLE FOR SETTING OUT AND CHECKING ALL LEVELS AND DIMENSIONS ON SITE PRIOR TO COMMENCING ANY SITE WORKS.
- FIGURED DIMENSIONS ARE TO TAKE PREFERENCE OVER SCALE
- DIMENSIONS TO STRUCTURAL TIMBERS & FACE OF BRICKS EXCLUDING BATTENS, PLASTERBOARD ETC.
- ALL DIMENSIONS ON PLAN ARE NOMINAL & MAY VARY TO ACTUAL SIZE
- PROVIDE LOCKS TO ALL OPENABLE WINDOWS & EXTERNAL SLIDING DOORS (KEYED ALIKE).
- MAN HOLE LOCATION MAY BE CHANGED DUE TO TRUSS LAYOUT.
- WINDOW AND DOOR FRAME SIZES ARE NOMINAL AND MAY VARY WITH LONG ISLAND HOMES APPROVED SUPPLIERS.

CLIENT
I / WE.....
CONFIRM THESE DRAWINGS ACCORD WITH OUR REQUIREMENTS AND AUTHORISE THEIR USE FOR NEXT STAGE PURPOSES.
SIGNED..... DATE.....
SIGNED..... DATE.....

SHEET CONTENT:
SHADOW DIAGRAM - 2PM
HOUSE TYPE:
SANYA 380
MIN LOT WIDTH:
12M
PROPERTY ADDRESS:
2251 SKODA CIRCUIT
POINTCOOK
CLIENT:
CLARE FRANSIS & CHRISTPHER
KEVIN GRIFFITHS

NORTH:		FACADE:		SHEET NUMBER: 11.6	JOB NUMBER:
		SCALE: 1 : 200			JOB ISSUE: H
		DATE:			
REVISIONS	ISSUE	DATE	REVISION DESCRIPTION		INITIALS
	B	29.07.21	R & C		CM
	C	04.08.21	R & C ADD AREA		CM
	D	20.09.21	COLOUR, PRE CONTRACT CLARIFICATION 06/09/21		CM
	E	27.09.21	ENERGY UPGRADES (OPT 2) & CLARIFICATION 27.09.21		CM
	F	27.09.21	WIR DOOR		CM
	G	29.09.21	ADDED ENGINEERING		CM
	H	27.10.21	CONTRACT QUOTE COMMENTS		CM

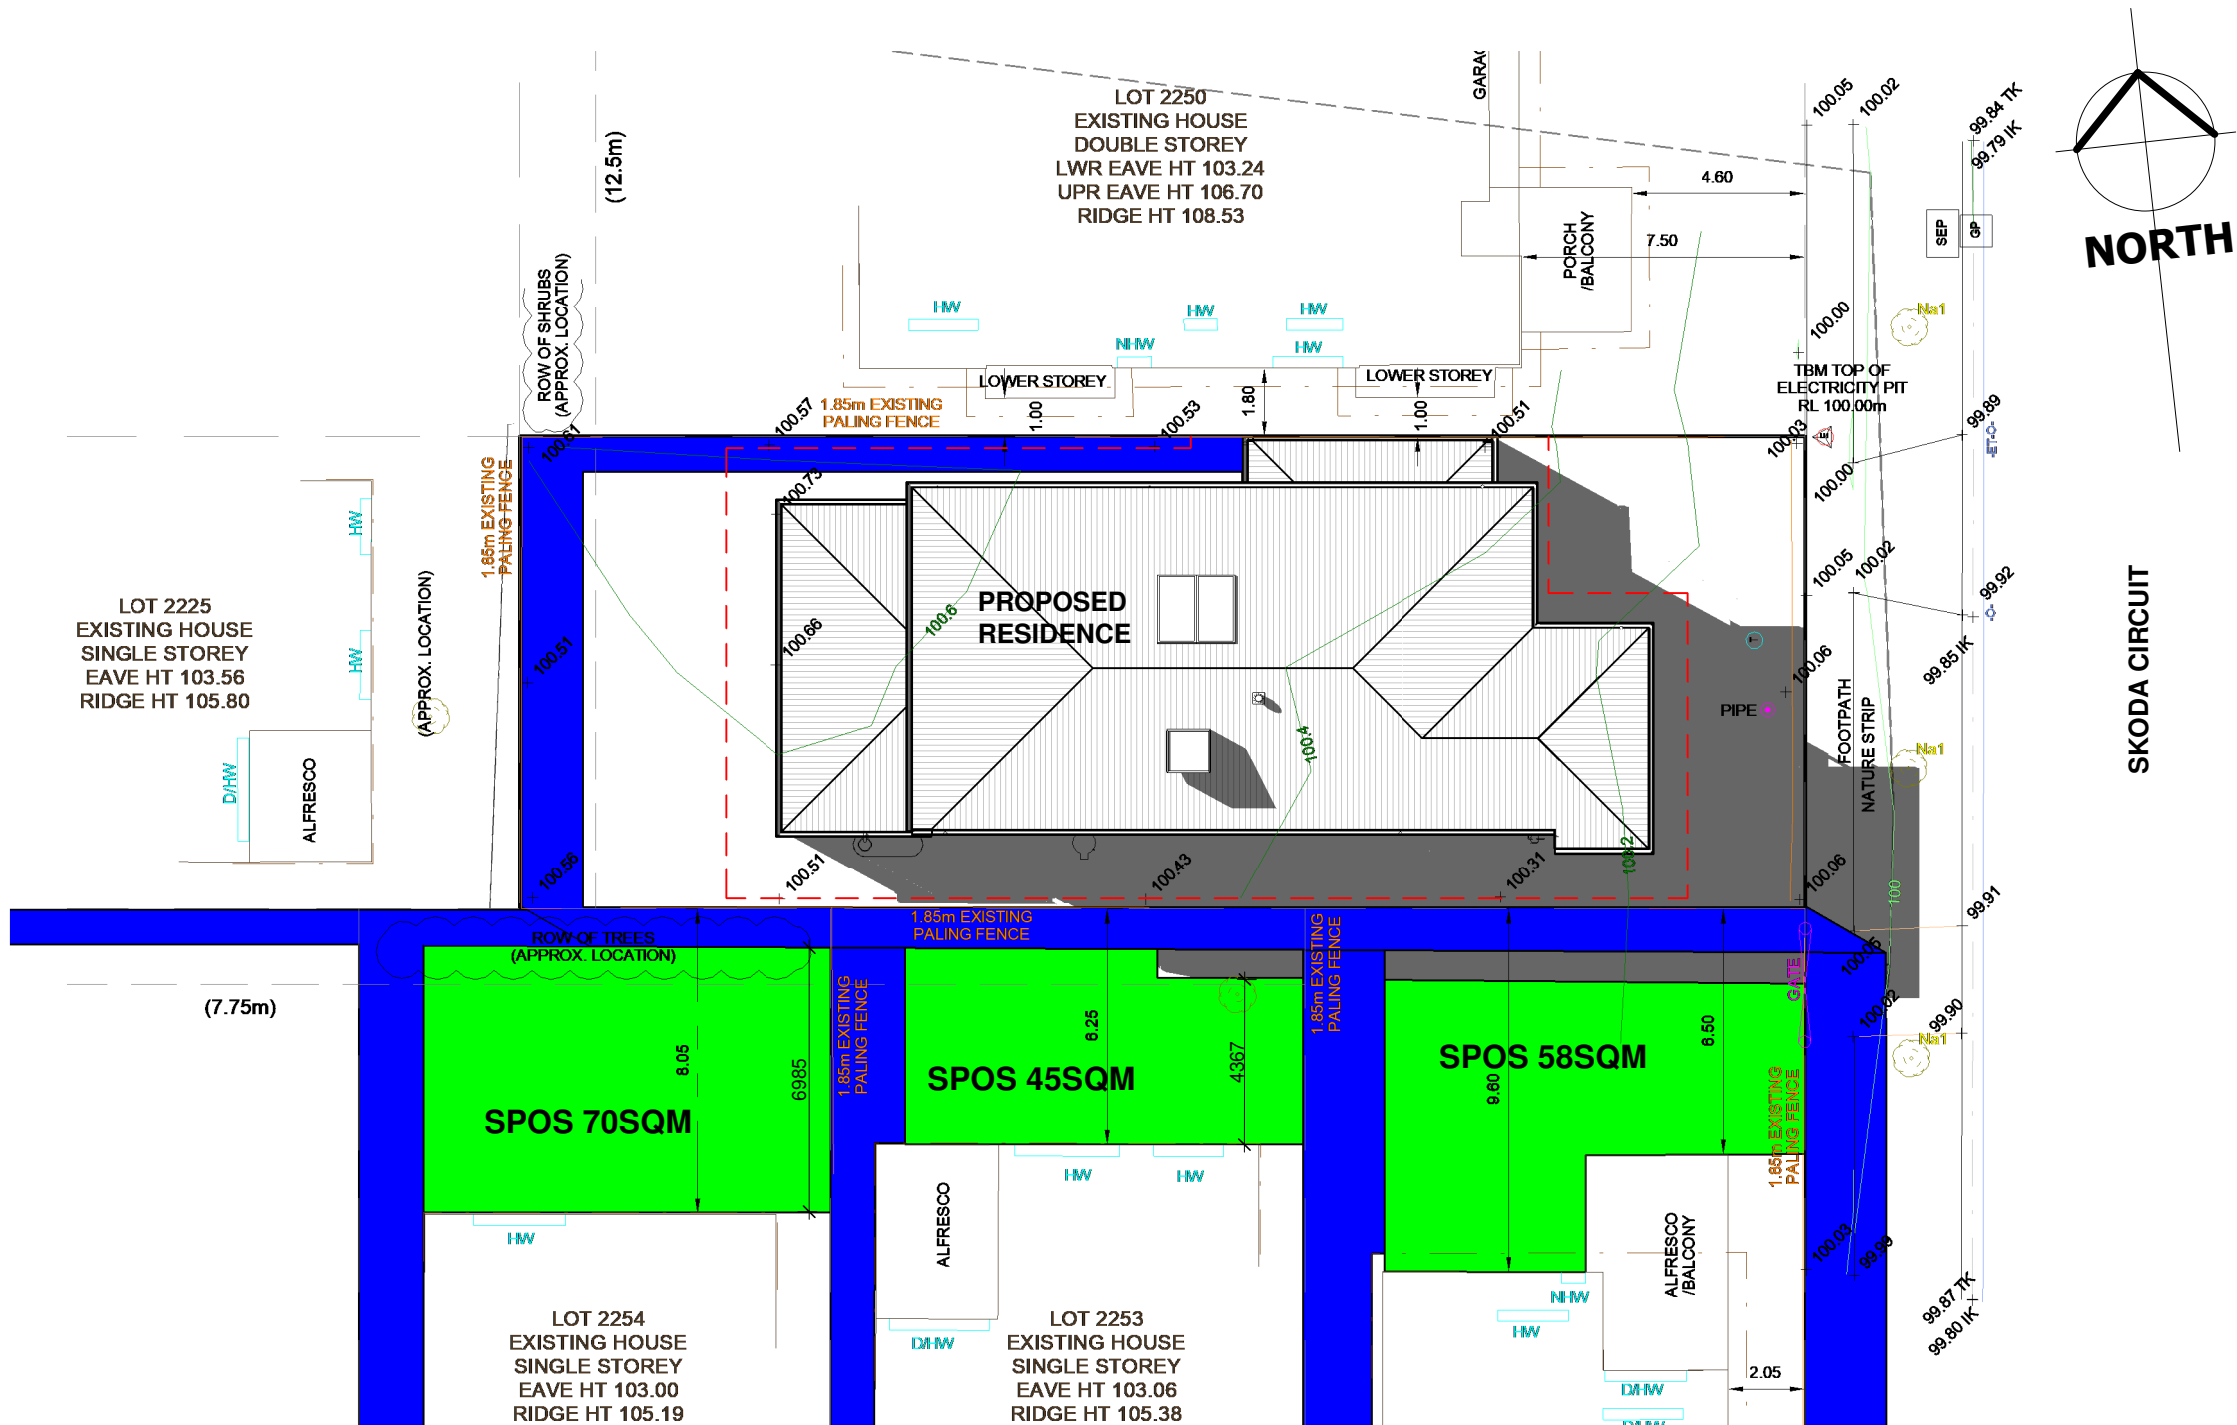

Long Island Homes Pty. Ltd.
PO BOX 6269
Point Cook, Vic 3030
p. 61 3 9369 6486 (1800 604 011)
f. 61 3 9369 0994
email: admin@longislandhomes.com.au
www.longislandhomes.com.au

© Copyright
THIS DESIGN & DRAWING SHALL REMAIN THE INTELLECTUAL PROPERTY OF
LONG ISLAND HOMES PTY. LTD. AND SHALL NOT BE COPIED IN WHOLE OR
PART WITHOUT WRITTEN CONSENT FROM LONG ISLAND HOMES PTY LTD.
DB NUMBER

GENERAL NOTES:

- THE CONTRACTOR IS RESPONSIBLE FOR SETTING OUT AND CHECKING ALL LEVELS AND DIMENSIONS ON SITE PRIOR TO COMMENCING ANY SITE WORKS.
- FIGURED DIMENSIONS ARE TO TAKE PREFERENCE OVER SCALE
- DIMENSIONS TO STRUCTURAL TIMBERS & FACE OF BRICKS EXCLUDING BATTENS, PLASTERBOARD ETC.
- ALL DIMENSIONS ON PLAN ARE NOMINAL & MAY VARY TO ACTUAL SIZE
- PROVIDE LOCKS TO ALL OPENABLE WINDOWS & EXTERNAL SLIDING DOORS (KEYED ALIKE).
- MAN HOLE LOCATION MAY BE CHANGED DUE TO TRUSS LAYOUT.
- WINDOW AND DOOR FRAME SIZES ARE NOMINAL AND MAY VARY WITH LONG ISLAND HOMES APPROVED SUPPLIERS.

CLIENT

I / WE.....

CONFIRM THESE DRAWINGS ACCORD WITH OUR REQUIREMENTS AND AUTHORISE THEIR USE FOR NEXT STAGE PURPOSES.

SIGNED..... DATE.....

SIGNED..... DATE.....

SHEET CONTENT:

SHADOW DIAGRAM - 3PM

HOUSE TYPE: SANYA 380 MIN LOT WIDTH: 12M

PROPERTY ADDRESS:
2251 SKODA CIRCUIT
POINTCOOK

CLIENT:

CLARE FRANSIS & CHRISTPHER
KEVIN GRIFFITHS

NORTH:

FACADE:

SCALE: 1 : 200

DATE:

SHEET NUMBER:

11.7

JOB NUMBER:

JOB ISSUE:

H

REVISIONS	ISSUE	DATE	REVISION DESCRIPTION	INITIALS
B	29.07.21	R & C		CM
C	04.08.21	R & C ADD AREA		CM
D	20.09.21	COLOUR, PRE CONTRACT CLARIFICATION 06/09/21		CM
E	27.09.21	ENERGY UPGRADES (OPT 2) & CLARIFICATION 27.09.21		CM
F	27.09.21	WIR DOOR		CM
G	29.09.21	ADDED ENGINEERING		CM
H	27.10.21	CONTRACT QUOTE COMMENTS		CM