


188 MONCRIEFF CRESCENT

WANDANA HEIGHTS

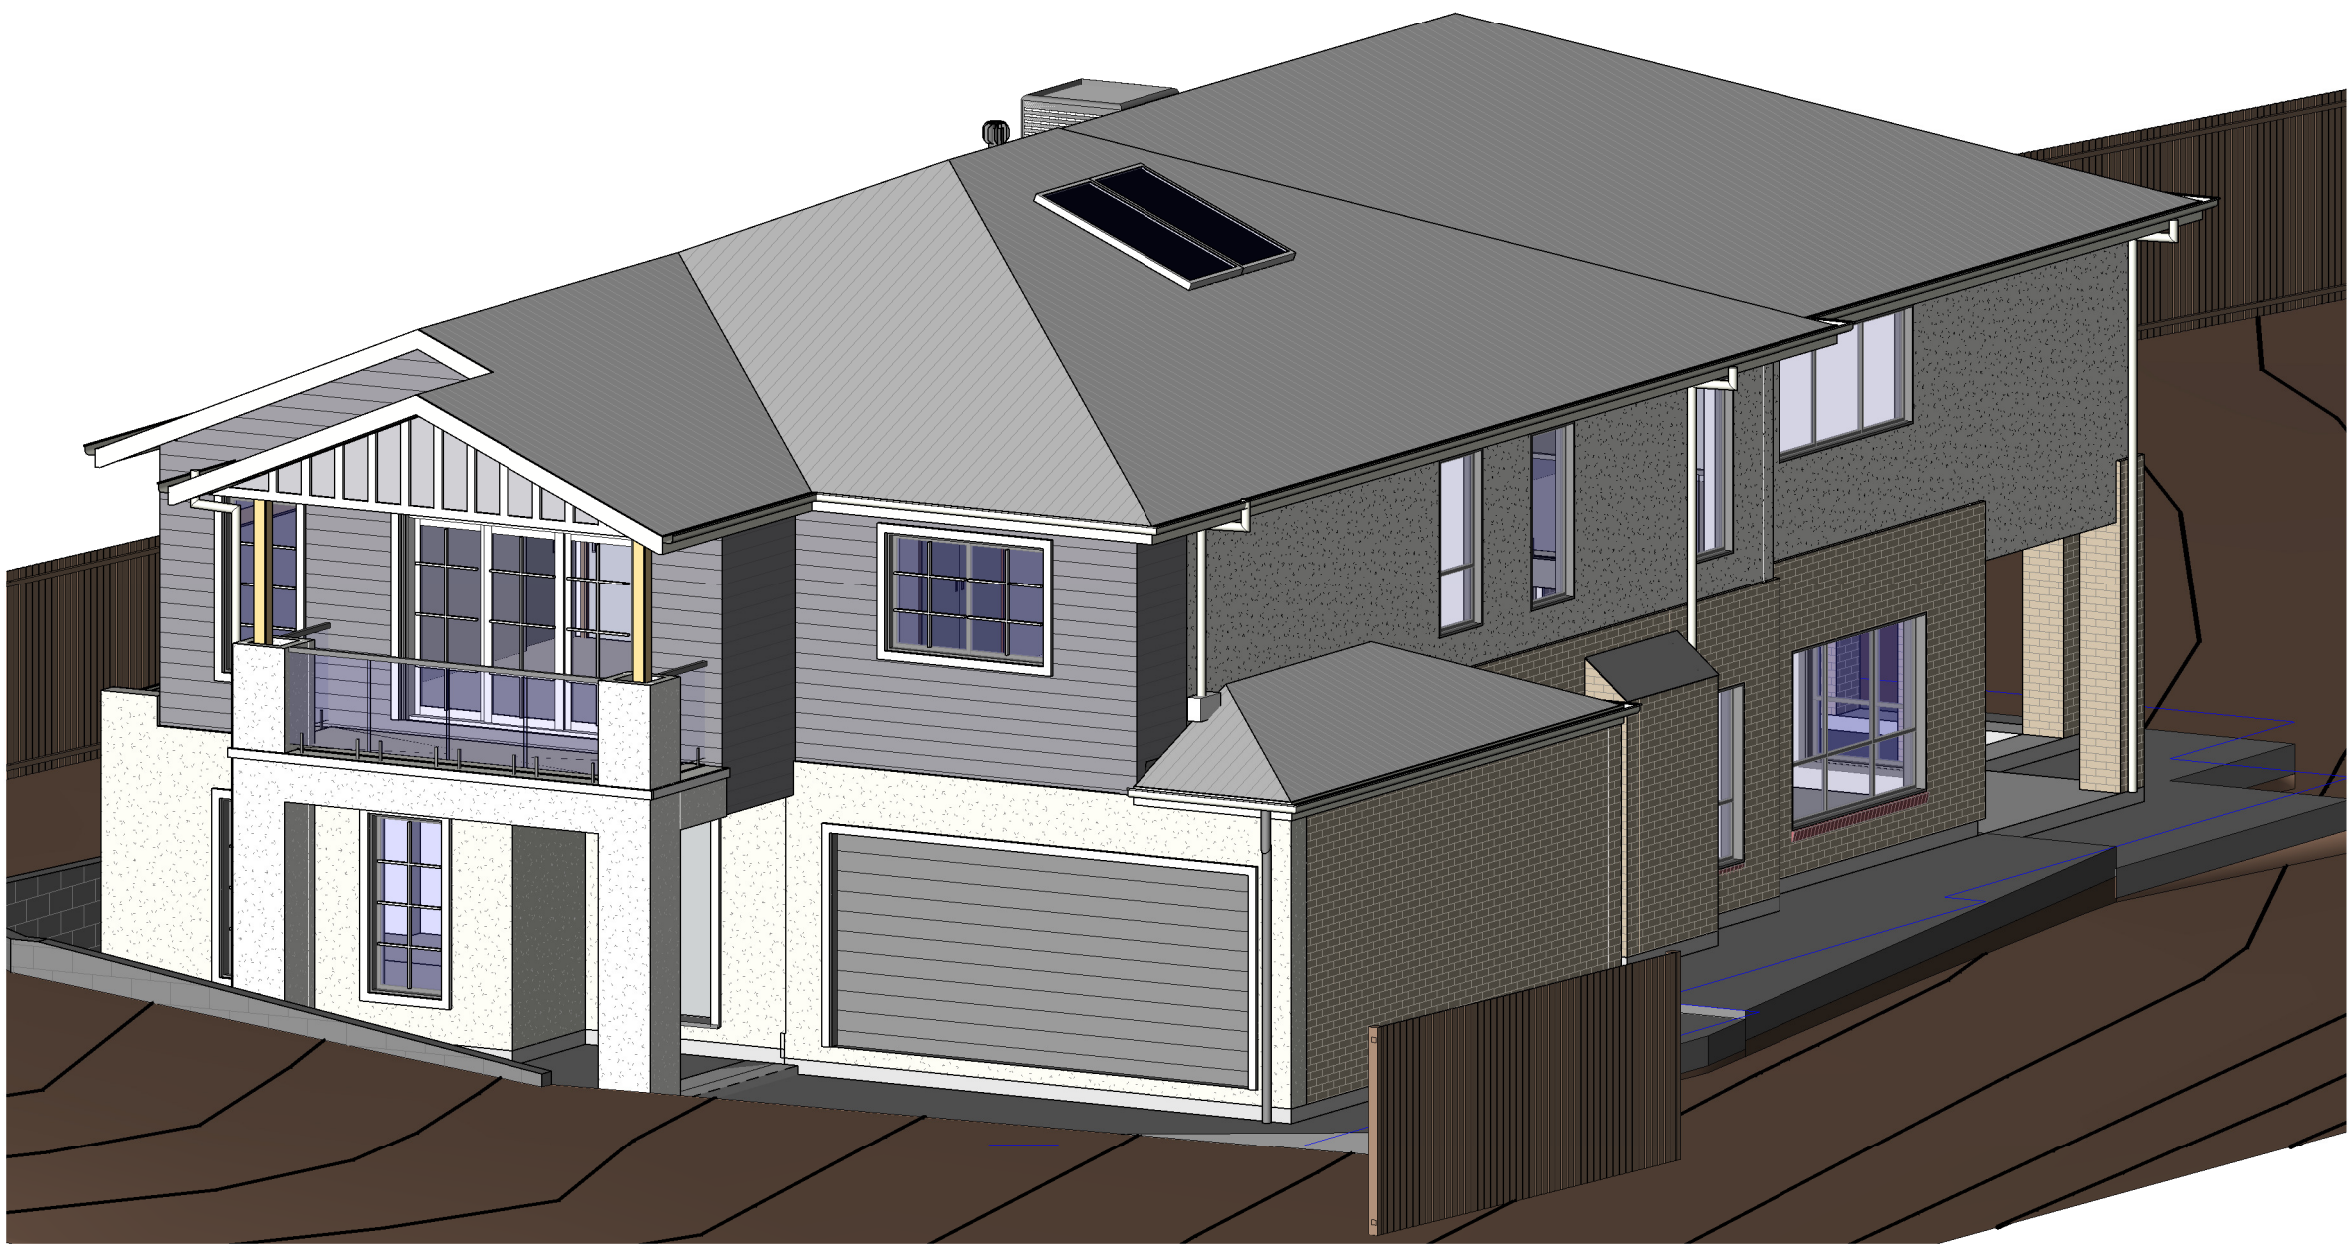

SHEET NO	DESCRIPTION
1.1	FACE SHEET & INDEX
1.2	GENERAL NOTES
2.1	SITE PLAN
3.1	PLAN - GROUND FLOOR
3.2	PLAN - FIRST FLOOR
4.1	ELEVATIONS A & B
4.2	ELEVATIONS C & D
5.1	ELECTRICAL - GROUND FLOOR
5.2	ELECTRICAL - FIRST FLOOR
6.1	FLOORING - GROUND FLOOR
6.2	FLOORING - FIRST FLOOR
7.1	SECTION
7.2	STAIR DETAILS
7.3	BALCONY DETAILS
8.1	KITCHEN, BUTLERS & PDR
8.2	L'DRY,ENS 1
8.3	ENS 2, ENS 3, ENS 4
8.4	LIVING & TYPICAL
9.1	LANDSCAPE PLAN
10.1	SLAB LAYOUT PLAN
11.1	OVERLOOKING
11.2	9am SHADOW
11.3	10am SHADOW
11.4	11am SHADOW
11.5	12pm SHADOW
11.6	1pm SHADOW
11.7	2pm SHADOW
11.8	3pm SHADOW

GRAPHICAL PRESENTATION ONLY

 LONG ISLAND HOMES ISLANDER	Long Island Homes Pty. Ltd. PO BOX 6269 Point Cook, Vic 3030 p. 61 3 9369 6486 (1800 604 011) f. 61 3 9369 0994 email: admin@longislandhomes.com.au www.longislandhomes.com.au	GENERAL NOTES: - THE CONTRACTOR IS RESPONSIBLE FOR SETTING OUT AND CHECKING ALL LEVELS AND DIMENSIONS ON SITE PRIOR TO COMMENCING ANY SITE WORKS. - FIGURED DIMENSIONS ARE TO TAKE PREFERENCE OVER SCALE - DIMENSIONS TO STRUCTURAL TIMBERS & FACE OF BRICKS EXCLUDING BATTENS, PLASTERBOARD ETC. - ALL DIMENSIONS ON PLAN ARE NOMINAL & MAY VARY TO ACTUAL SIZE - PROVIDE LOCKS TO ALL OPENABLE WINDOWS & EXTERNAL SLIDING DOORS (KEYED ALIKE). - MAN HOLE LOCATION MAY BE CHANGED DUE TO TRUSS LAYOUT. - WINDOW AND DOOR FRAME SIZES ARE NOMINAL AND MAY VARY WITH LONG ISLAND HOMES APPROVED SUPPLIERS.	CLIENT I / WE..... CONFIRM THESE DRAWINGS ACCORD WITH OUR REQUIREMENTS AND AUTHORISE THEIR USE FOR NEXT STAGE PURPOSES. SIGNED..... DATE..... SIGNED..... DATE.....	SHEET CONTENT: FACE SHEET & INDEX HOUSE TYPE: HAMPTON 490 MIN LOT WIDTH: 14M PROPERTY ADDRESS: 188 MONCRIEFF CRESCENT WANDANA HEIGHTS CLIENT: SANDEEP & IMMACOLATA BANSAL	NORTH: FACADE: SCALE: DATE: 20.12.22	SHEET NUMBER: 1.1 JOB NUMBER: 0188MON JOB ISSUE: I	<table><tr><th>ISSUE</th><th>DATE</th><th>REVISION DESCRIPTION</th><th>INITIALS</th></tr><tr><td>A</td><td>10.03.20</td><td>MASTER ISSUED</td><td>MP</td></tr><tr><td>B</td><td>9.11.21</td><td>AMEDED CAS. LIV. BULKHEAD TO LIGHT WEIGHT</td><td>MP</td></tr><tr><td>C</td><td>07.11.22</td><td>TENDER DRAWINGS, IDU & COLOUR DOC ADDED</td><td>CM</td></tr><tr><td>D</td><td>09.11.22</td><td>COLOUR CHECK ADDED</td><td>CM</td></tr><tr><td>E</td><td>10.11.22</td><td>ENERGY ADDED</td><td>CM</td></tr><tr><td>F</td><td>17.11.22</td><td>DA RFI</td><td>BL</td></tr><tr><td>G</td><td>30.11.22</td><td>ENG. ADDED, CONTRACT DRAWINGS ISSUED</td><td>BL</td></tr><tr><td>H</td><td>20.12.22</td><td>B.S RFI & CONTRACT QUOTE AMENDMENT</td><td>BL</td></tr><tr><td>I</td><td>21.12.22</td><td>AMEDED ENEGRY ADDED</td><td>BL</td></tr></table>	ISSUE	DATE	REVISION DESCRIPTION	INITIALS	A	10.03.20	MASTER ISSUED	MP	B	9.11.21	AMEDED CAS. LIV. BULKHEAD TO LIGHT WEIGHT	MP	C	07.11.22	TENDER DRAWINGS, IDU & COLOUR DOC ADDED	CM	D	09.11.22	COLOUR CHECK ADDED	CM	E	10.11.22	ENERGY ADDED	CM	F	17.11.22	DA RFI	BL	G	30.11.22	ENG. ADDED, CONTRACT DRAWINGS ISSUED	BL	H	20.12.22	B.S RFI & CONTRACT QUOTE AMENDMENT	BL	I	21.12.22	AMEDED ENEGRY ADDED	BL
	ISSUE	DATE	REVISION DESCRIPTION	INITIALS	
A	10.03.20	MASTER ISSUED	MP	
B	9.11.21	AMEDED CAS. LIV. BULKHEAD TO LIGHT WEIGHT	MP	
C	07.11.22	TENDER DRAWINGS, IDU & COLOUR DOC ADDED	CM	
D	09.11.22	COLOUR CHECK ADDED	CM	
E	10.11.22	ENERGY ADDED	CM	
F	17.11.22	DA RFI	BL	
G	30.11.22	ENG. ADDED, CONTRACT DRAWINGS ISSUED	BL	
H	20.12.22	B.S RFI & CONTRACT QUOTE AMENDMENT	BL	
I	21.12.22	AMEDED ENEGRY ADDED	BL	

GENERAL NOTES.

DO NOT SCALE DRAWINGS. USE WRITTEN DIMENSIONS ONLY.

THE OWNER, BUILDER AND/OR SUB-CONTRACTORS SHALL VERIFY ALL DIMENSIONS, LEVELS, SETBACKS AND ANY SPECIFICATIONS PRIOR TO COMMENCING ANY WORKS OR ORDERING MATERIALS AND SHALL BE RESPONSIBLE FOR ENSURING THAT ALL BUILDING WORKS CONFORM TO THE BUILDING CODE OF AUSTRALIA, AUSTRALIAN STANDARDS CODES (CURRENT EDITIONS), BUILDING REGULATIONS, LOCAL BY-LAWS AND RESCODE REQUIREMENTS. REPORT ALL DISCREPANCIES TO THIS OFFICE FOR CLARIFICATION.

1. THESE PLANS SHALL BE READ IN CONJUNCTION WITH ANY STRUCTURAL OR CIVIL ENGINEERING COMPUTATIONS AND DRAWINGS.

THESE PLANS SHALL BE READ IN CONJUNCTION WITH THE SOIL REPORT. FOOTINGS ARE TO BE FOUNDED AT THE MINIMUM DEPTHS INDICATED I THE SOIL REPORT.

WHERE THE BUILDING (OTHER THAN A CLASS 10a) IS LOCATED IN A DESIGNATED TERMITE INFESTATION AREA THE BUILDING SHALL BE PROTECTED IN ACCORDANCE WITH THE RELEVANT AUSTRALIAN STANDARDS.

2. STORMWATER SHALL BE TAKEN TO THE LEGAL POINT OF DISCHARGE TO THE SATISFACTION OF THE RELEVANT AUTHORITY.
3. SEWER OR SEPTIC SYSTEMS SHALL BE IN ACCORDANCE WITH THE RELEVANT AUTHORITY REQUIREMENTS.
4. FOOTINGS ARE NOT TO ENCROACH OVER ANY TITLE BOUNDARIES AND/OR EASEMENT LINES.

5. FOR BUILDINGS IN CLOSE PROXIMITY TO THE SEA ENSURE THAT ALL STEELWORK, BRICK CAVITY TIES, STEEL LINTELS ETC. THAT ARE IMBEDDED OR FIXED TO MASONRY BE PROTECTED IN ACCORDANCE WITH A.S. 3700-2018 (TABLE 2.2), HOT DIP GALVANIZED, STAINLESS STEEL OR CADMIUM COATED.

6. BUILDING SETBACKS ARE FROM TITLE LINE (NOT FENCE LINE) REFER TITLE RE-ESTABLISHMENT PLAN FOR CORRECT OFF SETS IN RELATION TO FENCE LINES

7. ALL WET AREAS ARE TO COMPLY WITH B.C.A. 3.8.1 OR A.S. 3740-2010. WALL FINISHES SHALL BE IMPERVIOUS TO A HEIGHT OF 1800MM ABOVE FLOOR LEVEL TO ANY SHOWER ENCLOSURES AND 150MM ABOVE BATHS, BASINS, SINKS AND TROUGHS IF WITHIN 75MM OF THE WALL.

8. RISERS -190MM MAXIMUM, 115MM MINIMUM. GOING -355MM MAXIMUM, 240MM MINIMUM. RISERS AND TREADS ARE TO BE CONSTANT IN SIZE THRU-OUT FLIGHT. PROVIDE NON-SLIP FINISH OR SUITABLE NON-SKID STRIP NEAR EDGE OF NOSING. ENSURE A GAP BETWEEN RISERS IS LESS THAN 125MM OR USE CLOSED RISERS. PROVIDE CONTINUOUS HAND RAILING 1000MM MINIMUM HEIGHT TO BALCONIES AND DECKS WHICH ARE 1000MM OR GREATER ABOVE GROUND LEVEL. HANDRAILS ARE TO BE A MINIMUM OF 865MM ABOVE STAIR NOSINGS AND LANDINGS. GAP BETWEEN BALUSTERS TO BE LESS THAN 125MM.

9. SMOKE ALARMS ARE TO BE PROVIDED AND INSTALLED IN ACCORDANCE WITH A.S. 3786-2014, AND UNLESS INSTALLED IN AN EXISTING PART OF A CLASS 1, 2 OR 3 BUILDING OR A CLASS 4 PART OF A BUILDING THE SMOKE ALARM SHALL BE HARD-WIRED WITH A BATTERY BACK-UP INTERCONNECTED.

SPECIFICATION NOTES:

BRICKWORK:

PROVIDE WALL-TIES TO BRICKWORK AT A MAXIMUM OF 600MM IN EACH DIRECTION AND WITHIN 300MM OF ANY ARTICULATION JOINTS. FOR PERPS AND BEDS JOINTS SPACINGS (REFER TO BCA PART 3.3.1)

TIMBER FRAMING:

ALL TIMBER FRAMING THRU-OUT IS TO BE IN ACCORDANCE WITH A.S. 1684 AND ALSO READ IN CONJUNCTION WITH THE ENGINEERS DETAILS AND DRAWINGS.

FLOORING & FOOTINGS:

FINISHED FLOOR LEVELS ARE NOMINAL ONLY AND SHOULD BE CONFIRMED PRIOR TO START OF WORK.

READ IN ACCORDANCE WITH THE SOIL REPORT REQUIREMENTS. READ IN CONJUNCTION WITH THE ENGINEERS DETAILS FOR ALL FOOTING SIZE & DETAILS.

PLEASE NOTE MINIMUM FOUNDING DEPTH TO BE DETERMINED AS "NOTED" IN THE SOIL REPORT

WALL LINTELS & SUPPORT STUDS THRU-OUT:

FOR ALL EXTERNAL PERIMETER LOAD-BEARING LINTELS AND THEIR SUPPORTING STUDS REFER TO THE ENGINEERS DETAILS AND DRAWINGS AND TO GENERAL SPECIFICATIONS

CARPENTERS TO ALLOW 45MM DOOR STUD AT WALL JUNCTIONS

INTERNAL DOORS:

ALL INTERNAL DOORS ARE TO BE 2040mm HIGH UNLESS NOTED OTHERWISE ON THE PLAN.

WC DOORS:

HINGED DOORS THAT OPEN INWARDS TOWARDS THE PAN BUT THE EDGE OF THE DOOR IS A MINIMUM OF 1200MM AWAY FROM THE PAN AT ITS NEAREST POINT, MUST HAVE DEMOUNTABLE HINGES TO ALLOW EASY REMOVAL OF THE DOOR FROM THE OUTSIDE THE WC COMPARTMENT.

ROOFING:

CONCRETE TILED ROOF OVER ROOF BATTENS AT 330 CTRS. TYPICAL THRU-OUT UNLESS NOTED OTHERWISE. METAL EITHER TIMBER OR METAL BATTENS TO BE USED & FIXED IN ACCORDANCE WITH THE MANUFACTURERS DETAILS & SPECIFICATIONS & PROVIDE APPROVED CAPPING & FLASHING THRU-OUT.

SELECTED TIMBER FRAMED ROOF TRUSS AT 600mm MAX CTRS. TO MANUFACTURERS SPECIFICATIONS UNLESS NOTED OTHERWISE.

PLASTERBOARD LINED CEILINGS THRU-OUT.

SELECTED PROFILE METAL EAVES GUTTER & FASCIA TO THE PERIMETER OF THE ROOF AREA.

ALSO READ IN CONJUNCTION WITH ANY ENGINEERS DETAILS & DRAWINGS FOR ANY ROOF BEAMS, LINTELS, ETC.

4.5mm THICK F.C. SHEET CEILING LINING TO THE UNDERSIDE OF THE FIRST FLOOR EAVES.

LINTEL NOTES:

BUILDER IS TO NOTE THAT LINTELS SELECTED BY THE ENGINEER ARE DESIGNED TO CARRY ONLY STANDARD TILE ROOFING & TRUSS LOADS WHERE ARE AT 600mm MAXIMUM CTRS. IF ANY GIRDER TRUSSES ARE LOCATED DIRECTLY ON ANY LINTELS.

TRUSS MANUFACTURER AND / OR BUILDER IS TO REFER TO THE ENGINEER TO CONFIRM IF LINTEL & SUPPORTING STUDS ARE ADEQUATE.

ENGINEER'S DRAWINGS TAKE PRECEDENCE OVER NOMINAL SIZES INDICATED ON THESE PLANS.

WINDOWS:

ALL GLAZING SHALL CONFORM TO AS2047 AND AS1288-2006 WINDOW SIZES SHOWN ARE NOMINAL DEPENDING ON THE WINDOW MANUFACTURERS CLOSEST STANDARD SPECIFICATIONS.

1. ALL GLAZING IS TO BE IN ACCORDANCE WITH AS2047 AND AS1288-2006
2. READ IN CONJUNCTION WITH THE WINDOW SCHEDULE & ELEVATIONS.
3. ALL EXTERNAL DOORS ARE TO FITTED WITH WEATHER STRIPS.
4. 'F' DENOTES FIXED GLAZING, 'O' DENOTES OPENABLE SASH.

NOTE: THESE HEIGHTS MAY VARY SLIGHTLY ACCORDING TO DIFFERENCES IN BRICK SIZES.

WALLING:

90mm WIDE STUD FRAME WALLS THRU-OUT

MGP10 GRADE

90x35 COMMON STUDS

70x35 NOGGINGS

2(90x35) TOP PLATES

2(90x45) JAMB STUDS

LININGS:

10mm PLASTERBOARD TO ALL INTERNAL WALLS. 10mm PLASTERBOARD TO CEILINGS. SELECTED WATER RESISTANT SUB-STRATE & TILING TO WE AREAS.

HEATING & COOLING:

ALL HEATING & COOLING UNITS, SIZES, TYPES & LOCATIONS ARE TO BE CONFIRMED BETWEEN THE BUILDER & THE SUPPLIER.

ALL HEATING & COOLING DUCTS & VENT LOCATIONS ARE TO BE CONFIRMED BY THE BUILDER PRIOR TO COMMENCEMENT OF BUILDING TO DETERMINE IF ANY ADDITIONAL RISER DUCTS ARE REQUIRED.

ALL HEATING & COOLING POINTS LOCATIONS, MAY VARY FROM PLAN TO PLAN.

GEOTECHNICAL:

THESE DRAWINGS ARE TO BE READ IN CONJUNCTION WITH A GEOTECHNICAL REPORT. IT IS THE BUILDERS'S RESPONSIBILITY TO OBTAIN SUCH REPORTS PRIOR TO COMMENCEMENT OF WORKS.

FULL HEIGHT CONTROL JOINTS (FOOTING TO EAVES) AT 5m MAX CTRS UNLESS OTHERWISE STATED IN THE SOIL REPORT.

REFER TO SOIL REPORT.

6 STAR ENERGY UPGRADE:

1. ALL EXTERNAL GAPS & CRACKS TO WINDOW/DOOR FRAMES SEALED ON CONSTRUCTION.
2. SISALATION APPLIED TO ALL WALLS, & GAPS/JOINS SEALED.
3. SELF CLOSING EXHAUST FANS THROUGHOUT OR 'DRAFT STOPPER' SHROUDS OVER EXHAUST FANS.
4. WEATHER STRIPS/SEALS TO ALL EXTERNAL HINGED DOORS AND INTERNAL GARAGE ACCESS DOOR.
5. ALL CHIMNEYS FITTED WITH DAMPERS.
6. ALL DOWNLIGHTS OF "CLOSED-RING" TYPE.
7. INSULATION LEVELS AS DETAILED IN ATTACHED ENERGY RATING ASSESSOR'S REPORT.

PAINTWORK:

PROVIDE THREE COAT PAINT SYSTEM INTERNALLY, BASED ON ONE WALL COLOUR THROUGHOUT AND ONE CEILING COLOUR THROUGHOUT.

LINTEL SCHEDULE

MEMBER SIZE	UPPER FLOOR & SINGLE STOREY	LOWER FLOOR (DOUBLE STOREY)
	MAX SIZE OF OPENING (mm)	MAX SIZE OF OPENING (mm)
90x45 F17	1000	800
140x45 F17	1400	1200
190x45 F17	1900	1600
240x45 F17	2400	2000
290x45 F17	2900	2400
190x45 F17	1900	1600
90x45 F17	1000 FRONT DOOR	800
90x45 F17	900 GARAGE REAR DOOR	800

SOIL CLASSIFICATION: "M"

REPORT NO:	170565
BY:	INTRAX
DATE:	12/10/2022
B.A.L.:	LOW
WIND SPEED:	N-3

WALLING FRAME SIZES

EXTERNAL STUDS	450mm
INTERNAL STUDS	450mm

ENERGY REPORT - INSULATION

INSULATION TO BE INSTALLED TO THE FOLLOWING AREAS:	
CEILINGS (EXCLUDING GARAGE)	R 6.0
WALLS (EXCLUDING GARAGE EXTERNAL WALLS)	R 2.5 + SISALATION
FLOORS (FLOOR ABOVE PORCH, GARAGE & ALFRESCO)	R 4.1
STANDARD INCLUSION FOR LONG ISLAND HOMES PROVIDE INSULATION TO: EXTERNAL DWELLING WALLS, WALL BETWEEN GARAGE AND HOUSE AND CEILING DIRECTLY UNDER ROOF SPACE EXCLUDED INSULATION TO GARAGE CEILING SPACE, GARAGE EXTERNAL WALLS AND GROUND FLOOR CEILING UNDER 1ST FLOOR OF DOUBLE STOREY HOMES. NOTE: WHERE SITE LEVELS ARE NOT AVAILABLE, THE BUILDER ASSUMES THE DWELLING SITS 200MM ABOVE N.G.L. FOR ENERGY REPORT PURPOSES.	
REQUIREMENTS ARE AS PER ENERGY REPORT - REF NO#TD0B3L9IAZ-04	
DATES	24/12/2022



ISLANDER

Long Island Homes Pty. Ltd.
PO BOX 6269
Point Cook, Vic 3030
p. 61 3 9369 6486 (1800 604 011)
f. 61 3 9369 0994
email: admin@longislandhomes.com.au
www.longislandhomes.com.au

© Copyright
THIS DESIGN & DRAWING SHALL REMAIN THE INTELLECTUAL PROPERTY OF LONG ISLAND HOMES PTY. LTD. AND SHALL NOT BE COPIED IN WHOLE OR PART WITHOUT WRITTEN CONSENT FROM LONG ISLAND HOMES PTY LTD.
DB NUMBER: CDB - U 58094

GENERAL NOTES:

- THE CONTRACTOR IS RESPONSIBLE FOR SETTING OUT AND CHECKING ALL LEVELS AND DIMENSIONS ON SITE PRIOR TO COMMENCING ANY SITE WORKS.
- FIGURED DIMENSIONS ARE TO TAKE PREFERENCE OVER SCALE
- DIMENSIONS TO STRUCTURAL TIMBERS & FACE OF BRICKS EXCLUDING BATTENS, PLASTERBOARD ETC.
- ALL DIMENSIONS ON PLAN ARE NOMINAL & MAY VARY TO ACTUAL SIZE
- PROVIDE LOCKS TO ALL OPENABLE WINDOWS & EXTERNAL SLIDING DOORS (KEYED ALIKE).
- MAN HOLE LOCATION MAY BE CHANGED DUE TO TRUSS LAYOUT.
- WINDOW AND DOOR FRAME SIZES ARE NOMINAL AND MAY VARY WITH LONG ISLAND HOMES APPROVED SUPPLIERS.

CLIENT

I / WE.....

CONFIRM THESE DRAWINGS ACCORD WITH OUR REQUIREMENTS AND AUTHORISE THEIR USE FOR NEXT STAGE PURPOSES.

SIGNED..... DATE.....

SIGNED..... DATE.....

SHEET CONTENT:

GENERAL NOTES

HOUSE TYPE: HAMPTON 490

MIN LOT WIDTH: 14M

PROPERTY ADDRESS:
188 MONCRIEFF CRESCENT
WANDANA HEIGHTS

CLIENT:
SANDEEP & IMMACOLATA BANSAL

NORTH:

FACADE:

SCALE: 1 : 1

DATE: 20.12.22

SHEET NUMBER:

1.2

JOB NUMBER:

0188MON

JOB ISSUE:

1

REVISIONS

ISSUE	DATE	REVISION DESCRIPTION	INITIALS
A	10.03.20	MASTER ISSUED	MP
B	9.11.21	AMEDED GAS. LIV. BULKHEAD TO LIGHT WEIGHT	MP
C	07.11.22	TENDER DRAWINGS, IDU & COLOUR DOC ADDED	CM
D	09.11.22	COLOUR CHECK ADDED	CM
E	10.11.22	ENERGY ADDED	CM
F	17.11.22	DA RFI	BL
G	30.11.22	ENG. ADDED, CONTRACT DRAWINGS ISSUED	BL
H	20.12.22	B.S RFI & CONTRACT QUOTE AMENDMENT	BL
I	21.12.22	AMEDED ENEGRY ADDED	BL


LEGEND				
	- GAS METER		- ELEC. POLE	P.O.S
	- HOT WATER SYSTEM		- SIDE ENTRY PIT	
	- METER BOX		- WATER VALVE	
	- TITLE PEG		- S/W PROPERTY INLET	
	- SEWER VENT / I.S.		- WATER METER	
	- TELSTRA PIT		- STORM WATER PIT	
	- TREE		- TBM	
	- STREET SIGN	HAB	- HABITABLE ROOM WINDOW	
	- SEWER MANHOLE	GW	- SIGN STAMPED ON CONCRETE KERB	
	- ELECT. PIT	NHAB	- NON-HABITABLE ROOM WINDOW	
				

TOTAL HOUSE AREA		
TOTAL HOUSE AREA	258.68	m²
SITE AREA	1265	m²
SITE COVERAGE	20.45	%
PAVING	44.70	m²
PERMEABLE COVERAGE	76.02	%
GARDEN AREA	74.62	%

ROOF SCHEDULE	
TYPE	AREA
Metal Roof - 145mm	297.42 m²

LOT 188A
HOUSE UNDER
CONSTRUCTION
SINGLE STOREY
EAVE HT 101.23
RIDGE HT 101.42
(LOCK UP STAGE)
AS OF 21.10.22

PROPOSED RETURN FENCING - 1.8m(H)
CAPPED & LAPPED TIMBER PALING
FENCING WITH EXPOSED POSTS ON BOTH
SIDES, AS PER DEVELOPERS
GUIDELINES, BY OWNER.

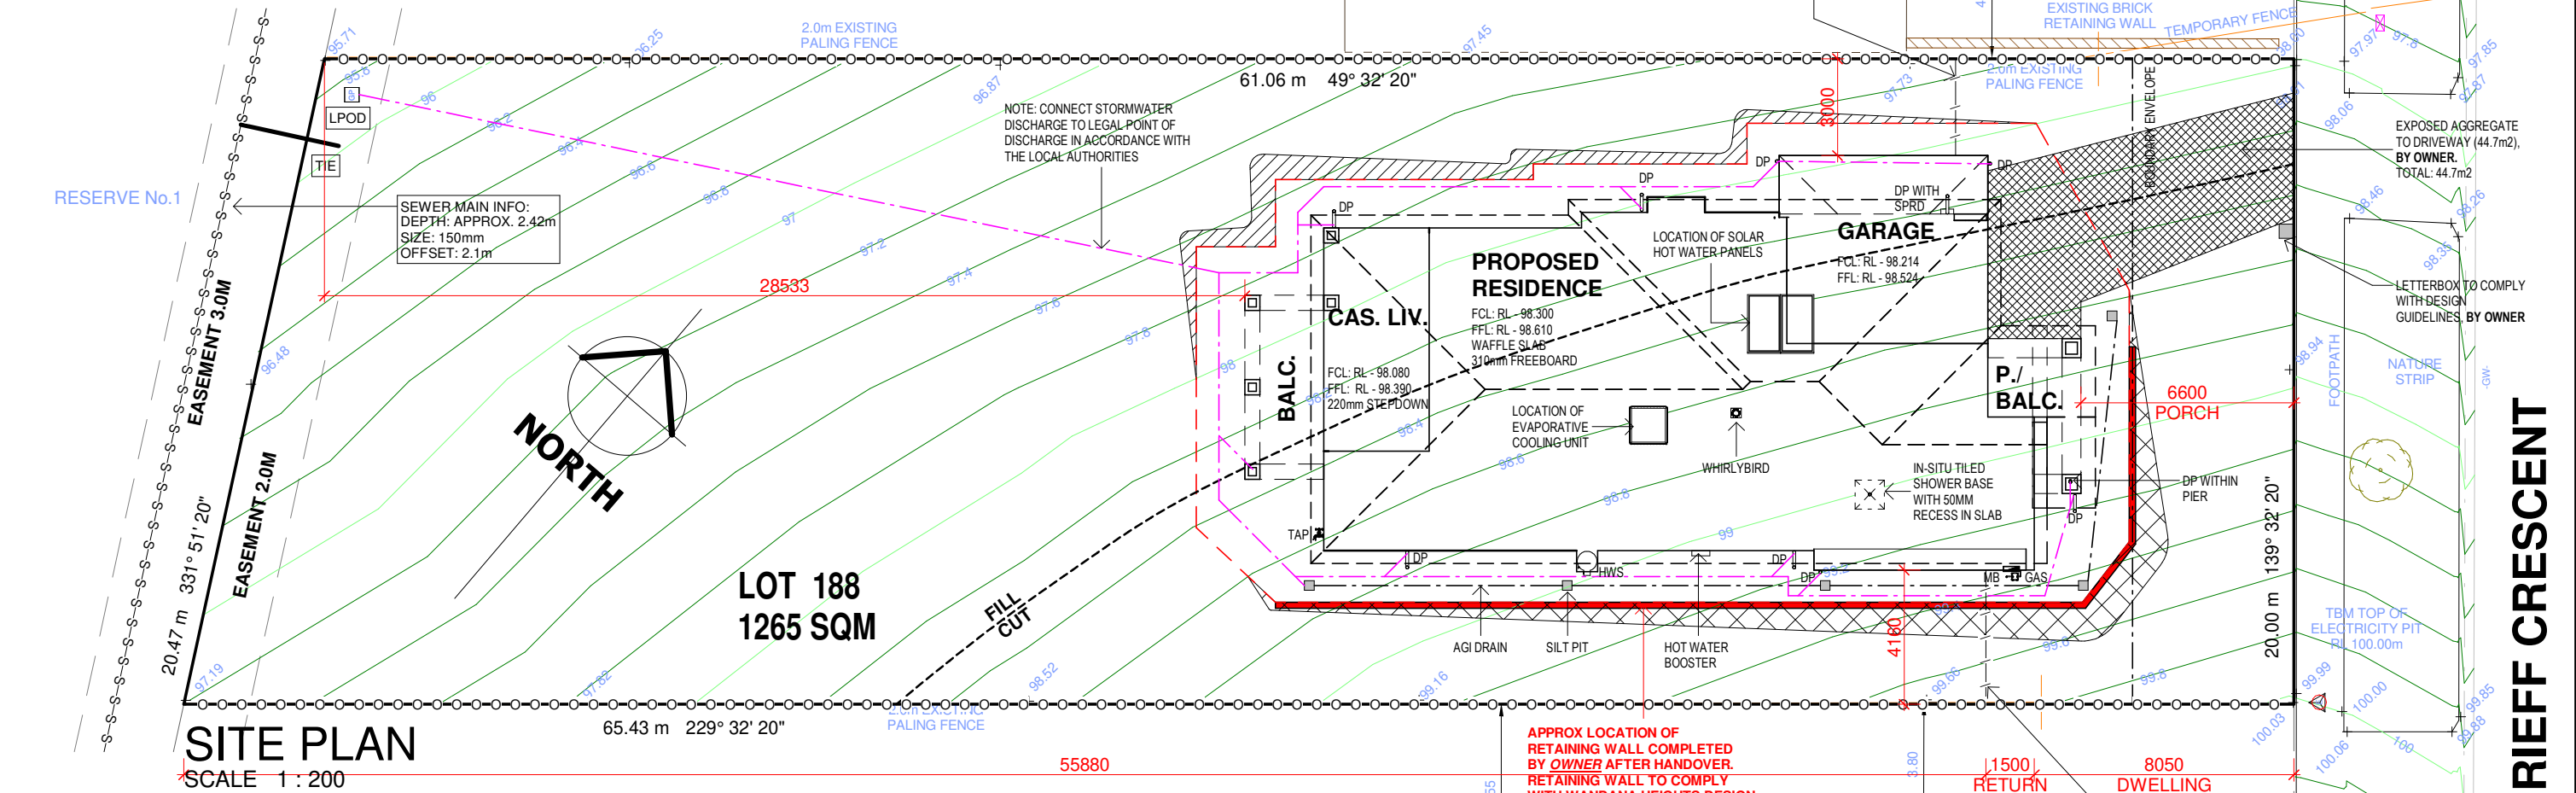

NOTE: SITE SCRAPE
SCRAPE SITE TO REMOVE SURFACE VEGETATION AND PROVIDE LEVEL BUILDING PLATFORM. PROVIDE ADDITIONAL CUT TO GARAGE AREA TO ACCOMMODATE 86mm SLAB STEP DOWN.

NOTE: SITE CLEAR
LONG ISLAND HOMES REQUIRES THE SITE TO BE CLEAR OF ALL OBSTRUCTIONS, INCLUDING EXISTING SITE RUBBLE, EXISTING STRUCTURES, PAVING AND FENCING, PRIOR TO SITE START.

NOTE: BACK FILL
SITE TO BE BACK FILLED TO REBATE HEIGHT & FALL AWAY FROM DWELLING.

NOTE: DRIVEWAY GRADIENT
DRIVEWAY TO BE GRADED TO ENSURE MAXIMUM 1:6 GRADIENT FROM CROSSOVER TO GARAGE FLOOR.

NOTE: EASEMENTS
FOUNDATION MAYBE AFFECTED DUE TO PIPE DEPTH AND RESULTING ANGLE OF REPOSE CONSIDERATIONS.

NOTE: TERMITE PROTECTION
PROVIDE TERMITE TREATMENT IN ACCORDANCE WITH AS 3660.1

SITE SPECIFIC NOTES

NOTE: DRIVEWAY, PORCH & PATH
DRIVEWAY, PORCH & FRONT PATH TO BE CONSTRUCTED OF EXPOSED AGGREGATE, COMPLETED BY OWNER & TO COMPLY WITH RELEVANT DESIGN GUIDELINES.

NOTE: FENCING
SIDE, REAR & WING FENCE TO BE CONSTRUCTED AS PER DEVELOPERS GUIDELINES REQUIREMENTS & COMPLETED BY OWNER.

NOTE: AUTHORITY APPROVAL
SITING OF PROPOSED RESIDENCE IS SUBJECT TO APPROVAL BY DEVELOPER AND RELEVANT LOCAL AUTHORITY.



Long Island Homes Pty. Ltd.
PO BOX 6269
Point Cook, Vic 3030
p. 61 3 9369 6486 (1800 604 011)
f. 61 3 9369 0994
email: admin@longislandhomes.com.au
www.longislandhomes.com.au

© Copyright
THIS DESIGN & DRAWING SHALL REMAIN THE INTELLECTUAL PROPERTY OF LONG ISLAND HOMES PTY. LTD. AND SHALL NOT BE COPIED IN WHOLE OR PART WITHOUT WRITTEN CONSENT FROM LONG ISLAND HOMES PTY LTD.
DB NUMBER: CDB - U 58094

GENERAL NOTES:

- THE CONTRACTOR IS RESPONSIBLE FOR SETTING OUT AND CHECKING ALL LEVELS AND DIMENSIONS ON SITE PRIOR TO COMMENCING ANY SITE WORKS.
- FIGURED DIMENSIONS ARE TO TAKE PREFERENCE OVER SCALE
- DIMENSIONS TO STRUCTURAL TIMBERS & FACE OF BRICKS EXCLUDING BATTENS, PLASTERBOARD ETC.
- ALL DIMENSIONS ON PLAN ARE NOMINAL & MAY VARY TO ACTUAL SIZE
- PROVIDE LOCKS TO ALL OPENABLE WINDOWS & EXTERNAL SLIDING DOORS (KEYED ALIKE).
- MAN HOLE LOCATION MAY BE CHANGED DUE TO TRUSS LAYOUT.
- WINDOW AND DOOR FRAME SIZES ARE NOMINAL AND MAY VARY WITH LONG ISLAND HOMES APPROVED SUPPLIERS.

CLIENT

I / WE.....

CONFIRM THESE DRAWINGS ACCORD WITH OUR REQUIREMENTS AND AUTHORISE THEIR USE FOR NEXT STAGE PURPOSES.

SIGNED..... DATE.....

SIGNED..... DATE.....

SHEET CONTENT:
SITE PLAN

HOUSE TYPE:
HAMPTON 490

MIN LOT WIDTH:
14M

PROPERTY ADDRESS:
**188 MONCRIEFF CRESCENT
WANDANA HEIGHTS**

CLIENT:
SANDEEP & IMMACOLATA BANSAL

NORTH:		FACADE:		SHEET NUMBER: 2.1	JOB NUMBER: 0188MON	
		SCALE: As indicated			JOB ISSUE:	
		DATE: 20.12.22			I	
REVISIONS	ISSUE	DATE	REVISION DESCRIPTION			INITIALS
	A	10.03.20	MASTER ISSUED			MP
	B	9.11.21	AMEDED CAS. LIV. BULKHEAD TO LIGHT WEIGHT			MP
	C	07.11.22	TENDER DRAWINGS, IDU & COLOUR DOC ADDED			CM
	D	09.11.22	COLOUR CHECK ADDED			CM
	E	10.11.22	ENERGY ADDED			CM
	F	17.11.22	DA RFI			BL
	G	30.11.22	ENG. ADDED, CONTRACT DRAWINGS ISSUED			BL
	H	20.12.22	B.S RFI & CONTRACT QUOTE AMENDMENT			BL
	I	21.12.22	AMEDED ENRGY ADDED			BL

NOTES

- ALL DIMENSIONS ON PLAN ARE NOMINAL & MAY VARY TO ACTUAL SIZES
- CARPENTERS TO ALLOW 45MM DOOR STUD AT WALL JUNCTIONS
- PROVIDE LOCKS TO ALL OPENABLE WINDOWS & EXTERNAL SLIDING DOORS (KEYED ALIKE)
- MAN HOLE LOCATION MAY BE CHANGED DUE TO TRUSS LAYOUT.
- WINDOW AND DOOR FRAME SIZES ARE NOMINAL AND MAY VARY WITH LONG ISLAND HOMES APPROVED SUPPLIERS.
- ALL WATER CLOSETS TO HAVE REMOVABLE HINGES TO THE DOORS IF THERE IS LESS THAN 1.2m CLEARANCE BETWEEN THE CLOSET PAN & THE DOORWAY.
- WINDOW SIZES ARE INDICATIVE ONLY, ACTUAL WINDOW SIZES TO BE DETERMINED BY VARIOUS WINDOW MANUFACTURERS, WITH 100MM ALLOWANCE OF PLAN SPECIFIED SIZES.

VENTING TO EXHAUST FANS & RANGEHOODS


- EXHAUST FANS TO DISCHARGE DIRECTLY TO OUTSIDE AIR VIA DUCTS

LEGEND

- GAS METER
- METER BOX
- CAPPED GAS
- HOT WATER SYSTEM

SITE SPECIFIC NOTES

- ALL DOOR HEIGHTS TO BE 2040 mm(H) INCLUDING GARAGE ACCESS DOOR UNLESS OTHERWISE NOTED.
- PROVIDE 67 x 18mm PENCIL ROUND ARCHITRAVES AND SKIRTING BOARDS TO ENS 1.
- PROVIDE 67 x 12mm PENCIL ROUND ARCHITRAVES AND SKIRTING BOARDS TO THE REST OF THE HOUSE.
- PROVIDE SQUARE SET CORNICE TO ENS 1.
- PROVIDE 75mm SCOTIA COVE CORNICE.
- PROVIDE FLYSCREENS TO ALL OPENABLE WINDOWS.
- PROVIDE 1NO. PRIVACY LOCKS TO PDR DOOR.
- PROVIDE 2NO. 40KG NOGGIN TO BATTEN FITTING TO ENTRANCE AND VOID.

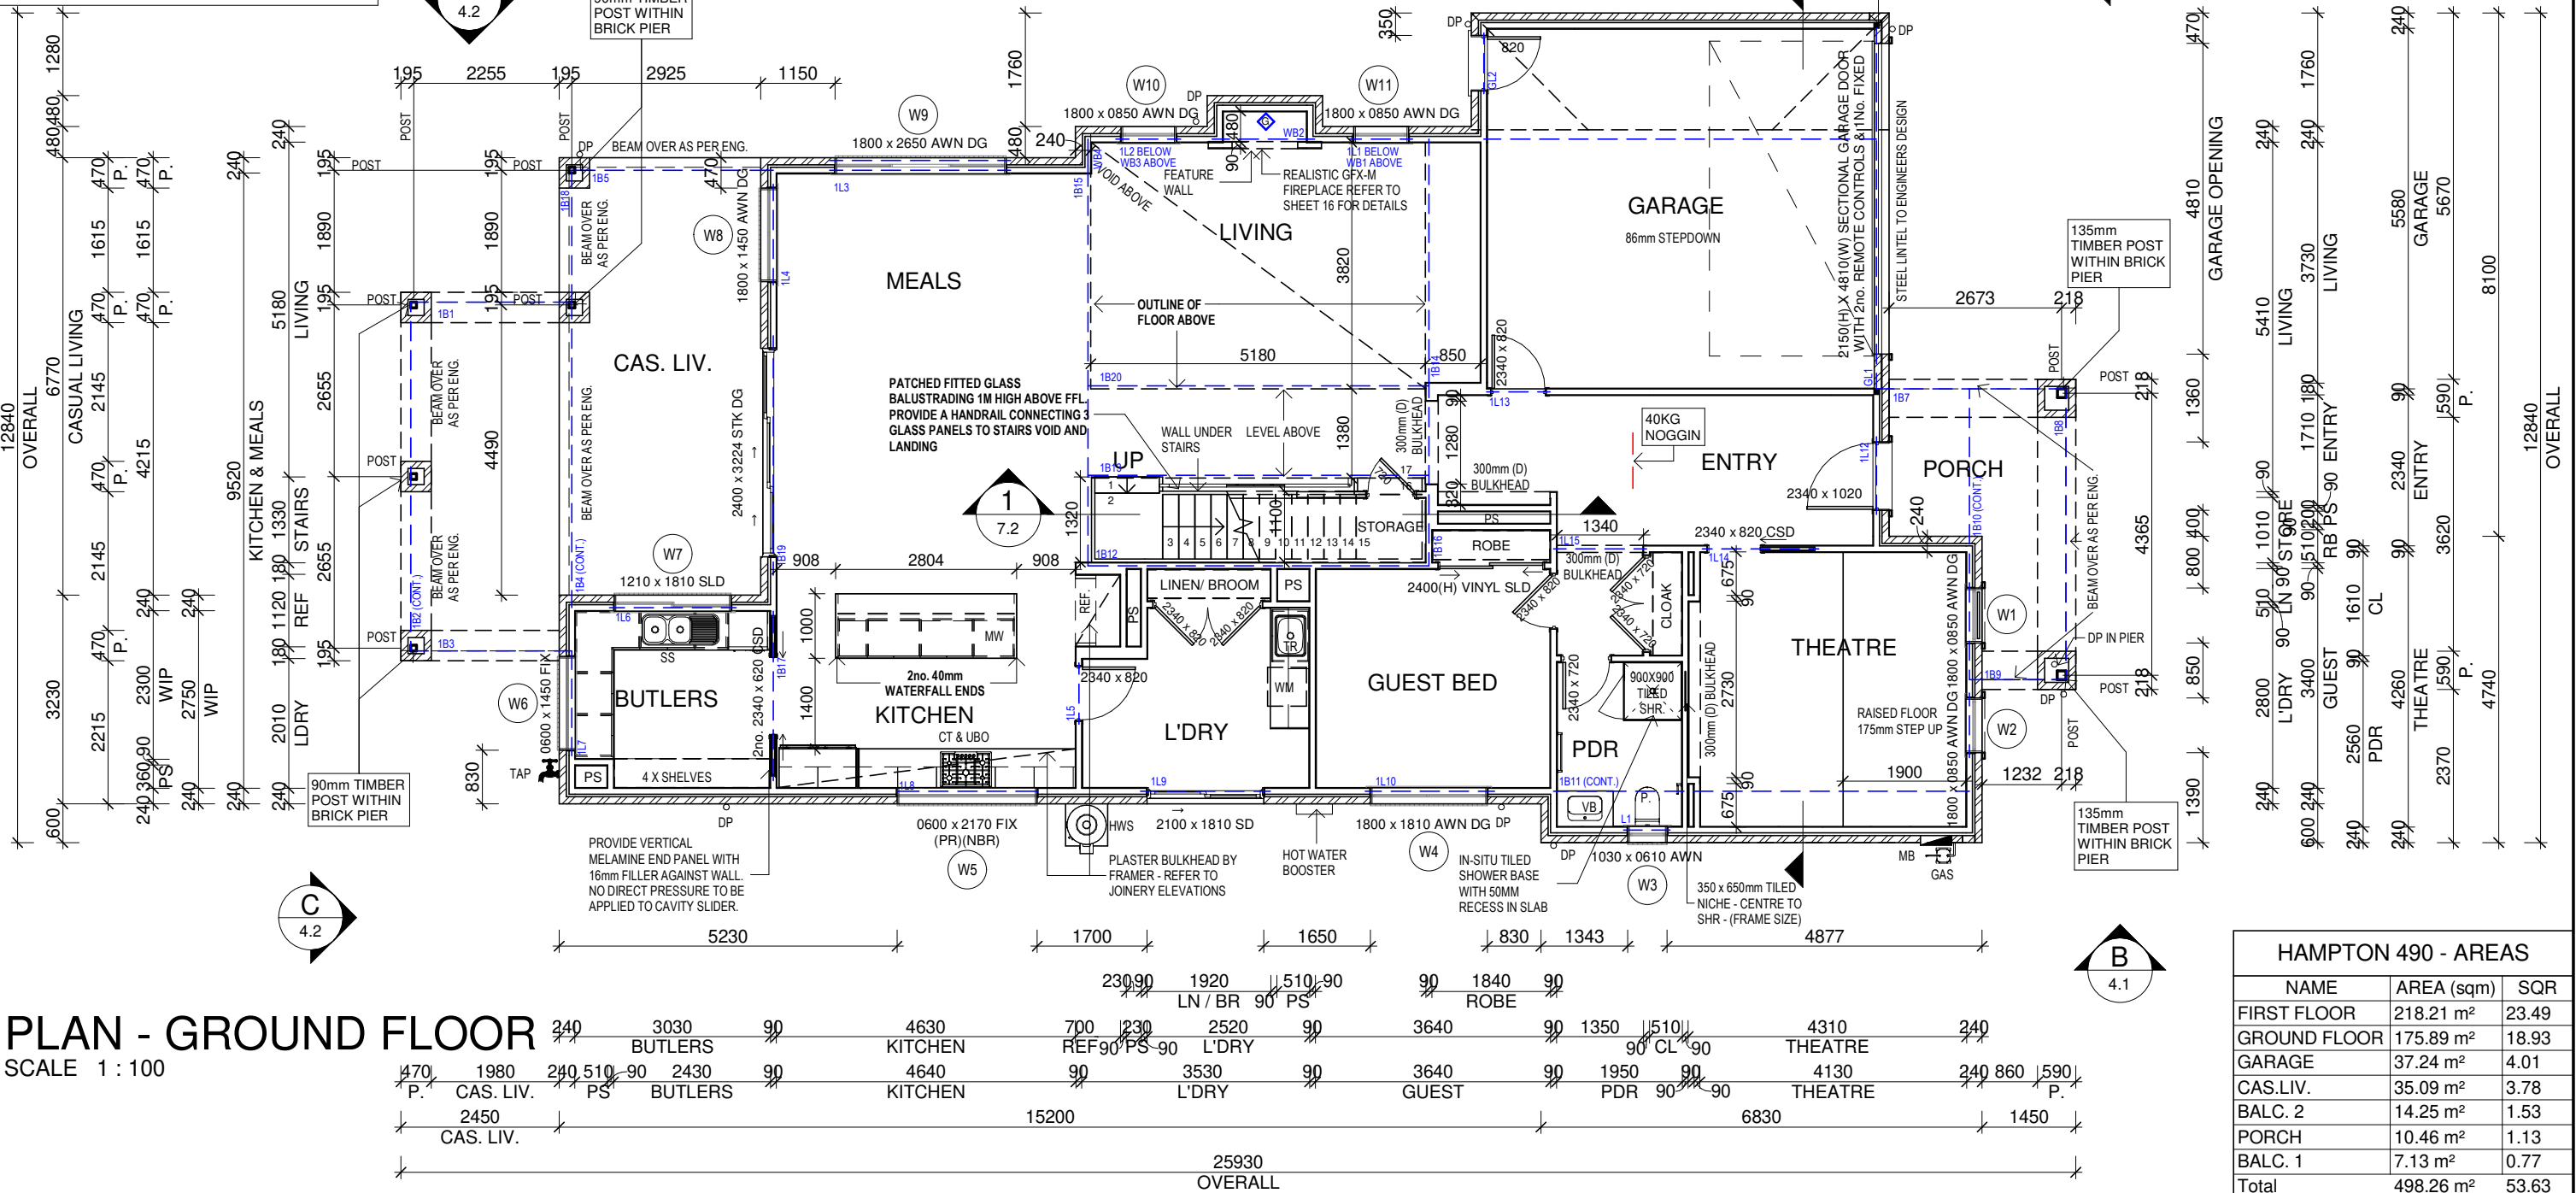

HAMPTON 490 - AREAS

NAME	AREA (sqm)	SQR
FIRST FLOOR	218.21 m ²	23.49
GROUND FLOOR	175.89 m ²	18.93
GARAGE	37.24 m ²	4.01
CAS.LIV.	35.09 m ²	3.78
BALC. 2	14.25 m ²	1.53
PORCH	10.46 m ²	1.13
BALC. 1	7.13 m ²	0.77
Total	498.26 m ²	53.63



Long Island Homes Pty. Ltd.
PO BOX 6269
Point Cook, Vic 3030
p. 61 3 9369 6486 (1800 604 011)
f. 61 3 9369 0994
email: admin@longislandhomes.com.au
www.longislandhomes.com.au

© Copyright
THIS DESIGN & DRAWING SHALL REMAIN THE INTELLECTUAL PROPERTY OF LONG ISLAND HOMES PTY. LTD. AND SHALL NOT BE COPIED IN WHOLE OR PART WITHOUT WRITTEN CONSENT FROM LONG ISLAND HOMES PTY LTD.
DB NUMBER: CDB - U 58094

GENERAL NOTES:

- THE CONTRACTOR IS RESPONSIBLE FOR SETTING OUT AND CHECKING ALL LEVELS AND DIMENSIONS ON SITE PRIOR TO COMMENCING ANY SITE WORKS.
- FIGURED DIMENSIONS ARE TO TAKE PREFERENCE OVER SCALE
- DIMENSIONS TO STRUCTURAL TIMBERS & FACE OF BRICKS EXCLUDING BATTENS, PLASTERBOARD ETC.
- ALL DIMENSIONS ON PLAN ARE NOMINAL & MAY VARY TO ACTUAL SIZE
- PROVIDE LOCKS TO ALL OPENABLE WINDOWS & EXTERNAL SLIDING DOORS (KEYED ALIKE).
- MAN HOLE LOCATION MAY BE CHANGED DUE TO TRUSS LAYOUT.
- WINDOW AND DOOR FRAME SIZES ARE NOMINAL AND MAY VARY WITH LONG ISLAND HOMES APPROVED SUPPLIERS.

CLIENT

I / WE.....
CONFIRM THESE DRAWINGS ACCORD WITH OUR REQUIREMENTS AND AUTHORISE THEIR USE FOR NEXT STAGE PURPOSES.

SIGNED..... DATE.....
SIGNED..... DATE.....

SHEET CONTENT:

PLAN - GROUND FLOOR

HOUSE TYPE:
HAMPTON 490

MIN LOT WIDTH:
14M

PROPERTY ADDRESS:
**188 MONCRIEFF CRESCENT
WANDANA HEIGHTS**

CLIENT:
SANDEEP & IMMACOLATA BANSAL

NORTH:

FAÇADE:

SCALE: As indicated

DATE: 20.12.22

SHEET NUMBER:

3.1

JOB NUMBER:

0188MON

JOB ISSUE:

I

REVISIONS

ISSUE	DATE	REVISION DESCRIPTION	INITIALS
A	10.03.20	MASTER ISSUED	MP
B	9.11.21	AMEDED CAS. LIV. BULKHEAD TO LIGHT WEIGHT	MP
C	07.11.22	TENDER DRAWINGS, IDU & COLOUR DOC ADDED	CM
D	09.11.22	COLOUR CHECK ADDED	CM
E	10.11.22	ENERGY ADDED	CM
F	17.11.22	DA RFI	BL
G	30.11.22	ENG. ADDED, CONTRACT DRAWINGS ISSUED	BL
H	20.12.22	B.S RFI & CONTRACT QUOTE AMENDMENT	BL
I	21.12.22	AMEDED ENRGY ADDED	BL

NOTES

- ALL DIMENSIONS ON PLAN ARE NOMINAL & MAY VARY TO ACTUAL SIZES
- CARPENTERS TO ALLOW 45MM DOOR STUD AT WALL JUNCTIONS
- PROVIDE LOCKS TO ALL OPENABLE WINDOWS & EXTERNAL SLIDING DOORS (KEYED ALIKE)
- MAN HOLE LOCATION MAY BE CHANGED DUE TO TRUSS LAYOUT.
- WINDOW AND DOOR FRAME SIZES ARE NOMINAL AND MAY VARY WITH LONG ISLAND HOMES APPROVED SUPPLIERS.
- ALL WATER CLOSETS TO HAVE REMOVABLE HINGES TO THE DOORS IF THERE IS LESS THAN 1.2m CLEARANCE BETWEEN THE CLOSET PAN & THE DOORWAY.
- WINDOW SIZES ARE INDICATIVE ONLY, ACTUAL WINDOW SIZES TO BE DETERMINED BY VARIOUS WINDOW MANUFACTURERS, WITH 100MM ALLOWANCE OF PLAN SPECIFIED SIZES.

VENTING TO EXHAUST FANS & RANGEHOODS


- EXHAUST FANS TO DISCHARGE DIRECTLY TO OUTSIDE AIR VIA DUCTS

LEGEND

- GAS METER
- METER BOX
- CAPPED GAS
- HOT WATER SYSTEM

SITE SPECIFIC NOTES

- ALL DOOR HEIGHTS TO BE 2040 mm(H) INCLUDING GARAGE ACCESS DOOR UNLESS OTHERWISE NOTED.
- PROVIDE 67 x 18mm PENCIL ROUND ARCHITRAVES AND SKIRTING BOARDS TO ENS 1.
- PROVIDE 67 x 12mm PENCIL ROUND ARCHITRAVES AND SKIRTING BOARDS TO THE REST OF THE HOUSE.
- PROVIDE SQUARE SET CORNICE TO ENS 1.
- PROVIDE 75mm SCOTIA COVE CORNICE.
- PROVIDE FLYSCREENS TO ALL OPENABLE WINDOWS.
- PROVIDE 1NO. PRIVACY LOCKS TO PDR DOOR.
- PROVIDE 2NO. 40KG NOGGIN TO BATTEN FITTING TO ENTRANCE AND VOID.

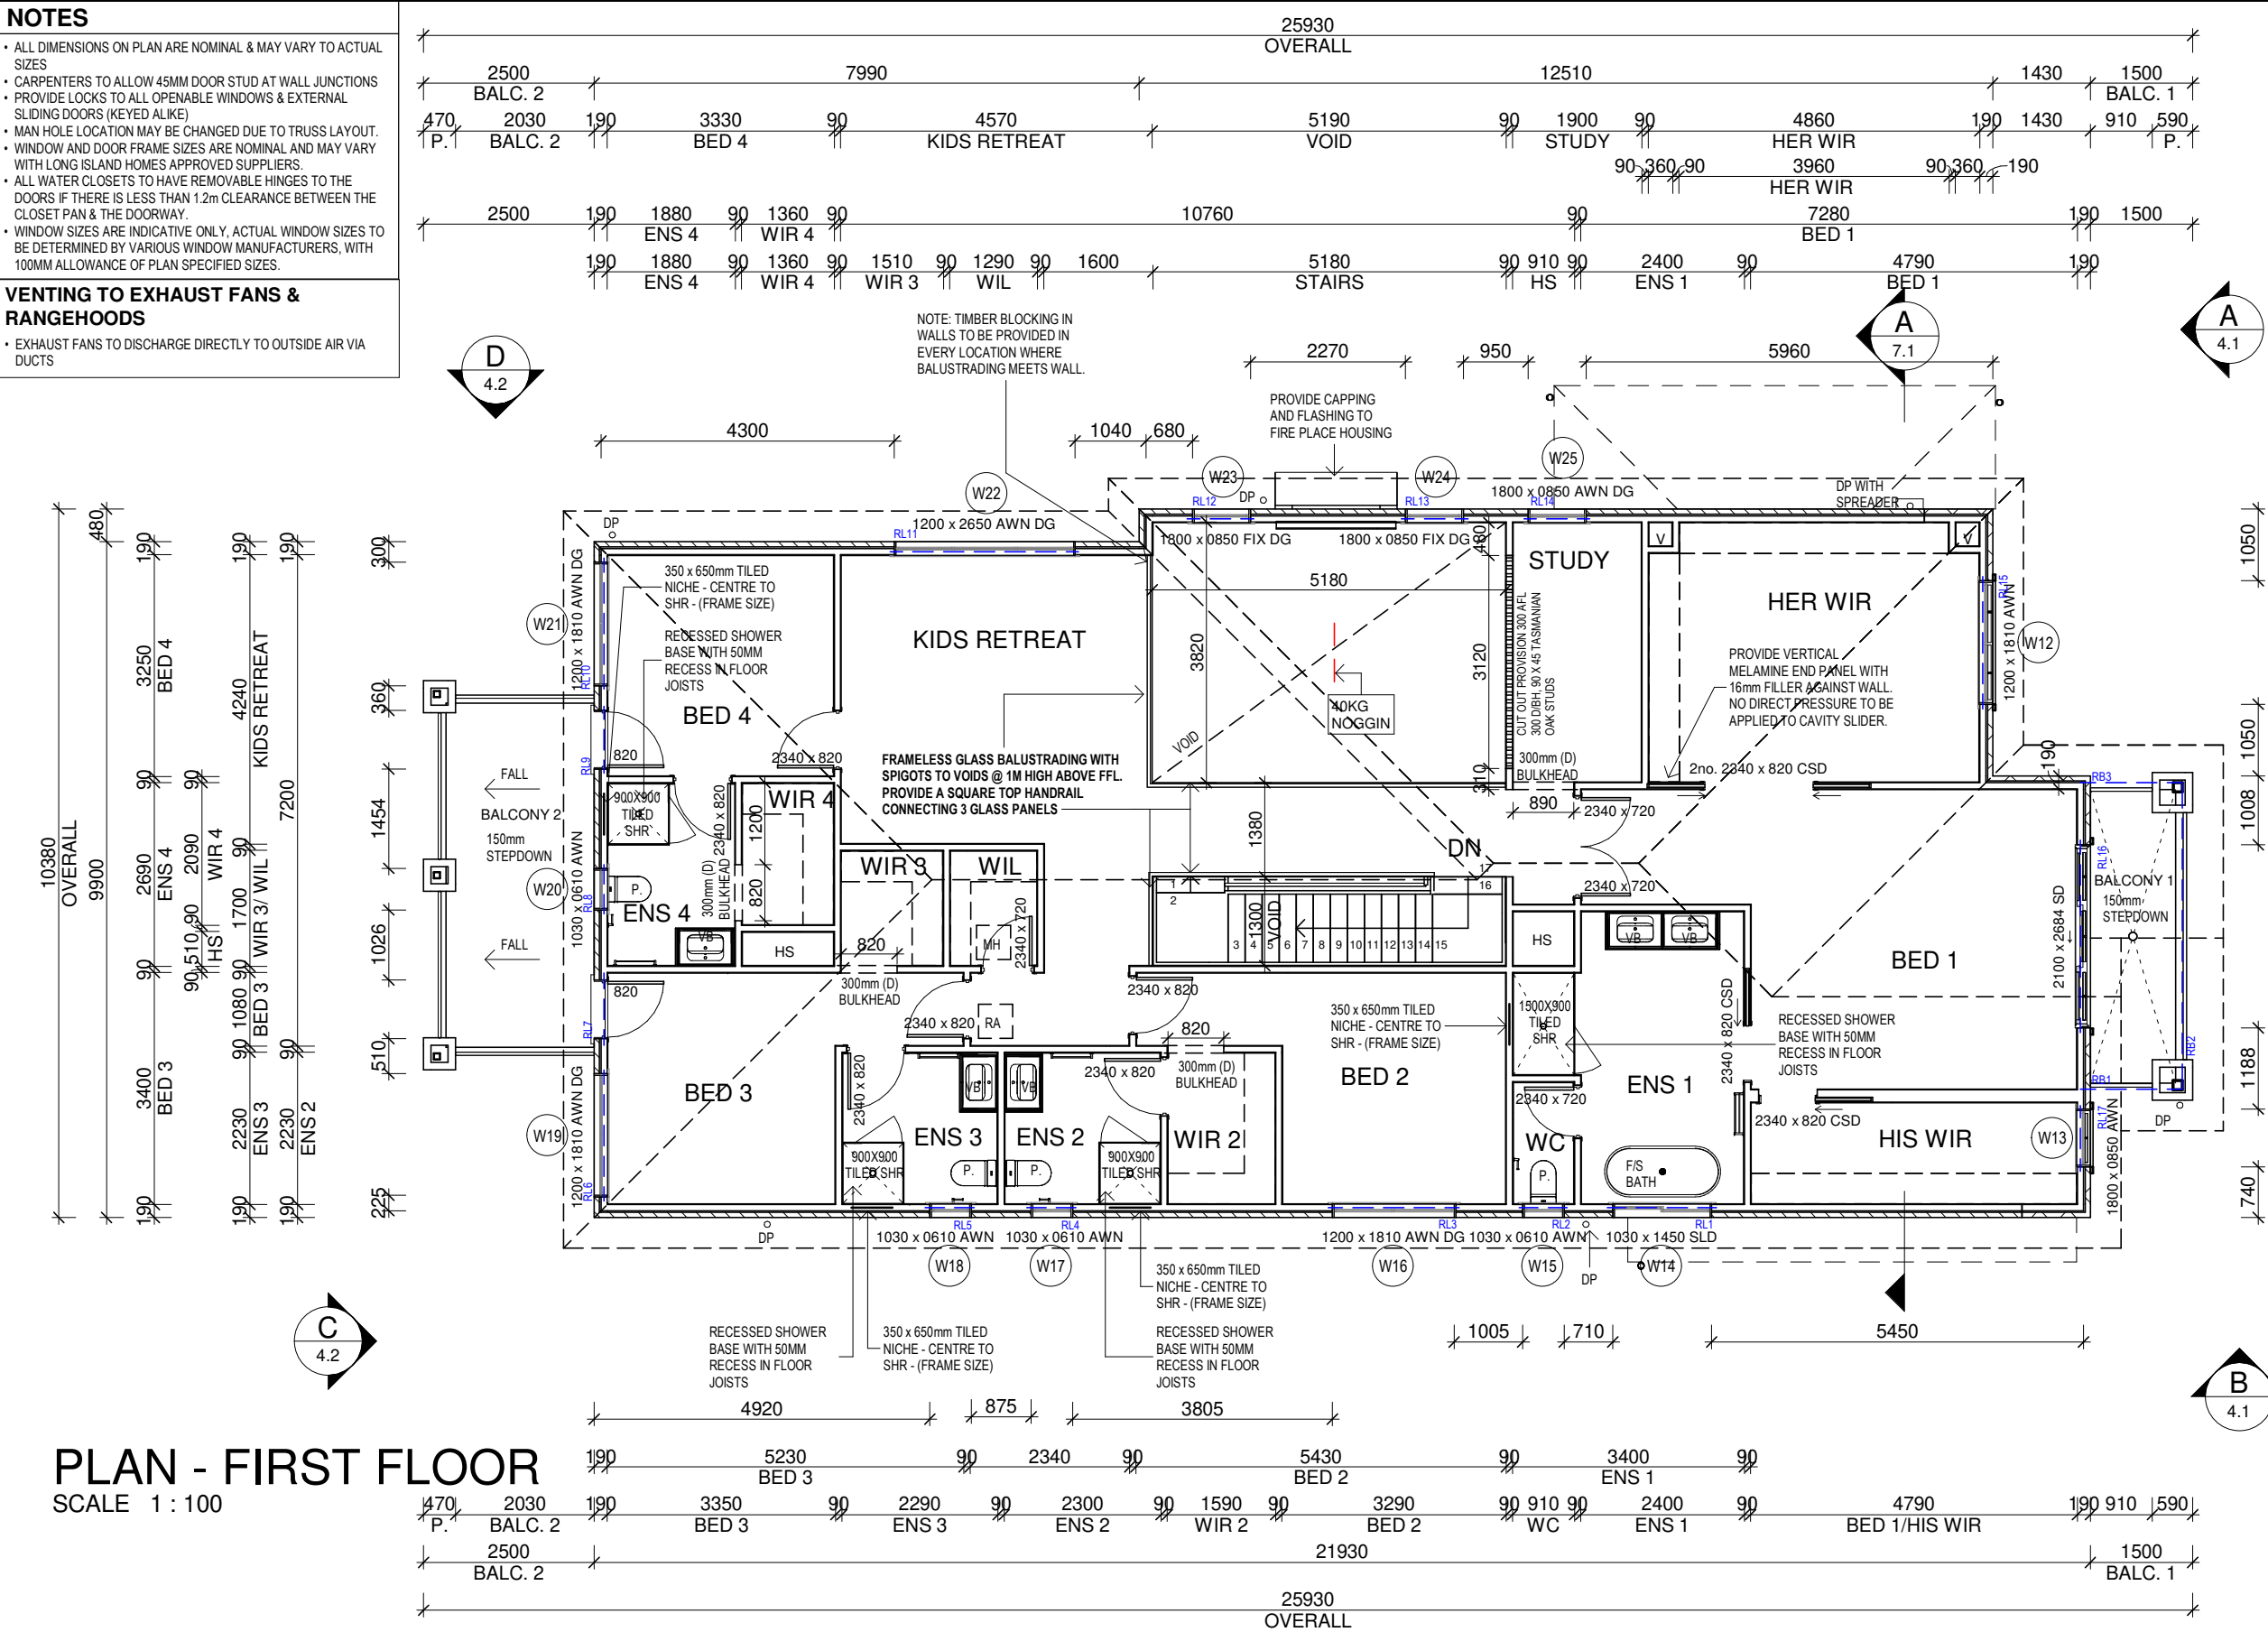

PLAN - FIRST FLOOR
SCALE 1 : 100

HAMPTON 490 - AREAS

NAME	AREA (sqm)	SQR
FIRST FLOOR	218.21 m ²	23.49
GROUND FLOOR	175.89 m ²	18.93
GARAGE	37.24 m ²	4.01
CAS.LIV.	35.09 m ²	3.78
BALC. 2	14.25 m ²	1.53
PORCH	10.46 m ²	1.13
BALC. 1	7.13 m ²	0.77
Total	498.26 m ²	53.63



ISLANDER

Long Island Homes Pty. Ltd.
PO BOX 6269
Point Cook, Vic 3030
p. 61 3 9369 6486 (1800 604 011)
f. 61 3 9369 0994
email: admin@longislandhomes.com.au
www.longislandhomes.com.au

© Copyright
THIS DESIGN & DRAWING SHALL REMAIN THE INTELLECTUAL PROPERTY OF LONG ISLAND HOMES PTY. LTD. AND SHALL NOT BE COPIED IN WHOLE OR PART WITHOUT WRITTEN CONSENT FROM LONG ISLAND HOMES PTY LTD.
DB NUMBER: CDB - U 58094

GENERAL NOTES:

- THE CONTRACTOR IS RESPONSIBLE FOR SETTING OUT AND CHECKING ALL LEVELS AND DIMENSIONS ON SITE PRIOR TO COMMENCING ANY SITE WORKS.
- FIGURED DIMENSIONS ARE TO TAKE PREFERENCE OVER SCALE
- DIMENSIONS TO STRUCTURAL TIMBERS & FACE OF BRICKS EXCLUDING BATTENS, PLASTERBOARD ETC.
- ALL DIMENSIONS ON PLAN ARE NOMINAL & MAY VARY TO ACTUAL SIZE
- PROVIDE LOCKS TO ALL OPENABLE WINDOWS & EXTERNAL SLIDING DOORS (KEYED ALIKE).
- MAN HOLE LOCATION MAY BE CHANGED DUE TO TRUSS LAYOUT.
- WINDOW AND DOOR FRAME SIZES ARE NOMINAL AND MAY VARY WITH LONG ISLAND HOMES APPROVED SUPPLIERS.

CLIENT

I / WE.....

CONFIRM THESE DRAWINGS ACCORD WITH OUR REQUIREMENTS AND AUTHORISE THEIR USE FOR NEXT STAGE PURPOSES.

SIGNED..... DATE.....

SIGNED..... DATE.....

SHEET CONTENT:

PLAN - FIRST FLOOR

HOUSE TYPE:
HAMPTON 490

MIN LOT WIDTH:
14M

PROPERTY ADDRESS:
188 MONCRIEFF CRESCENT
WANDANA HEIGHTS

CLIENT:

SANDEEP & IMMACOLATA BANSAL

NORTH:

FAÇADE:

SCALE: As indicated

DATE: 20.12.22

SHEET NUMBER:

3.2

JOB NUMBER:

0188MON

JOB ISSUE:

I

REVISIONS

ISSUE	DATE	REVISION DESCRIPTION	INITIALS
A	10.03.20	MASTER ISSUED	MP
B	9.11.21	AMEDED GAS. LIV. BULKHEAD TO LIGHT WEIGHT	MP
C	07.11.22	TENDER DRAWINGS, IDU & COLOUR DOC ADDED	CM
D	09.11.22	COLOUR CHECK ADDED	CM
E	10.11.22	ENERGY ADDED	CM
F	17.11.22	DA RFI	BL
G	30.11.22	ENG. ADDED, CONTRACT DRAWINGS ISSUED	BL
H	20.12.22	B.S RFI & CONTRACT QUOTE AMENDMENT	BL
I	21.12.22	AMEDED ENEGRY ADDED	BL


BRICKY'S NOTE

- ARTICULATION JOINTS TO ALL INTERNAL CORNERS.
- PERPS AND BEDS TO BE INSTALLED STRICTLY TO AS3700.
- USE INFILLS BESIDE WINDOWS AND DOORS IF NECESSARY.
- CUT BRICKS IF NECESSARY.
- DO NOT UNDER ANY CIRCUMSTANCE COMPROMISE PERPS AND BEDS.
- LIFT WINDOWS TIGHT UNDER SIDE OF LINTEL BEFORE LAYING BRICK SILLS.
- ALL FIRST FLOOR BEDROOM WINDOWS WITH OPENING HEIGHT LESS THAN 1700mm TO BE RESTRICTED TO 125mm OPENING

NOTE: BACK FILL

- SITE TO BE BACK FILLED TO REBATE HEIGHT & FALL AWAY FROM DWELLING.

OBSCURE GLAZING

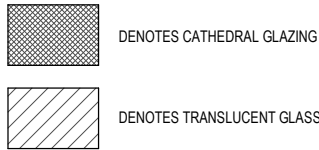

ROOF SOLAR ABSORBANCE


- ALL ROOF (COLORBOND ROOF)
- COLOR: SOUTHERLY - LIGHT 0.4

VENTING TO EXHAUST FANS & RANGEHOODS

- EXHAUST FANS TO DISCHARGE DIRECTLY TO OUTSIDE AIR VIA DUCTS

WINDOW SCHEDULE


MARK	TYPE	HEIGHT	WIDTH	OBSOLETE GLAZING	HEAD HEIGHT	SILL HEIGHT
W1	1800 x 0850 AWN DG	1800	850	No	2086	286
W2	1800 x 0850 AWN DG	1800	850	No	2086	286
W3	1030 x 0610 AWN	1030	610	No	2086	1056
W4	1800 x 1810 AWN DG	1800	1810	No	2086	286
W5	0600 x 2170 FIX (PR)(NBR)	600	2170	No	1510	910
W6	0600 x 1450 FIX	600	1450	No	1570	970
W7	1210 x 1810 SLD	1210	1810	No	2180	970
W8	1800 x 1450 AWN DG	1800	1450	No	2086	286
W9	1800 x 2650 AWN DG	1800	2650	No	2086	286
W10	1800 x 0850 AWN DG	1800	850	No	2086	286
W11	1800 x 0850 AWN DG	1800	850	No	2086	286
W12	1200 x 1810 AWN	1200	1810	No	2100	900
W13	1800 x 0850 AWN	1800	850	No	2100	300
W14	1030 x 1450 SLD	1030	1450	No	2175	1145
W15	1030 x 0610 AWN	1030	610	No	2175	1145
W16	1200 x 1810 AWN DG	1200	1810	No	2175	975
W17	1030 x 0610 AWN	1030	610	No	2175	1145
W18	1030 x 0610 AWN	1030	610	No	2175	1145
W19	1200 x 1810 AWN DG	1200	1810	No	2175	975
W20	1030 x 0610 AWN	1030	610	No	2175	1145
W21	1200 x 1810 AWN DG	1200	1810	No	2175	975
W22	1200 x 2650 AWN DG	1200	2650	No	2175	975
W23	1800 x 0850 FIX DG	1800	850	No	2175	375
W24	1800 x 0850 FIX DG	1800	850	No	2175	375
W25	1800 x 0850 AWN DG	1800	850	No	2175	375

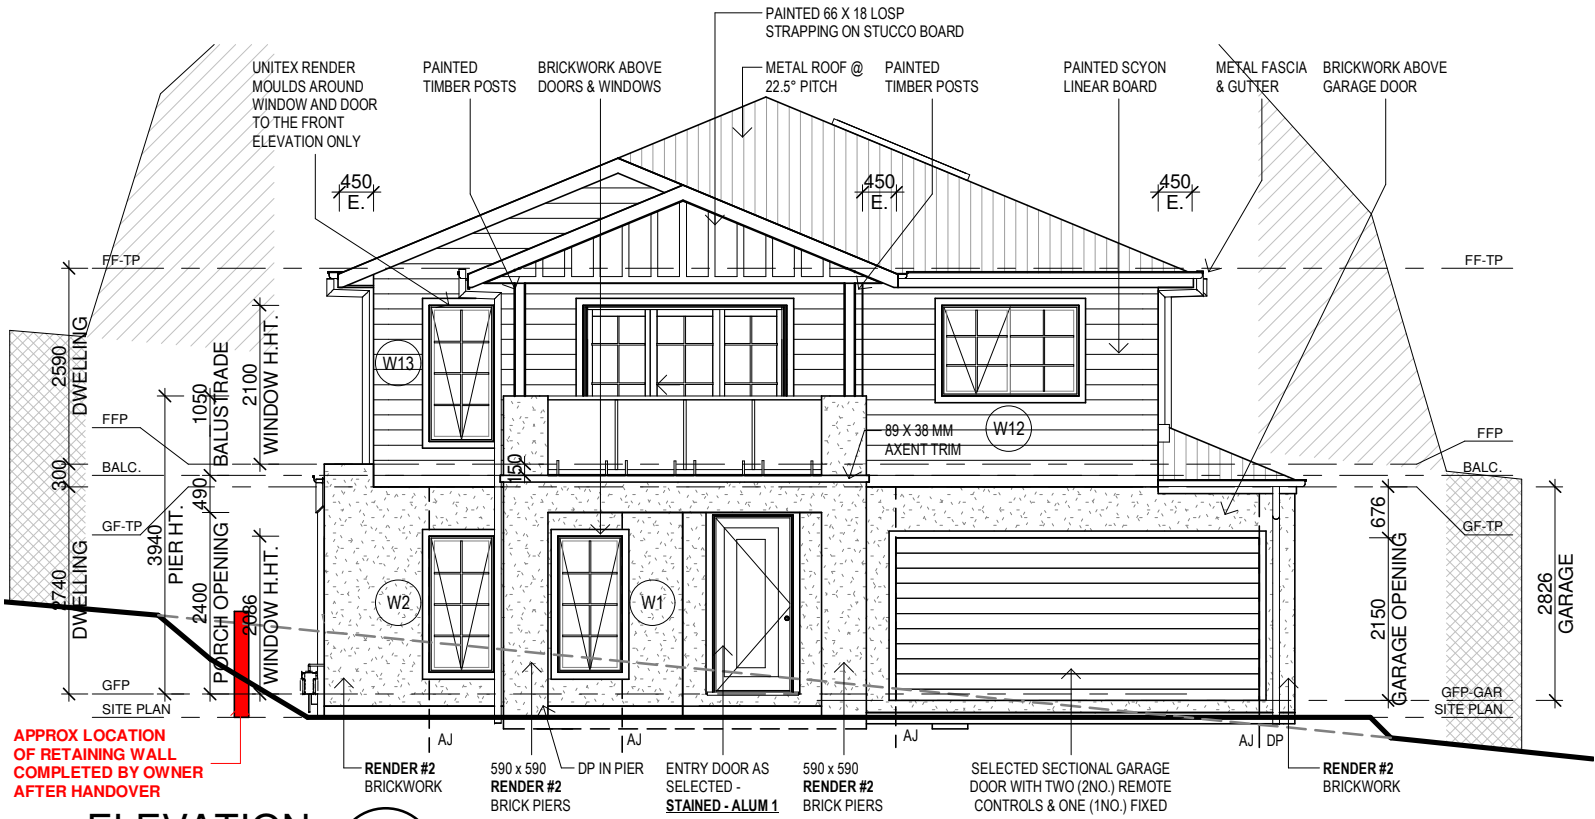

ELEVATION

SCALE 1 : 100

A
3.1

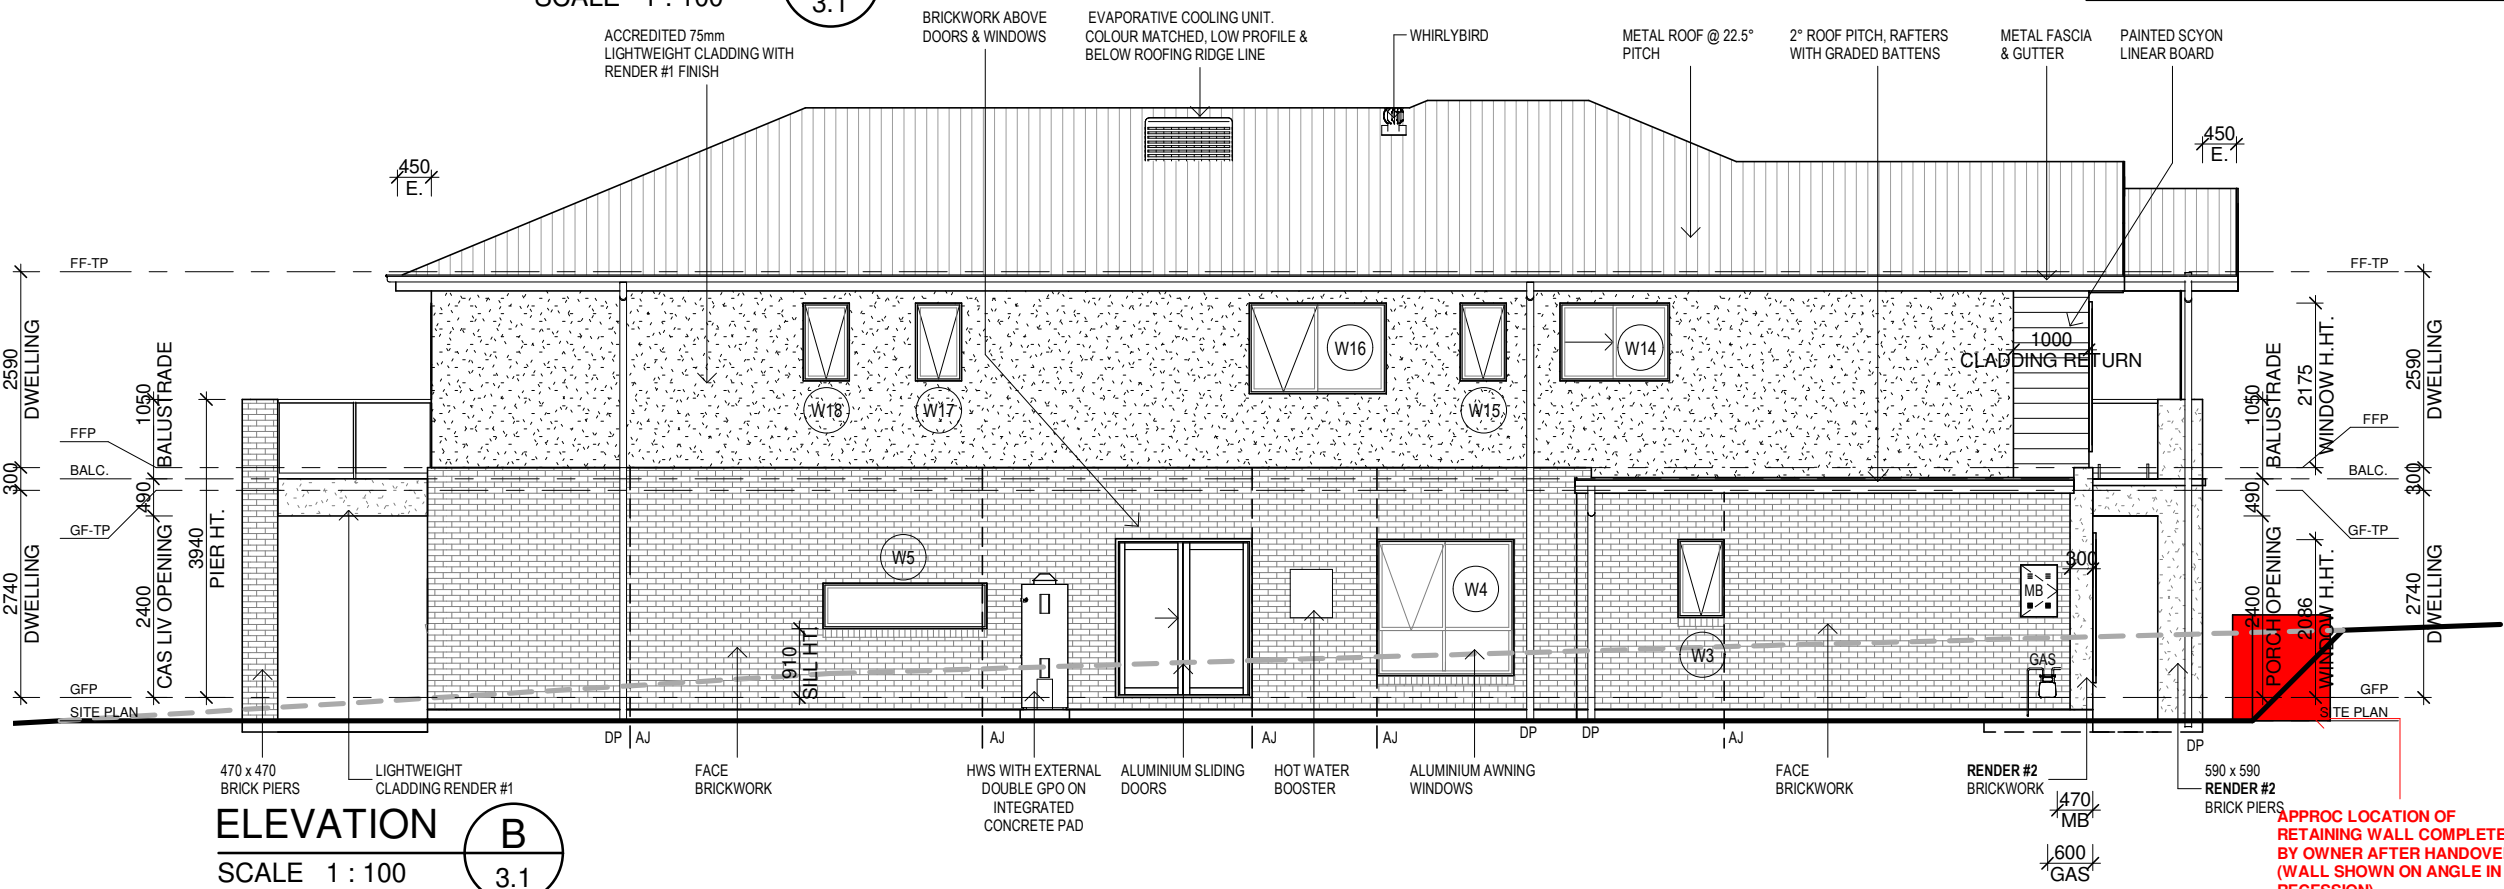

ELEVATION

SCALE 1 : 100

B
3.1

EXTERNAL WALL SCHEDULE

TYPE	AREA
Brick Double - 230mm - Render #2	7.02 m²
Brick Single - 110mm	27.12 m²
Brick Single - 110mm - Render #1	16.32 m²
Brick Veneer - 240mm	139.68 m²
Brick Veneer - 240mm - Render #1	2.79 m²
Brick Veneer - 240mm - Render #2	119.40 m²



ISLANDER

Long Island Homes Pty. Ltd.
PO BOX 6269
Point Cook, Vic 3030
p. 61 3 9369 6486 (1800 604 011)
f. 61 3 9369 0994
email: admin@longislandhomes.com.au
www.longislandhomes.com.au

© Copyright
THIS DESIGN & DRAWING SHALL REMAIN THE INTELLECTUAL PROPERTY OF LONG ISLAND HOMES PTY. LTD. AND SHALL NOT BE COPIED IN WHOLE OR PART WITHOUT WRITTEN CONSENT FROM LONG ISLAND HOMES PTY LTD.
DB NUMBER: CDB - U 58094

GENERAL NOTES:

- THE CONTRACTOR IS RESPONSIBLE FOR SETTING OUT AND CHECKING ALL LEVELS AND DIMENSIONS ON SITE PRIOR TO COMMENCING ANY SITE WORKS.
- FIGURED DIMENSIONS ARE TO TAKE PREFERENCE OVER SCALE
- DIMENSIONS TO STRUCTURAL TIMBERS & FACE OF BRICKS EXCLUDING BATTENS, PLASTERBOARD ETC.
- ALL DIMENSIONS ON PLAN ARE NOMINAL & MAY VARY TO ACTUAL SIZE
- PROVIDE LOCKS TO ALL OPENABLE WINDOWS & EXTERNAL SLIDING DOORS (KEYED ALIKE).
- MAN HOLE LOCATION MAY BE CHANGED DUE TO TRUSS LAYOUT.
- WINDOW AND DOOR FRAME SIZES ARE NOMINAL AND MAY VARY WITH LONG ISLAND HOMES APPROVED SUPPLIERS.

CLIENT

I / WE.....
CONFIRM THESE DRAWINGS ACCORD WITH OUR REQUIREMENTS AND AUTHORISE THEIR USE FOR NEXT STAGE PURPOSES.

SIGNED..... DATE.....
SIGNED..... DATE.....

SHEET CONTENT:

ELEVATIONS A & B

HOUSE TYPE:
HAMPTON 490

MIN LOT WIDTH:
14M

PROPERTY ADDRESS:
188 MONCRIEFF CRESCENT
WANDANA HEIGHTS

CLIENT:
SANDEEP & IMMACOLATA BANSAL

NORTH:

SCALE: As indicated

ISSUE	DATE	REVISION DESCRIPTION	INITIALS
A	10.03.20	MASTER ISSUED	MP
B	9.11.21	AMEDED GAS. LIV. BULKHEAD TO LIGHT WEIGHT	MP
C	07.11.22	TENDER DRAWINGS, IDU & COLOUR DOC ADDED	CM
D	09.11.22	COLOUR CHECK ADDED	CM
E	10.11.22	ENERGY ADDED	CM
F	17.11.22	DA RFI	BL
G	30.11.22	ENG. ADDED, CONTRACT DRAWINGS ISSUED	BL
H	20.12.22	B.S RFI & CONTRACT QUOTE AMENDMENT	BL
I	21.12.22	AMEDED ENEGRY ADDED	BL

- ARTICULATION JOINTS TO ALL INTERNAL CORNERS.

- PERPS AND BEDS TO BE INSTALLED STRICTLY TO AS3700.
- USE INFILLS BESIDE WINDOWS AND DOORS IF NECESSARY.
- CUT BRICKS IF NECESSARY.
- DO NOT UNDER ANY CIRCUMSTANCE COMPROMISE PERPS AND BEDS.
- LIFT WINDOWS TIGHT UNDER SIDE OF LINTEL BEFORE LAYING BRICK SILLS.
- ALL FIRST FLOOR BEDROOM WINDOWS WITH OPENING HEIGHT LESS THAN 1700mm TO BE RESTRICTED TO 125mm OPENING


- SITE TO BE BACK FILLED TO REBATE HEIGHT & FALL AWAY FROM DWELLING.

 DENOTES CATHEDRAL GLAZING


 DENOTES TRANSLUCENT GLASS

ALL ROOF (COLORBOND ROOF)
• COLOUR: SOUTHERLY - LIGHT 0.4

- EXHAUST FANS TO DISCHARGE DIRECTLY TO OUTSIDE AIR VIA DUCTS

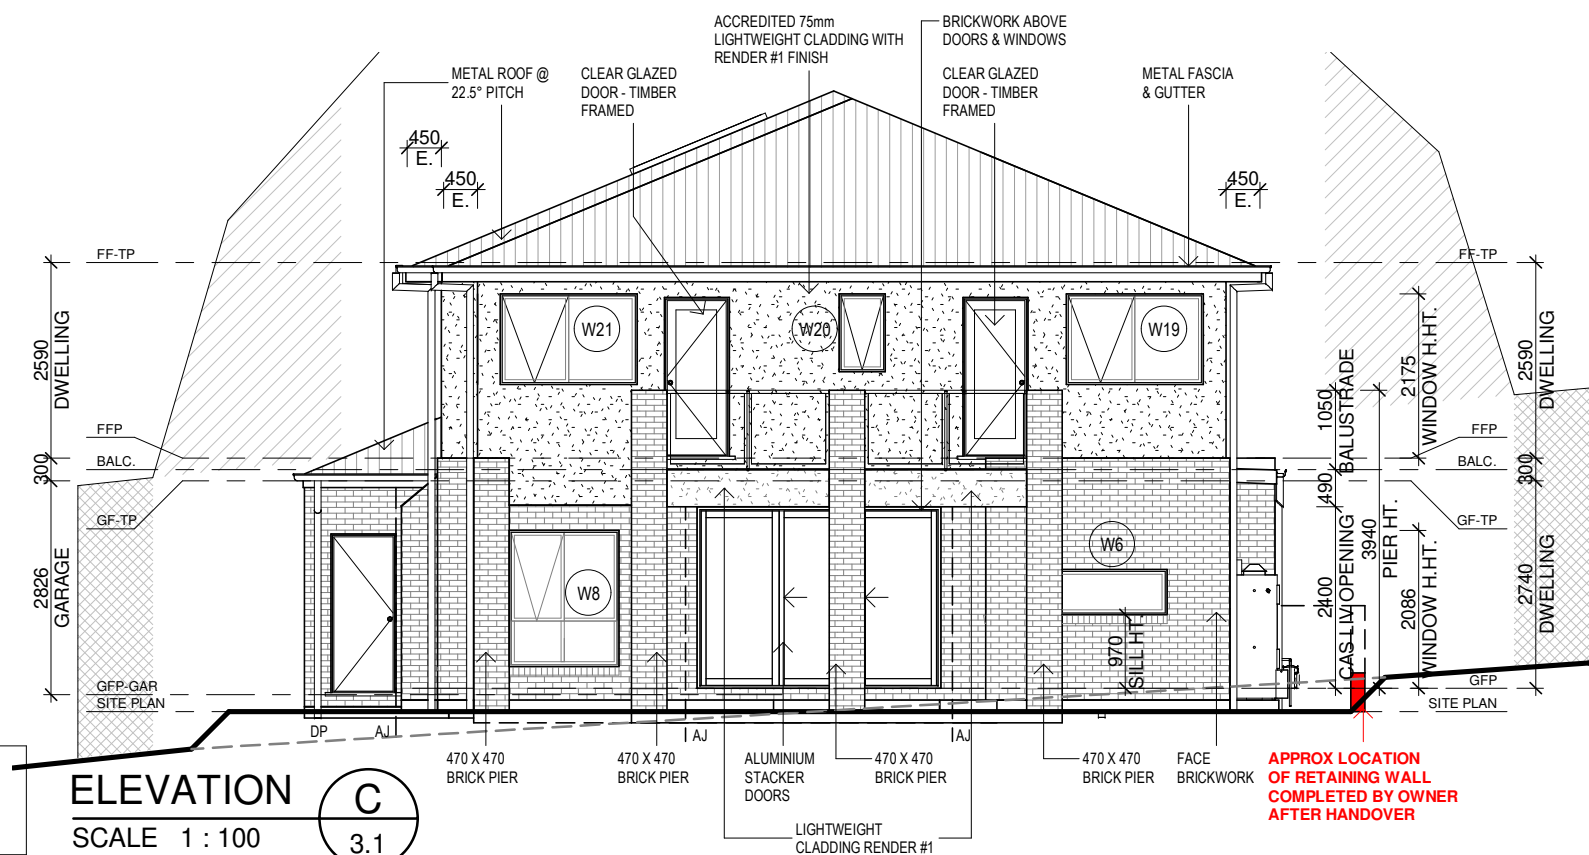

WINDOW SCHEDULE						
MARK	TYPE	HEIGHT	WIDTH	OBSOLETE GLAZING	HEAD HEIGHT	SILL HEIGHT
W1	1800 x 0850 AWN DG	1800	850	No	2086	286
W2	1800 x 0850 AWN DG	1800	850	No	2086	286
W3	1030 x 0610 AWN	1030	610	No	2086	1056
W4	1800 x 1810 AWN DG	1800	1810	No	2086	286
W5	0600 x 2170 FIX (PR)(NBR)	600	2170	No	1510	910
W6	0600 x 1450 FIX	600	1450	No	1570	970
W7	1210 x 1810 SLD	1210	1810	No	2180	970
W8	1800 x 1450 AWN DG	1800	1450	No	2086	286
W9	1800 x 2650 AWN DG	1800	2650	No	2086	286
W10	1800 x 0850 AWN DG	1800	850	No	2086	286
W11	1800 x 0850 AWN DG	1800	850	No	2086	286
W12	1200 x 1810 AWN	1200	1810	No	2100	900
W13	1800 x 0850 AWN	1800	850	No	2100	300
W14	1030 x 1450 SLD	1030	1450	No	2175	1145
W15	1030 x 0610 AWN	1030	610	No	2175	1145
W16	1200 x 1810 AWN DG	1200	1810	No	2175	975
W17	1030 x 0610 AWN	1030	610	No	2175	1145
W18	1030 x 0610 AWN	1030	610	No	2175	1145
W19	1200 x 1810 AWN DG	1200	1810	No	2175	975
W20	1030 x 0610 AWN	1030	610	No	2175	1145
W21	1200 x 1810 AWN DG	1200	1810	No	2175	975
W22	1200 x 2650 AWN DG	1200	2650	No	2175	975
W23	1800 x 0850 FIX DG	1800	850	No	2175	375
W24	1800 x 0850 FIX DG	1800	850	No	2175	375
W25	1800 x 0850 AWN DG	1800	850	No	2175	375

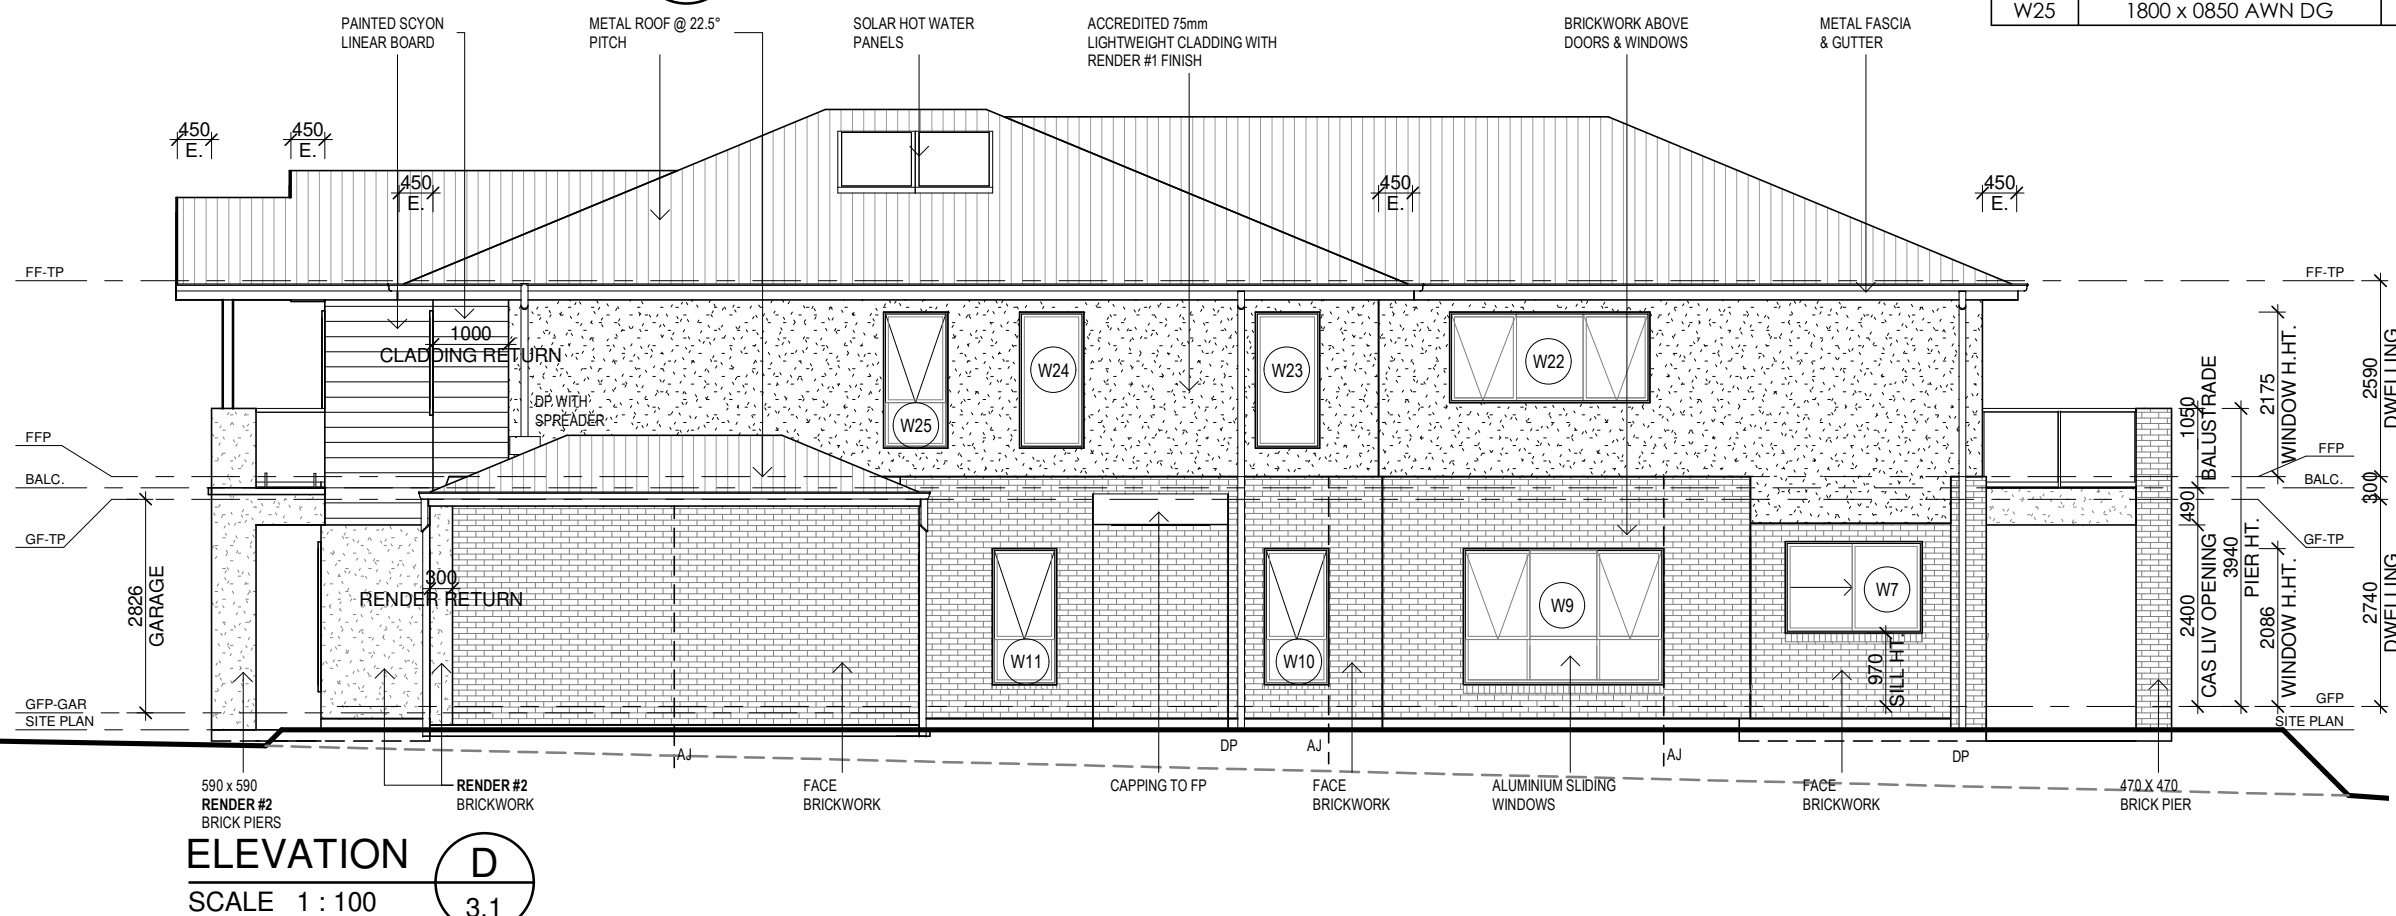

EXTERNAL WALL SCHEDULE	
TYPE	AREA
Brick Double - 230mm - Render #2	7.02 m ²
Brick Single - 110mm	27.12 m ²
Brick Single - 110mm - Render #1	16.32 m ²
Brick Veneer - 240mm	139.68 m ²
Brick Veneer - 240mm - Render #1	2.79 m ²
Brick Veneer - 240mm - Render #2	1.00 m ²



ISLANDER

Long Island Homes Pty. Ltd.
PO BOX 6269
Point Cook, Vic 3030
p. 61 3 9369 6486 (1800 604 011)
f. 61 3 9369 0994
email: admin@longislandhomes.com.au
www.longislandhomes.com.au

© Copyright
THIS DESIGN & DRAWING SHALL REMAIN THE INTELLECTUAL PROPERTY OF
LONG ISLAND HOMES PTY. LTD. AND SHALL NOT BE COPIED IN WHOLE OR
PART WITHOUT WRITTEN CONSENT FROM LONG ISLAND HOMES PTY LTD.
DB NUMBER: CDB - U 58094

- THE CONTRACTOR IS RESPONSIBLE FOR SETTING OUT AND CHECKING ALL LEVELS AND DIMENSIONS ON SITE PRIOR TO COMMENCING ANY SITE WORKS.
- FIGURED DIMENSIONS ARE TO TAKE PREFERENCE OVER SCALE
- DIMENSIONS TO STRUCTURAL TIMBERS & FACE OF BRICKS EXCLUDING BATTENS, PLASTERBOARD ETC.
- ALL DIMENSIONS ON PLAN ARE NOMINAL & MAY VARY TO ACTUAL SIZE
- PROVIDE LOCKS TO ALL OPENABLE WINDOWS & EXTERNAL SLIDING DOORS (KEYED ALIKE).
- MAN HOLE LOCATION MAY BE CHANGED DUE TO TRUSS LAYOUT.
- WINDOW AND DOOR FRAME SIZES ARE NOMINAL AND MAY VARY WITH LONG ISLAND HOMES APPROVED SUPPLIERS.

I / WE.....

CONFIRM THESE DRAWINGS ACCORD WITH OUR
REQUIREMENTS AND AUTHORISE THEIR USE FOR
NEXT STAGE PURPOSES.

SIGNED..... DATE.....

SIGNED..... DATE.....

	SHEET CONTENT:
--	----------------

ELEVATIONS C & D

HOUSE TYPE:
HAMPTON 490

MIN LOT WIDTH:	14M
----------------	-----

PROPERTY ADDRESS:

188 MONCRIEFF CRESCENT
WANDANA HEIGHTS

CLIENT:	
---------	--

SANDEEP & IMMACOLATA BANSAL

NORTH:

Brick Veneer - 240mm	SHEET NUMBER: #30	JOB NUMBER: 19-40 m²
----------------------	-------------------	----------------------

0188MON		
---------	--	--

SCALE: As indicated 4 2

4.2

JOB ISSUE:

DATE: 20.12.22		
----------------	--	--

DATE	REVISION DESCRIPTION	INITIAL
------	----------------------	---------

DATE	REVISION DESCRIPTION	INITIALS
03.20	MASTER ISSUED	MP

1.21	AMEDED CAS. LIV. BULKHEAD TO LIGHT WEIGHT	MP
1.22	TENDER DRAWINGS. IDU & COLOUR DOC ADDED	CM

11.22	TENDER DRAWINGS, IDU & COLOUR DOC ADDED	CM
11.22	COLOUR CHECK ADDED	CM

11.22	ENERGY ADDED	CM
11.23	PAUSE	PL

11.22	DA RFI	BL
11.22	ENG. ADDED, CONTRACT DRAWINGS ISSUED	BL

12.22	B.S RFI & CONTRACT QUOTE AMENDMENT	BL
-------	------------------------------------	----

NCC PART 3.12.5.5 ARTIFICIAL LIGHTING LAMPPOWER DENSITY SHALL NOT EXCEED:

- 5W/sq.m FOR CLASS 1 BUILDING
- 4W/sq.m FOR VERANDAH, ALFRESCO, PORCH OR BALCONY
- 3W/sq.m FOR CLASS 10a BUILDING PERIMETER LIGHTING TO BE CONTROLLED BY A SENSOR OR HAVE A MAXIMUM OF 40 LUMENS PER WATT.

SMOKE DETECTORS TO BE INTERCONNECTED AS PER NCC 2019

ELECTRICAL NOTES

- PROVIDE ENERGY SAVING LIGHT BULBS TO BATTEN LIGHTING THROUGHOUT.
- PROVIDE WHITE COVER PLATES TO SWITCHES.
- PROVIDE LINKED SMOKE DETECTORS, HARDWIRED WITH BATTERY BACKUP.

- 30 x LED DOWNLIGHTS
- 10 x ADDITIONAL DOUBLE POWER POINTS
- 2 x WALL MOUNTED COACH LIGHTS TO PORCH
- 2 x SENSORS
- 1 x DIMMER TO THEATRE

PROVIDE FIBRE OPTIC IN ACCORDANCE WITH ESTATE REQUIREMENTS. THIS INVOLVES DISTRIBUTION OF DATA, PHONE & TV FROM ONE CENTRE LOCATION.

- 2 X DATA
 - 0 X PHONE
 - 2 X TELEVISION
- CONDUIT AND DRAW WIRE FROM TELECOMMUNICATIONS SUPPLY PIT TO THE TERMINATION POINT.
- NOTES: IT IS THE OWNER'S RESPONSIBILITY TO ARRANGE CONNECTION OF THE FOLLOWING SERVICES WITH THE APPROPRIATE PROVIDERS AFTER HANDOVER. EXCLUDES TV ANTENNA.

- PROVIDE 4 STAR GAS DUCTED HEATING UNIT WITH 2 ZONES.
- PROVIDE EVAPORATIVE COOLING UNIT UP TO 8 POINTS, INCLUDES MAGI-Q-CONTROLLER CONNECTED INTO THE HEATING UNIT.

ITEM	TOTAL
DGPO	31
DGPO - EXTERNAL	5
DUCT - COOLING	8
DUCT - HEATING	13
EXHAUSTING FAN	5
FLOOD LIGHT - SINGLE	2
LIGHT - BATTEN	23
LIGHT - LED	70
LIGHT - WALL EXTERNAL BATTEN	2
POINT - DATA	2
POINT - TV	2
SGPO	6
SMOKE DETECTOR	6



ALL ELECTRICAL LOCATIONS ARE INDICATIVE ONLY

		FACADE: SCALE: As indicated DATE: 20.12.22		SHEET NUMBER: 5.1		JOB NUMBER: 0188MON JOB ISSUE: I	
DATE	REVISION DESCRIPTION	INITIALS					
10.03.20	MASTER ISSUED	MP					
9.11.21	AMEDED CAS. LIV. BULKHEAD TO LIGHT WEIGHT	MP					
07.11.22	TENDER DRAWINGS, IDU & COLOUR DOC ADDED	CM					
09.11.22	COLOUR CHECK ADDED	CM					
10.11.22	ENERGY ADDED	CM					
17.11.22	DA RFI	BL					
30.11.22	ENG. ADDED, CONTRACT DRAWINGS ISSUED	BL					
20.12.22	B.S RFI & CONTRACT QUOTE AMENDMENT	BL					
21.12.22	AMENDED ENERGY ADDED	BL					

SCALE 1 : 100



THE CONTRACTOR IS RESPONSIBLE FOR SETTING OUT AND CHECKING ALL LEVELS AND DIMENSIONS ON SITE PRIOR TO COMMENCING ANY SITE WORKS.

FIGURED DIMENSIONS ARE TO TAKE PREFERENCE OVER SCALE

DIMENSIONS TO STRUCTURAL TIMBERS & FACE OF BRICKS EXCLUDING BATTENS, PLASTERBOARD ETC.

ALL DIMENSIONS ON PLAN ARE NOMINAL & MAY VARY TO ACTUAL SIZE

PROVIDE LOCKS TO ALL OPENABLE WINDOWS & EXTERNAL SLIDING DOORS (KEYED ALIKE).

MAN HOLE LOCATION MAY BE CHANGED DUE TO TRUSS LAYOUT.

WINDOW AND DOOR FRAME SIZES ARE NOMINAL AND MAY VARY WITH LONG ISLAND HOMES APPROVED SUPPLIERS.

SIGN OFF	I / WE.....
	
	CONFIRM THESE DRAWINGS ACCORD WITH OUR REQUIREMENTS AND AUTHORISE THEIR USE FOR NEXT STAGE PURPOSES.
	SIGNED..... DATE.....
	SIGNED..... DATE.....

SHEET CONTENT:	
ELECTRICAL - GROUND FLOOR	
HOUSE TYPE: HAMPTON 490	MIN LOT WIDTH: 14M
PROPERTY ADDRESS: 188 MONCRIEFF CRESCENT WANDANA HEIGHTS	
CLIENT: SANDEEP & IMMACOLATA BANSAL	

NORTH:			FACADE:		SHEET NUMBER:		JOB NUMBER:	
			SCALE: As indicated		5.1		0188MON	
			DATE: 20.12.22				JOB ISSUE:	
							I	
REVISIONS	ISSUE	DATE	REVISION DESCRIPTION					INITIALS
	A	10.03.20	MASTER ISSUED					MP
	B	9.11.21	AMEDED CAS, LIV, BULKHEAD TO LIGHT WEIGHT					MP
	C	07.11.22	TENDER DRAWINGS, IDU & COLOUR DOC ADDED					CM
	D	09.11.22	COLOUR CHECK ADDED					CM
	E	10.11.22	ENERGY ADDED					CM
	F	17.11.22	DA RFI					BL
	G	30.11.22	ENG. ADDED, CONTRACT DRAWINGS ISSUED					BL
	H	20.12.22	B.S RFI & CONTRACT QUOTE AMENDMENT					BL
		21.12.22	AMFNPDRJUNFGRV, T DDED					BL

NCC PART 3.12.5.5 ARTIFICIAL LIGHTING LAMPPOWER DENSITY SHALL NOT EXCEED:

- 5W/sq.m FOR CLASS 1 BUILDING
- 4W/sq.m FOR VERANDAH, ALFRESCO, PORCH OR BALCONY
- 3W/sq.m FOR CLASS 10a BUILDING PERIMETER LIGHTING TO BE CONTROLLED BY A SENSOR OR HAVE A MAXIMUM OF 40 LUMENS PER WATT.

SMOKE DETECTORS TO BE INTERCONNECTED AS PER NCC 2019

ELECTRICAL NOTES

- PROVIDE ENERGY SAVING LIGHT BULBS TO BATTEN LIGHTING THROUGHOUT.
- PROVIDE WHITE COVER PLATES TO SWITCHES.
- PROVIDE LINKED SMOKE DETECTORS, HARDWIRED WITH BATTERY BACKUP.


- 30 x LED DOWNLIGHTS
- 10 x ADDITIONAL DOUBLE POWER POINTS
- 2 x WALL MOUNTED COACH LIGHTS TO PORCH
- 2 x SENSORS
- 1 x DIMMER TO THEATRE

PROVIDE FIBRE OPTIC IN ACCORDANCE WITH ESTATE REQUIREMENTS. THIS INVOLVES DISTRIBUTION OF DATA, PHONE & TV FROM ONE CENTRE LOCATION.

- CONDUIT AND DRAW WIRE FROM TELECOMMUNICATIONS SUPPLY PIT TO THE TERMINATION POINT.
NOTES: IT IS THE OWNER'S RESPONSIBILITY TO ARRANGE CONNECTION OF THE FOLLOWING SERVICES WITH THE APPROPRIATE PROVIDERS AFTER HANDOVER. EXCLUDES TV ANTENNA.

- PROVIDE 4 STAR GAS DUCTED HEATING UNIT WITH 2 ZONES.
- PROVIDE EVAPORATIVE COOLING UNIT UP TO 8 POINTS, INCLUDES MAGI-Q-CONTROLLER CONNECTED INTO THE HEATING UNIT.

ITEM	TOTAL
DGPO	31
DGPO - EXTERNAL	5
DUCT - COOLING	8
DUCT - HEATING	13
EXHAUSTING FAN	5
FLOOD LIGHT - SINGLE	2
LIGHT - BATTEN	23
LIGHT - LED	70
LIGHT - WALL	2
EXTERNAL BATTEN	
POINT - DATA	2
POINT - TV	2
SGPO	6
SMOKE DETECTOR	6

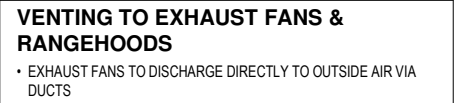

ALL ELECTRICAL LOCATIONS ARE INDICATIVE ONLY

		FACADE:		SHEET NUMBER: 5.2	JOB NUMBER: 0188MON	
		SCALE: As indicated			JOB ISSUE:	
		DATE: 20.12.22			I	
UE	DATE	REVISION DESCRIPTION				INITIALS
	10.03.20	MASTER ISSUED				MP
	9.11.21	AMEDED CAS. LIV. BULKHEAD TO LIGHT WEIGHT				MP
	07.11.22	TENDER DRAWINGS, IDU & COLOUR DOC ADDED				CM
	09.11.22	COLOUR CHECK ADDED				CM
	10.11.22	ENERGY ADDED				CM
	17.11.22	DA RFI				BL
	30.11.22	ENG. ADDED, CONTRACT DRAWINGS ISSUED				BL
	20.12.22	B.S RFI & CONTRACT QUOTE AMENDMENT				BL
	21.12.22	AMENDED ENRGY ADDED				BL

SCALE 1 : 100



© Copyright
THIS DESIGN & DRAWING SHALL REMAIN THE INTELLECTUAL PROPERTY OF
LONG ISLAND HOMES PTY. LTD. AND SHALL NOT BE COPIED IN WHOLE OR
PART WITHOUT WRITTEN CONSENT FROM LONG ISLAND HOMES PTY LTD.
DB NUMBER: CDB - U 58094

- THE CONTRACTOR IS RESPONSIBLE FOR SETTING OUT AND CHECKING ALL LEVELS AND DIMENSIONS ON SITE PRIOR TO COMMENCING ANY SITE WORKS.
- FIGURED DIMENSIONS ARE TO TAKE PREFERENCE OVER SCALE
- DIMENSIONS TO STRUCTURAL TIMBERS & FACE OF BRICKS EXCLUDING BATTENS, PLASTERBOARD ETC.
- ALL DIMENSIONS ON PLAN ARE NOMINAL & MAY VARY TO ACTUAL SIZE
- PROVIDE LOCKS TO ALL OPENABLE WINDOWS & EXTERNAL SLIDING DOORS (KEYED ALIKE).
- MAN HOLE LOCATION MAY BE CHANGED DUE TO TRUSS LAYOUT.
- WINDOW AND DOOR FRAME SIZES ARE NOMINAL AND MAY VARY WITH LONG ISLAND HOMES APPROVED SUPPLIERS.

SIGNED..... DATE.....

CLIENT: **SANDEEP & IMMACOLATA BANSAL**

REVISIONS

ISSUE	DATE	REVISION DESCRIPTION	INITIALS
A	10.03.20	MASTER ISSUED	MP
B	9.11.21	AMEDED CAS, LIV. BULKHEAD TO LIGHT WEIGHT	MP
C	07.11.22	TENDER DRAWINGS, IDU & COLOUR DOC ADDED	CM
D	09.11.22	COLOUR CHECK ADDED	CM
E	10.11.22	ENERGY ADDED	CM
F	17.11.22	DA RFI	BL
G	30.11.22	ENG. ADDED, CONTRACT DRAWINGS ISSUED	BL
H	20.12.22	B.S RFI & CONTRACT QUOTE AMENDMENT	BL
I	21.12.22	AMEDED ENRGY ADDED	BL

21/12/2022 4:21:27 PM J:\LONG ISLAND JOBS\188 Moncrieff Crescent, Wandana Heights\DRAWING\0188MON_REV 1.rvt

FLOOR COVERINGS


-  DENOTES CARPET
-  DENOTES TILES
-  DENOTES NATURAL CONCRETE
-  DENOTES LAMINATE FLOORING
-  DENOTES EXPOSED AGGREGATE
-  DENOTES COLOURED CONCRETE
-  DENOTES STAINED KDHW

NOTES:

- IF FLOOR COVERINGS ARE SUPPLIED BY LONG ISLAND HOMES, THE PATTERNED HATCH SHOWN ON DRAWINGS DOES NOT INDICATE LAYOUT OR DIRECTION OF FINISH.

FLOOR SCHEDULE

TYPE	AREA
Floor Tile - 400 x 400	16.21 m ²
Floor Tile - 600 x 600	140.42 m ²
LAMINATE	174.57 m ²

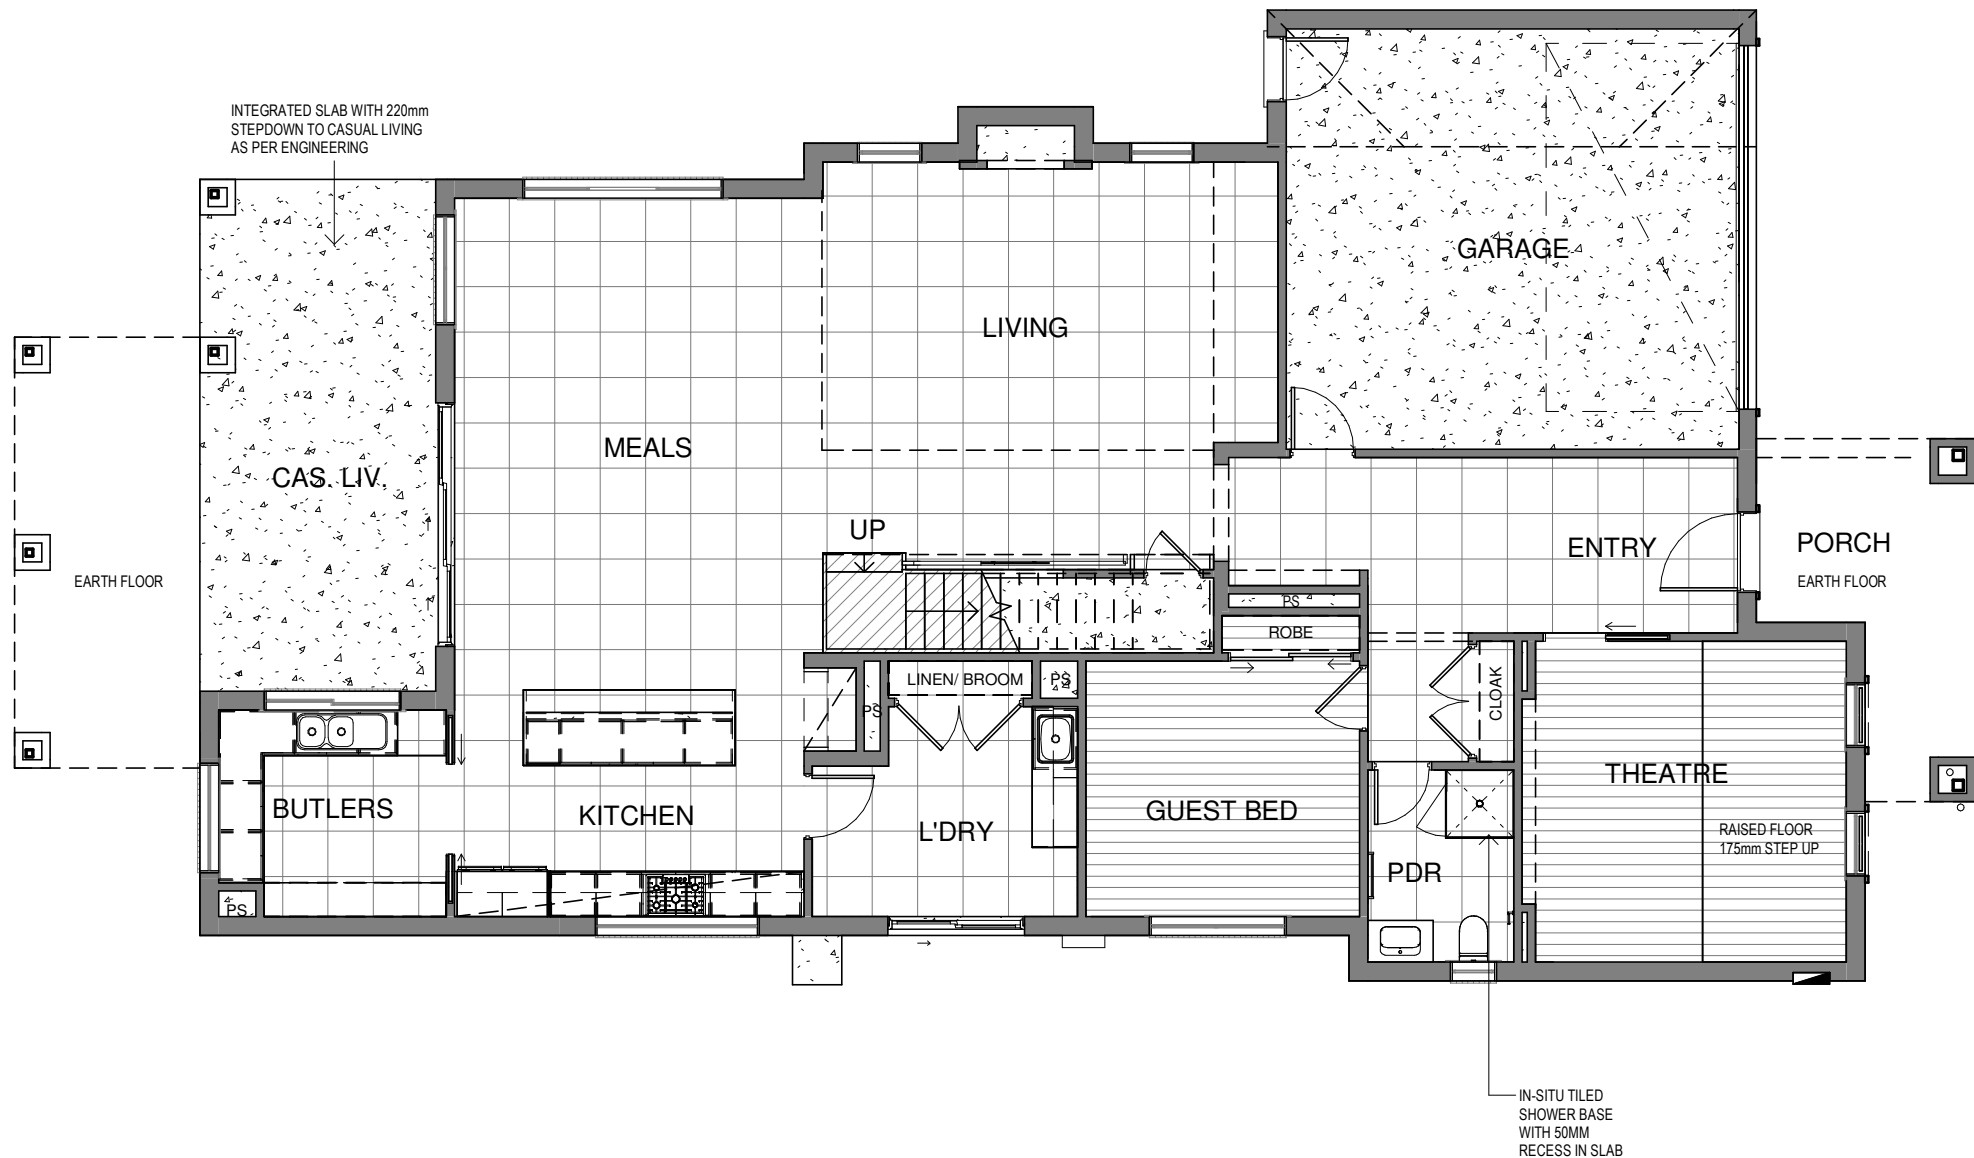

FLOORING - GROUND FLOOR

SCALE 1 : 100



ISLANDER

Long Island Homes Pty. Ltd.
PO BOX 6269
Point Cook, Vic 3030
p. 61 3 9369 6486 (1800 604 011)
f. 61 3 9369 0994
email: admin@longislandhomes.com.au
www.longislandhomes.com.au

© Copyright
THIS DESIGN & DRAWING SHALL REMAIN THE INTELLECTUAL PROPERTY OF
LONG ISLAND HOMES PTY. LTD. AND SHALL NOT BE COPIED IN WHOLE OR
PART WITHOUT WRITTEN CONSENT FROM LONG ISLAND HOMES PTY LTD.
DB NUMBER: CDB - U 58094

GENERAL NOTES:

- THE CONTRACTOR IS RESPONSIBLE FOR SETTING OUT AND CHECKING ALL LEVELS AND DIMENSIONS ON SITE PRIOR TO COMMENCING ANY SITE WORKS.
- FIGURED DIMENSIONS ARE TO TAKE PREFERENCE OVER SCALE
- DIMENSIONS TO STRUCTURAL TIMBERS & FACE OF BRICKS EXCLUDING BATTENS, PLASTERBOARD ETC.
- ALL DIMENSIONS ON PLAN ARE NOMINAL & MAY VARY TO ACTUAL SIZE
- PROVIDE LOCKS TO ALL OPENABLE WINDOWS & EXTERNAL SLIDING DOORS (KEYED ALIKE).
- MAN HOLE LOCATION MAY BE CHANGED DUE TO TRUSS LAYOUT.
- WINDOW AND DOOR FRAME SIZES ARE NOMINAL AND MAY VARY WITH LONG ISLAND HOMES APPROVED SUPPLIERS.

CLIENT

I / WE.....

CONFIRM THESE DRAWINGS ACCORD WITH OUR REQUIREMENTS AND AUTHORISE THEIR USE FOR NEXT STAGE PURPOSES.

SIGNED..... DATE.....

SIGNED..... DATE.....

SHEET CONTENT:

FLOORING - GROUND FLOOR

HOUSE TYPE:
HAMPTON 490

MIN LOT WIDTH:
14M

PROPERTY ADDRESS:
**188 MONCRIEFF CRESCENT
WANDANA HEIGHTS**

CLIENT:
SANDEEP & IMMACOLATA BANSAL

NORTH:

FACADE:

SCALE: 1 : 100

DATE: 20.12.22

SHEET NUMBER:

6.1

JOB NUMBER:

0188MON

JOB ISSUE:

I

ISSUE	DATE	REVISION DESCRIPTION	INITIALS
A	10.03.20	MASTER ISSUED	MP
B	9.11.21	AMEDED CAS. LIV. BULKHEAD TO LIGHT WEIGHT	MP
C	07.11.22	TENDER DRAWINGS, IDU & COLOUR DOC ADDED	CM
D	09.11.22	COLOUR CHECK ADDED	CM
E	10.11.22	ENERGY ADDED	CM
F	17.11.22	DA RFI	BL
G	30.11.22	ENG. ADDED, CONTRACT DRAWINGS ISSUED	BL
H	20.12.22	B.S RFI & CONTRACT QUOTE AMENDMENT	BL
I	21.12.22	AMEDED ENEGRY ADDED	BL

21/12/2022 4:21:28 PM J:\LONG ISLAND JOBS\188 Moncrieff Crescent, Wandana Heights\DRAWING\0188MON_REV 1.rvt

FLOOR COVERINGS


-  DENOTES CARPET
-  DENOTES TILES
-  DENOTES NATURAL CONCRETE
-  DENOTES LAMINATE FLOORING
-  DENOTES EXPOSED AGGREGATE
-  DENOTES COLOURED CONCRETE
-  DENOTES STAINED KDFW

NOTES:

- IF FLOOR COVERINGS ARE SUPPLIED BY LONG ISLAND HOMES, THE PATTERNED HATCH SHOWN ON DRAWINGS DOES NOT INDICATE LAYOUT OR DIRECTION OF FINISH.

FLOOR SCHEDULE

TYPE	AREA
Floor Tile - 400 x 400	16.21 m ²
Floor Tile - 600 x 600	140.42 m ²
LAMINATE	174.57 m ²

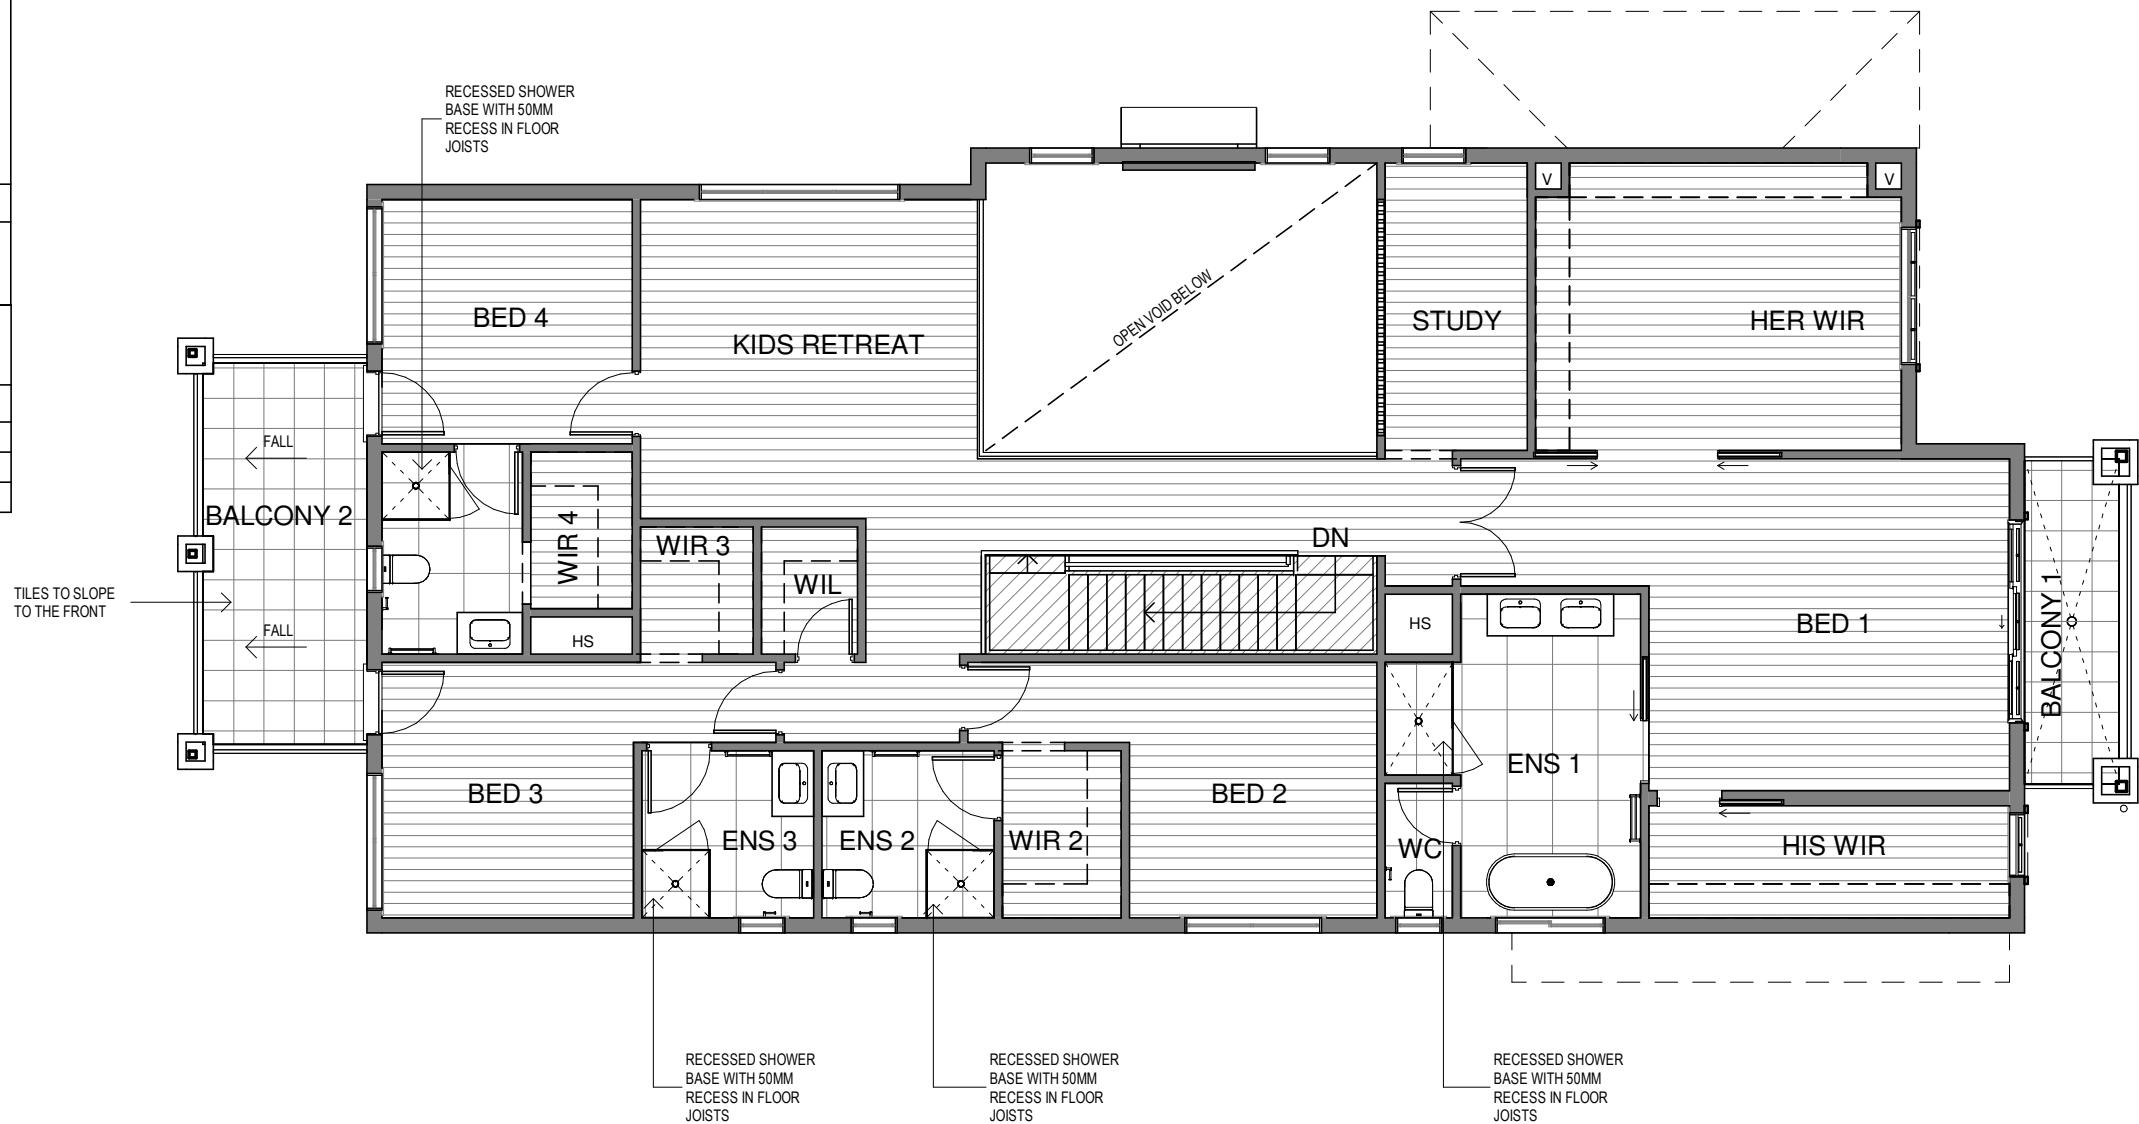

FLOORING - FIRST FLOOR

SCALE 1 : 100



ISLANDER

Long Island Homes Pty. Ltd.
PO BOX 6269
Point Cook, Vic 3030
p. 61 3 9369 6486 (1800 604 011)
f. 61 3 9369 0994
email: admin@longislandhomes.com.au
www.longislandhomes.com.au

© Copyright
THIS DESIGN & DRAWING SHALL REMAIN THE INTELLECTUAL PROPERTY OF
LONG ISLAND HOMES PTY. LTD. AND SHALL NOT BE COPIED IN WHOLE OR
PART WITHOUT WRITTEN CONSENT FROM LONG ISLAND HOMES PTY LTD.
DB NUMBER: CDB - U 58094

GENERAL NOTES:

- THE CONTRACTOR IS RESPONSIBLE FOR SETTING OUT AND CHECKING ALL LEVELS AND DIMENSIONS ON SITE PRIOR TO COMMENCING ANY SITE WORKS.
- FIGURED DIMENSIONS ARE TO TAKE PREFERENCE OVER SCALE
- DIMENSIONS TO STRUCTURAL TIMBERS & FACE OF BRICKS EXCLUDING BATTENS, PLASTERBOARD ETC.
- ALL DIMENSIONS ON PLAN ARE NOMINAL & MAY VARY TO ACTUAL SIZE
- PROVIDE LOCKS TO ALL OPENABLE WINDOWS & EXTERNAL SLIDING DOORS (KEYED ALIKE).
- MAN HOLE LOCATION MAY BE CHANGED DUE TO TRUSS LAYOUT.
- WINDOW AND DOOR FRAME SIZES ARE NOMINAL AND MAY VARY WITH LONG ISLAND HOMES APPROVED SUPPLIERS.

CLIENT

I / WE.....

CONFIRM THESE DRAWINGS ACCORD WITH OUR REQUIREMENTS AND AUTHORISE THEIR USE FOR NEXT STAGE PURPOSES.

SIGNED..... DATE.....

SIGNED..... DATE.....

SHEET CONTENT:

FLOORING - FIRST FLOOR

HOUSE TYPE:
HAMPTON 490

MIN LOT WIDTH:
14M

PROPERTY ADDRESS:
188 MONCRIEFF CRESCENT
WANDANA HEIGHTS

CLIENT:

SANDEEP & IMMACOLATA BANSAL

NORTH:

FACADE:

SCALE: 1 : 100

DATE: 20.12.22

SHEET NUMBER:

6.2

JOB NUMBER:

0188MON

JOB ISSUE:

1

ISSUE	DATE	REVISION DESCRIPTION	INITIALS
A	10.03.20	MASTER ISSUED	MP
B	9.11.21	AMEDED CAS. LIV. BULKHEAD TO LIGHT WEIGHT	MP
C	07.11.22	TENDER DRAWINGS, IDU & COLOUR DOC ADDED	CM
D	09.11.22	COLOUR CHECK ADDED	CM
E	10.11.22	ENERGY ADDED	CM
F	17.11.22	DA RFI	BL
G	30.11.22	ENG. ADDED, CONTRACT DRAWINGS ISSUED	BL
H	20.12.22	B.S RFI & CONTRACT QUOTE AMENDMENT	BL
I	21.12.22	AMEDED ENEGRY ADDED	BL

Diagram illustrating the roof structure details, showing the connection between the roof truss, metal roof batten, metal roof, and metal gutter & fascia. The diagram also shows the 10mm thick plasterboard ceiling and wall lining with a cove cornice.

Labels in the diagram:

- METAL ROOF BATTEN
- METAL ROOF
- METAL GUTTER & FASCIA
- ROOF TRUSS
- 10mm THICK PLASTERBOARD CEILING & WALL LINING WITH COVE CORNICE


LONG ISLAND HOMES ISLANDER	Long Island Homes Pty. Ltd. PO BOX 6269 Point Cook, Vic 3030 p. 61 3 9369 6486 (1800 604 011) f. 61 3 9369 0994 email: admin@longislandhomes.com.au www.longislandhomes.com.au	GENERAL NOTES: - THE CONTRACTOR IS RESPONSIBLE FOR SETTING OUT AND CHECKING ALL LEVELS AND DIMENSIONS ON SITE PRIOR TO COMMENCING ANY SITE WORKS. - FIGURED DIMENSIONS ARE TO TAKE PREFERENCE OVER SCALE - DIMENSIONS TO STRUCTURAL TIMBERS & FACE OF BRICKS EXCLUDING BATTENS, PLASTERBOARD ETC. - ALL DIMENSIONS ON PLAN ARE NOMINAL & MAY VARY TO ACTUAL SIZE - PROVIDE LOCKS TO ALL OPENABLE WINDOWS & EXTERNAL SLIDING DOORS (KEYED ALIKE). - MAN HOLE LOCATION MAY BE CHANGED DUE TO TRUSS LAYOUT. - WINDOW AND DOOR FRAME SIZES ARE NOMINAL AND MAY VARY WITH LONG ISLAND HOMES APPROVED SUPPLIERS.	CLIENT I / WE..... CONFIRM THESE DRAWINGS ACCORD WITH OUR REQUIREMENTS AND AUTHORISE THEIR USE FOR NEXT STAGE PURPOSES. SIGNED..... DATE..... SIGNED..... DATE.....	SIGN OFF	P R O J E C T	SHEET CONTENT: SECTION	HOUSE TYPE: HAMPTON 490	MIN LOT WIDTH: 14M	PROPERTY ADDRESS: 188 MONCRIEFF CRESCENT WANDANA HEIGHTS	CLIENT: SANDEEP & IMMACOLATA BANSAL	NORTH:	FACADE:	SCALE: As indicated	DATE: 20.12.22	SHEET NUMBER: 7.1	JOB NUMBER: 0188MON	JOB ISSUE: I																																		
	© Copyright THIS DESIGN & DRAWING SHALL REMAIN THE INTELLECTUAL PROPERTY OF LONG ISLAND HOMES PTY. LTD. AND SHALL NOT BE COPIED IN WHOLE OR PART WITHOUT WRITTEN CONSENT FROM LONG ISLAND HOMES PTY LTD. DB NUMBER: CDB - U 58094	REVISIONS <table border="1"> <thead> <tr> <th></th> <th>ISSUE</th> <th>DATE</th> <th>REVISION DESCRIPTION</th> <th>INITIALS</th> </tr> </thead> <tbody> <tr> <td>A</td> <td>10.03.20</td> <td></td> <td>MASTER ISSUED</td> <td>MP</td> </tr> <tr> <td>B</td> <td>9.11.21</td> <td></td> <td>AMEDED CAS. LIV. BULKHEAD TO LIGHT WEIGHT</td> <td>MP</td> </tr> <tr> <td>C</td> <td>07.11.22</td> <td></td> <td>TENDER DRAWINGS, IDU & COLOUR DOC ADDED</td> <td>CM</td> </tr> <tr> <td>D</td> <td>09.11.22</td> <td></td> <td>COLOUR CHECK ADDED</td> <td>CM</td> </tr> <tr> <td>E</td> <td>10.11.22</td> <td></td> <td>ENERGY ADDED</td> <td>CM</td> </tr> <tr> <td>F</td> <td>17.11.22</td> <td></td> <td>DA RFI</td> <td>BL</td> </tr> <tr> <td>G</td> <td>30.11.22</td> <td></td> <td>ENG. ADDED, CONTRACT DRAWINGS ISSUED</td> <td>BL</td> </tr> <tr> <td>H</td> <td>20.12.22</td> <td></td> <td>B.S RFI & CONTRACT QUOTE AMENDMENT</td> <td>BL</td> </tr> <tr> <td>I</td> <td>21.12.22</td> <td></td> <td>AMEDED ENERGY ADDED</td> <td>BL</td> </tr> </tbody> </table>				ISSUE	DATE	REVISION DESCRIPTION	INITIALS	A	10.03.20		MASTER ISSUED	MP	B	9.11.21		AMEDED CAS. LIV. BULKHEAD TO LIGHT WEIGHT	MP	C	07.11.22		TENDER DRAWINGS, IDU & COLOUR DOC ADDED	CM	D	09.11.22		COLOUR CHECK ADDED	CM	E	10.11.22		ENERGY ADDED	CM	F	17.11.22		DA RFI	BL	G	30.11.22		ENG. ADDED, CONTRACT DRAWINGS ISSUED	BL	H	20.12.22		B.S RFI & CONTRACT QUOTE AMENDMENT	BL	I	21.12.22
	ISSUE	DATE	REVISION DESCRIPTION	INITIALS	
A	10.03.20		MASTER ISSUED	MP	
B	9.11.21		AMEDED CAS. LIV. BULKHEAD TO LIGHT WEIGHT	MP	
C	07.11.22		TENDER DRAWINGS, IDU & COLOUR DOC ADDED	CM	
D	09.11.22		COLOUR CHECK ADDED	CM	
E	10.11.22		ENERGY ADDED	CM	
F	17.11.22		DA RFI	BL	
G	30.11.22		ENG. ADDED, CONTRACT DRAWINGS ISSUED	BL	
H	20.12.22		B.S RFI & CONTRACT QUOTE AMENDMENT	BL	
I	21.12.22		AMEDED ENERGY ADDED	BL	

21/12/2022 4:21:29 PM J:\LONG ISLAND JOBS\188 Moncrieff Crescent, Wandana Heights\DRAWING\0188MON_REV 1.rvt


NOTE: STAIRCASE MUST HAVE A TREAD SURFACE WITH A SLIP RESISTANCE OF NOT LESS THAN P3 OR P10 WHEN TESTED IN ACCORDANCE WITH AS4586, OR MUST INCORPORATE A NOSING STRIP WITH A SLIP RESISTANCE OF NOT LESS THAN P3 WHEN TESTED IN ACCORDANCE WITH AS4586.

NOTE: PROVIDE CONTINUOUS HANDRAILS TO STAIRCASES REGARDLESS IF BOUNDED BY WALLS, HANDRAIL SELECTION AS PER SPEC.

STAIRS (AS PER A.S 1170.1)
RISERS:
MAX - 190
MIN- 115mm
GOING:
MAX- 355mm
MIN- 240mm

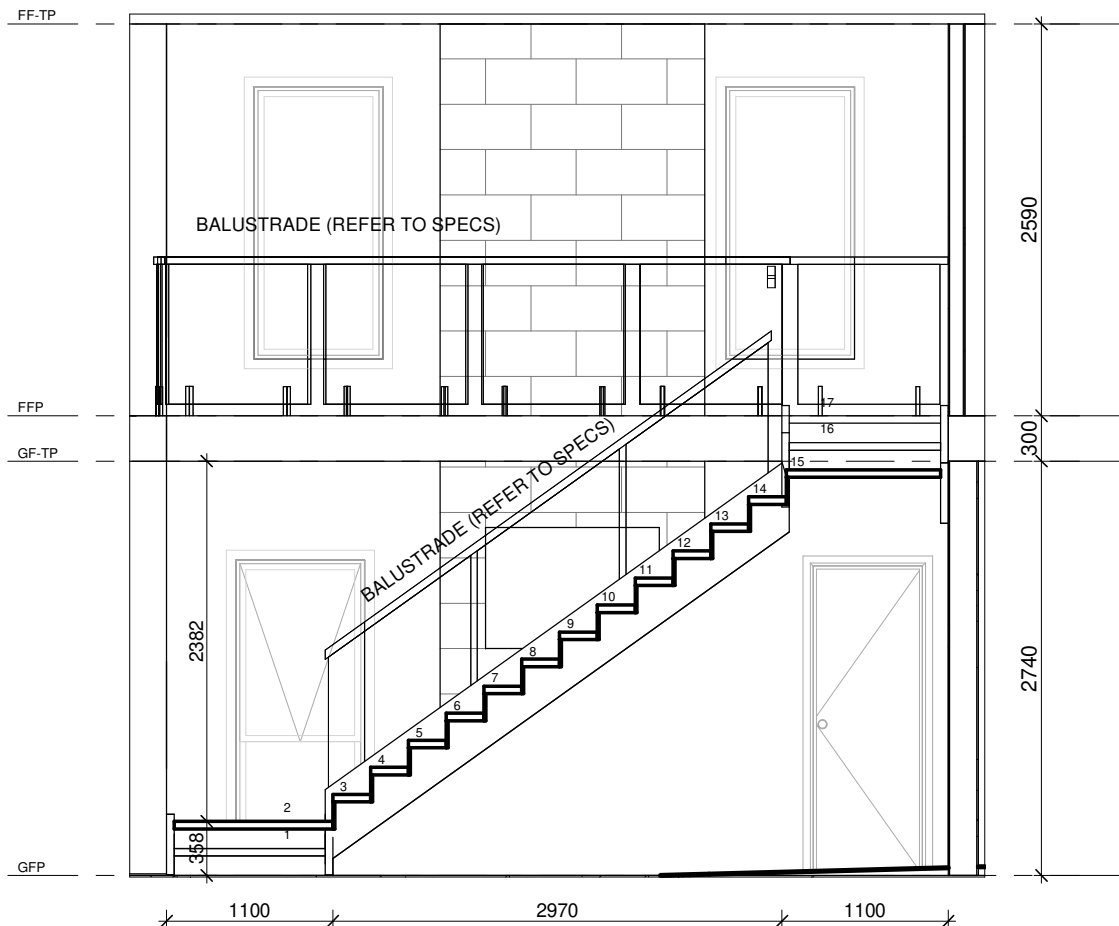

STAIR SECTION
SCALE 1 : 50

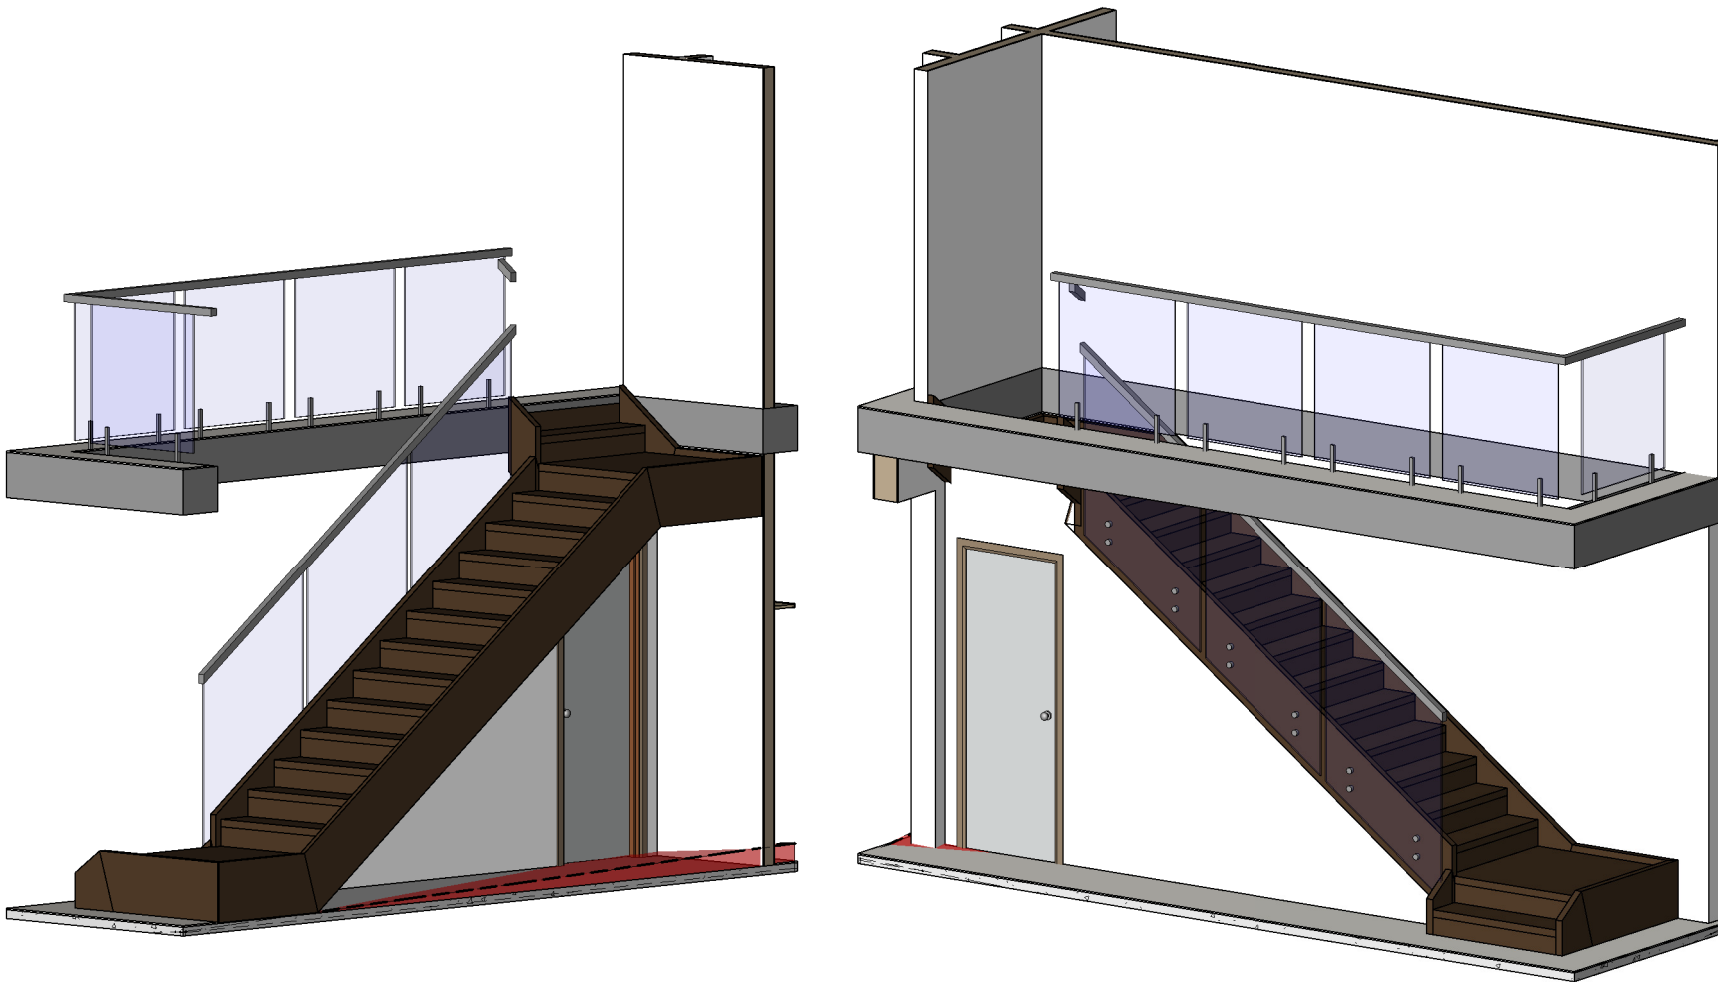

NOTE: 3D IMAGE IS TO DEPICT BALUSTRADING, DWARF WALLS AND FULL HEIGHT WALLS IN A GENERAL MANNER ONLY. SIZE AND POSITION OF POSTS, BALUSTERS, SPIGOTS, FRAMES, ETC ARE INDICATIVE ONLY. THEIR EXACT POSITIONING IS SUBJECT TO THE MANUFACTURER'S DISCRETION.



ISLANDER

Long Island Homes Pty. Ltd.
PO BOX 6269
Point Cook, Vic 3030
p. 61 3 9369 6486 (1800 604 011)
f. 61 3 9369 0994
email: admin@longislandhomes.com.au
www.longislandhomes.com.au

© Copyright
THIS DESIGN & DRAWING SHALL REMAIN THE INTELLECTUAL PROPERTY OF LONG ISLAND HOMES PTY. LTD. AND SHALL NOT BE COPIED IN WHOLE OR PART WITHOUT WRITTEN CONSENT FROM LONG ISLAND HOMES PTY LTD.
DB NUMBER: CDB - U 58094

GENERAL NOTES:

- THE CONTRACTOR IS RESPONSIBLE FOR SETTING OUT AND CHECKING ALL LEVELS AND DIMENSIONS ON SITE PRIOR TO COMMENCING ANY SITE WORKS.
- FIGURED DIMENSIONS ARE TO TAKE PREFERENCE OVER SCALE
- DIMENSIONS TO STRUCTURAL TIMBERS & FACE OF BRICKS EXCLUDING BATTENS, PLASTERBOARD ETC.
- ALL DIMENSIONS ON PLAN ARE NOMINAL & MAY VARY TO ACTUAL SIZE
- PROVIDE LOCKS TO ALL OPENABLE WINDOWS & EXTERNAL SLIDING DOORS (KEYED ALIKE).
- MAN HOLE LOCATION MAY BE CHANGED DUE TO TRUSS LAYOUT.
- WINDOW AND DOOR FRAME SIZES ARE NOMINAL AND MAY VARY WITH LONG ISLAND HOMES APPROVED SUPPLIERS.

CLIENT

I / WE.....

CONFIRM THESE DRAWINGS ACCORD WITH OUR REQUIREMENTS AND AUTHORISE THEIR USE FOR NEXT STAGE PURPOSES.

SIGNED..... DATE.....

SIGNED..... DATE.....

SHEET CONTENT:

STAIR DETAILS

HOUSE TYPE:
HAMPTON 490

MIN LOT WIDTH:
14M

PROPERTY ADDRESS:
**188 MONCRIEFF CRESCENT
WANDANA HEIGHTS**

CLIENT:
SANDEEP & IMMACOLATA BANSAL

NORTH:

FACADE:

SCALE: 1 : 50

DATE: 20.12.22

SHEET NUMBER:

7.2


JOB NUMBER:

0188MON


JOB ISSUE:

1

REVISIONS	ISSUE	DATE	REVISION DESCRIPTION	INITIALS
A	10.03.20		MASTER ISSUED	MP
B	9.11.21		AMEDED CAS. LIV. BULKHEAD TO LIGHT WEIGHT	MP
C	07.11.22		TENDER DRAWINGS, IDU & COLOUR DOC ADDED	CM
D	09.11.22		COLOUR CHECK ADDED	CM
E	10.11.22		ENERGY ADDED	CM
F	17.11.22		DA RFI	BL
G	30.11.22		ENG. ADDED, CONTRACT DRAWINGS ISSUED	BL
H	20.12.22		B.S RFI & CONTRACT QUOTE AMENDMENT	BL
I	21.12.22		AMENDED ENEGRY ADDED	BL

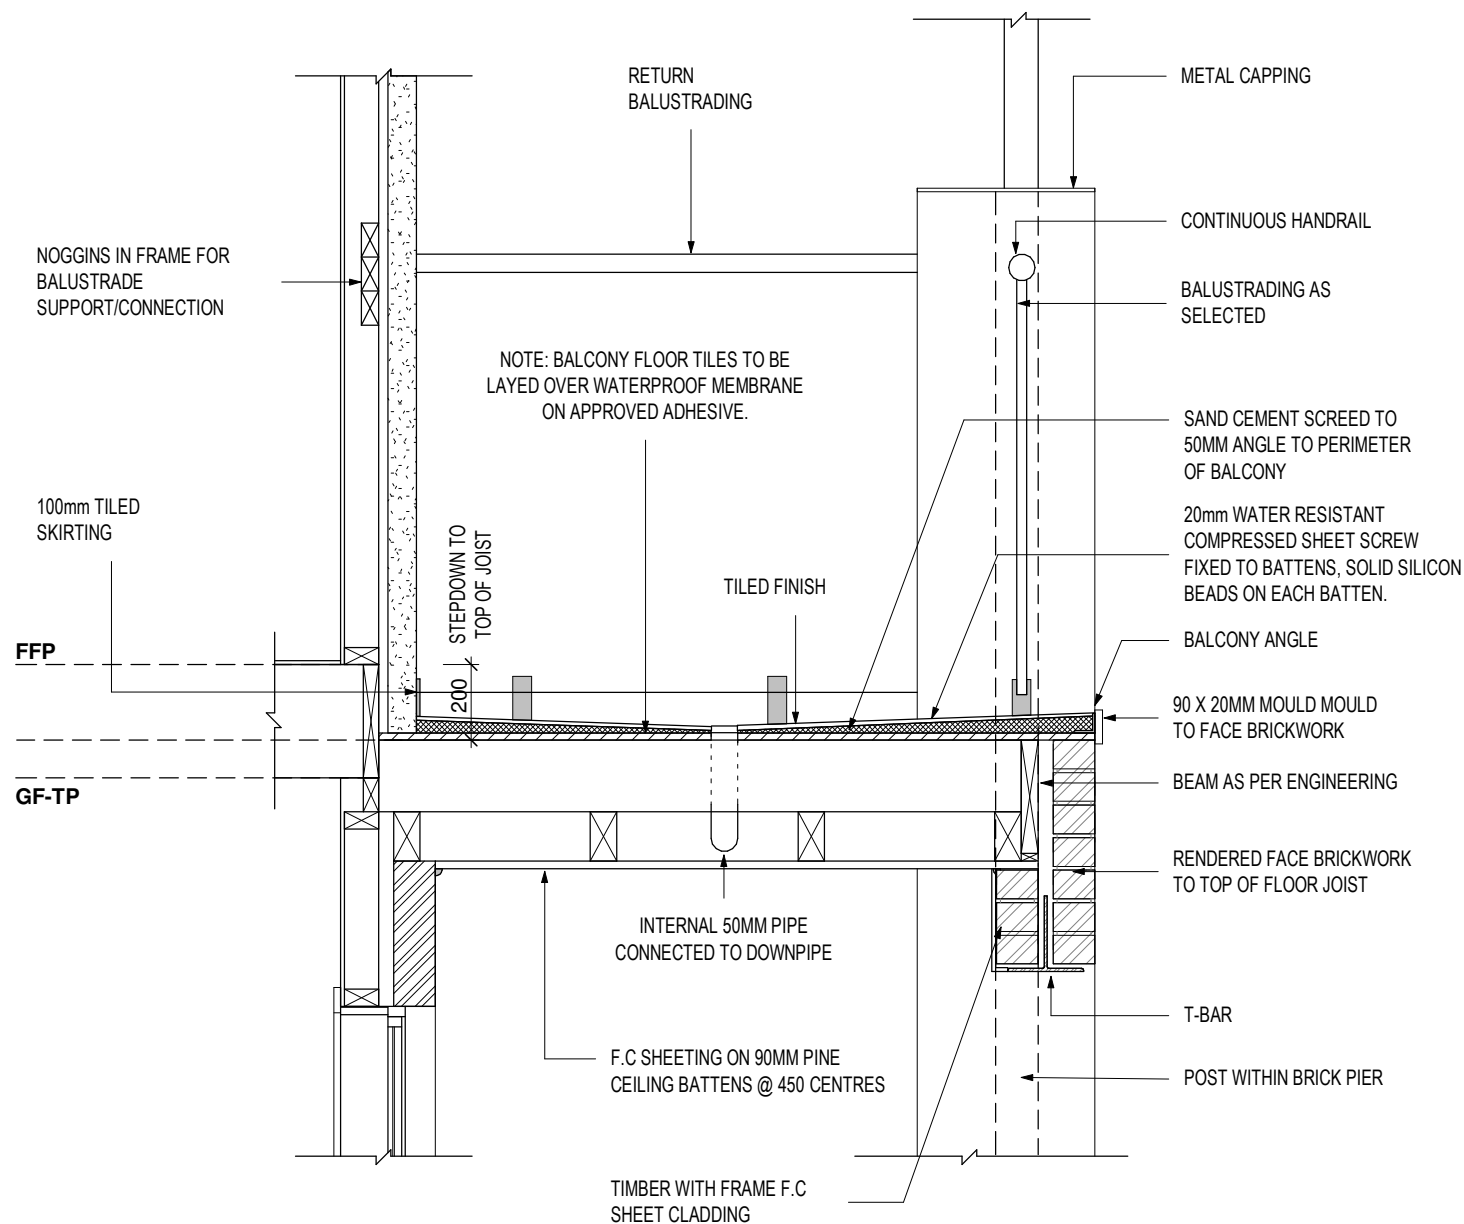

BALCONY 1 DETAIL
SCALE 1 : 20

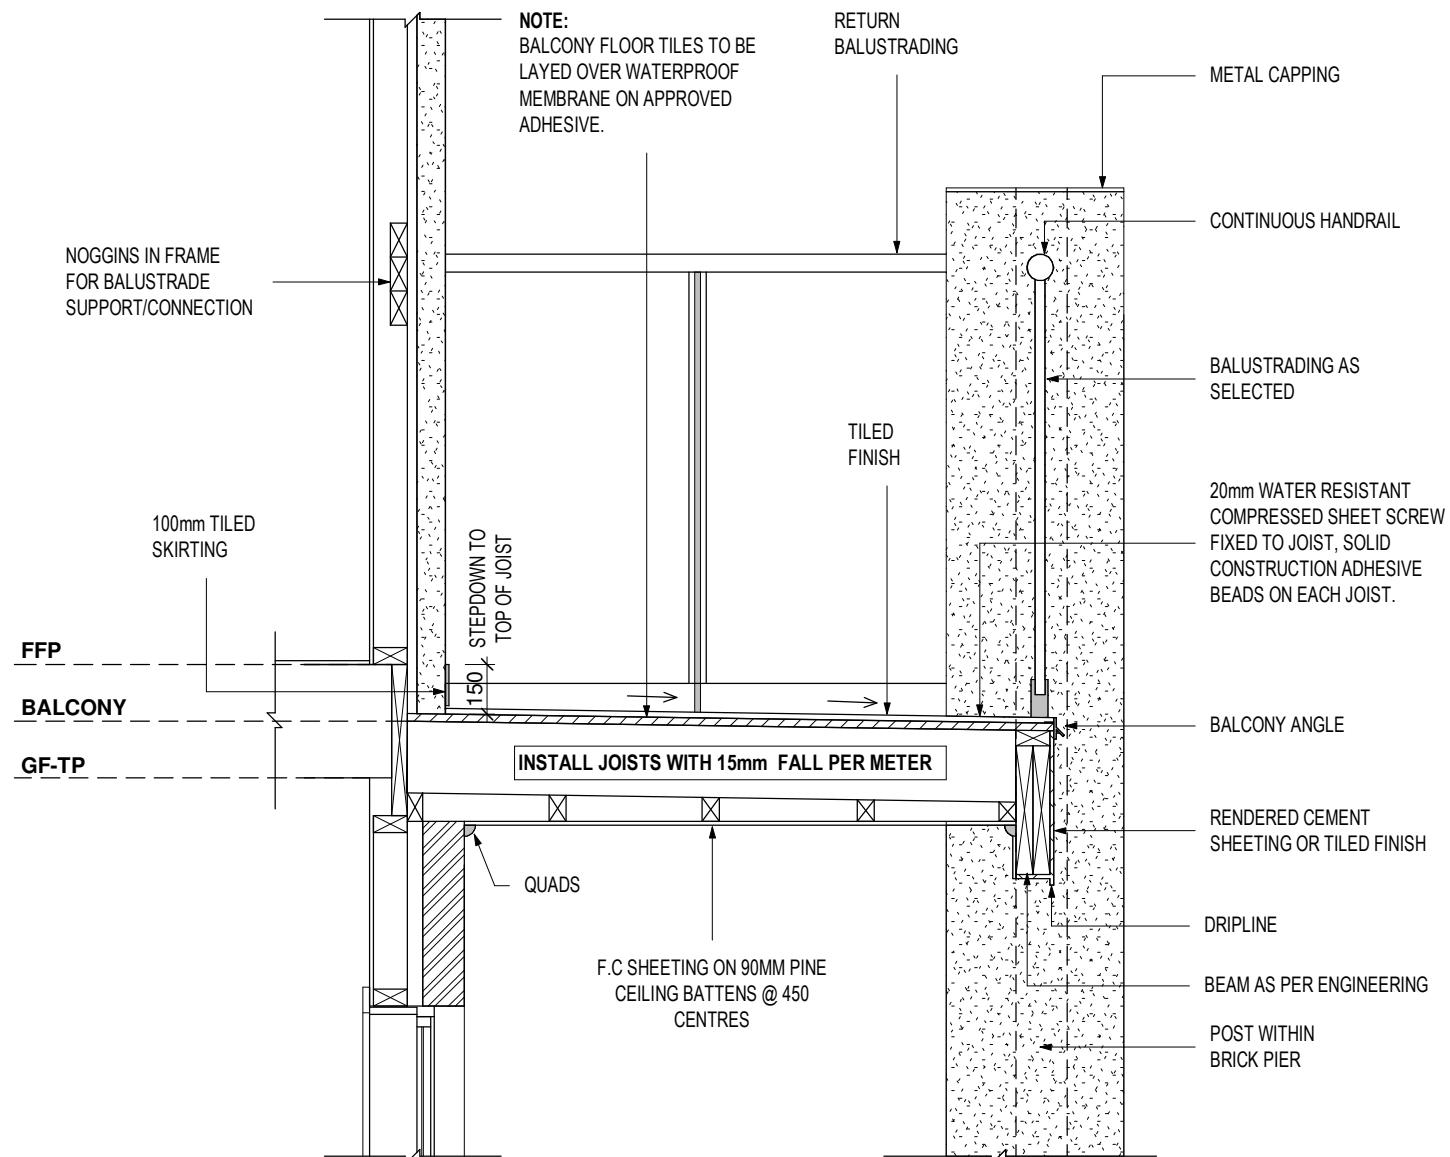

BALCONY 2 DETAIL
SCALE 1 : 20



ISLANDER

Long Island Homes Pty. Ltd.
PO BOX 6269
Point Cook, Vic 3030
p. 61 3 9369 6486 (1800 604 011)
f. 61 3 9369 0994
email: admin@longislandhomes.com.au
www.longislandhomes.com.au

© Copyright
THIS DESIGN & DRAWING SHALL REMAIN THE INTELLECTUAL PROPERTY OF
LONG ISLAND HOMES PTY. LTD. AND SHALL NOT BE COPIED IN WHOLE OR
PART WITHOUT WRITTEN CONSENT FROM LONG ISLAND HOMES PTY LTD.
DB NUMBER: CDB - U 58094

GENERAL NOTES:

- THE CONTRACTOR IS RESPONSIBLE FOR SETTING OUT AND CHECKING ALL LEVELS AND DIMENSIONS ON SITE PRIOR TO COMMENCING ANY SITE WORKS.
- FIGURED DIMENSIONS ARE TO TAKE PREFERENCE OVER SCALE
- DIMENSIONS TO STRUCTURAL TIMBERS & FACE OF BRICKS EXCLUDING BATTENS, PLASTERBOARD ETC.
- ALL DIMENSIONS ON PLAN ARE NOMINAL & MAY VARY TO ACTUAL SIZE
- PROVIDE LOCKS TO ALL OPENABLE WINDOWS & EXTERNAL SLIDING DOORS (KEYED ALIKE).
- MAN HOLE LOCATION MAY BE CHANGED DUE TO TRUSS LAYOUT.
- WINDOW AND DOOR FRAME SIZES ARE NOMINAL AND MAY VARY WITH LONG ISLAND HOMES APPROVED SUPPLIERS.

CLIENT

I / WE.....

CONFIRM THESE DRAWINGS ACCORD WITH OUR REQUIREMENTS AND AUTHORISE THEIR USE FOR NEXT STAGE PURPOSES.

SIGNED..... DATE.....

SIGNED..... DATE.....

SHEET CONTENT:

BALCONY DETAILS

HOUSE TYPE:
HAMPTON 490

MIN LOT WIDTH:
14M

PROPERTY ADDRESS:
188 MONCRIEFF CRESCENT
WANDANA HEIGHTS

CLIENT:
SANDEEP & IMMACOLATA BANSAL

NORTH:

FACADE:

SCALE: 1 : 20

DATE: 20.12.22

SHEET NUMBER:

7.3


JOB NUMBER:

0188MON


JOB ISSUE:

1


REVISIONS	ISSUE	DATE	REVISION DESCRIPTION	INITIALS
A	10.03.20		MASTER ISSUED	MP
B	9.11.21		AMEDED CAS. LIV. BULKHEAD TO LIGHT WEIGHT	MP
C	07.11.22		TENDER DRAWINGS, IDU & COLOUR DOC ADDED	CM
D	09.11.22		COLOUR CHECK ADDED	CM
E	10.11.22		ENERGY ADDED	CM
F	17.11.22		DA RFI	BL
G	30.11.22		ENG. ADDED, CONTRACT DRAWINGS ISSUED	BL
H	20.12.22		B.S RFI & CONTRACT QUOTE AMENDMENT	BL
I	21.12.22		AMEDED ENEGRY ADDED	BL

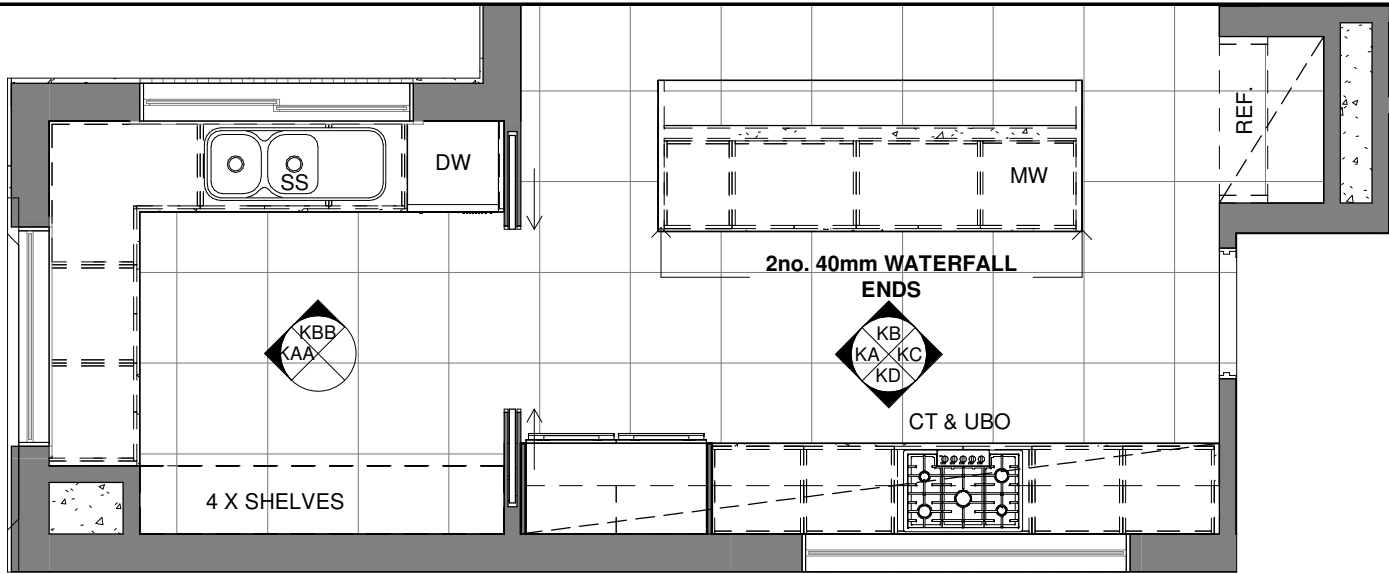

KITCHEN & BUTLERS PLAN
SCALE 1 : 50

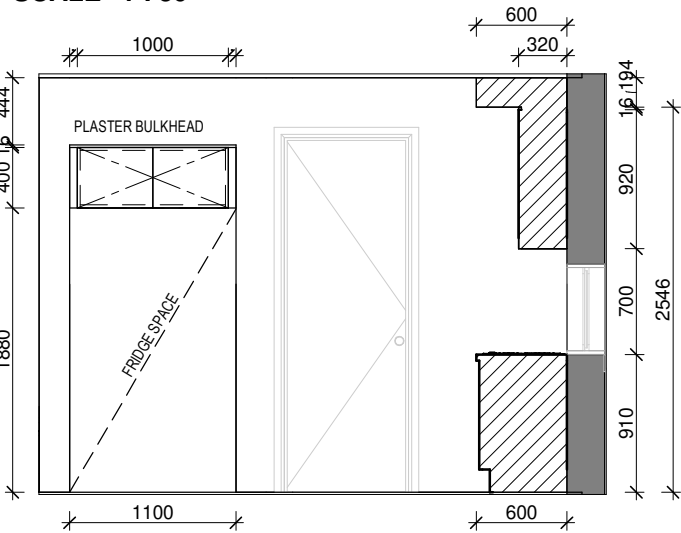


ELEVATION - KA

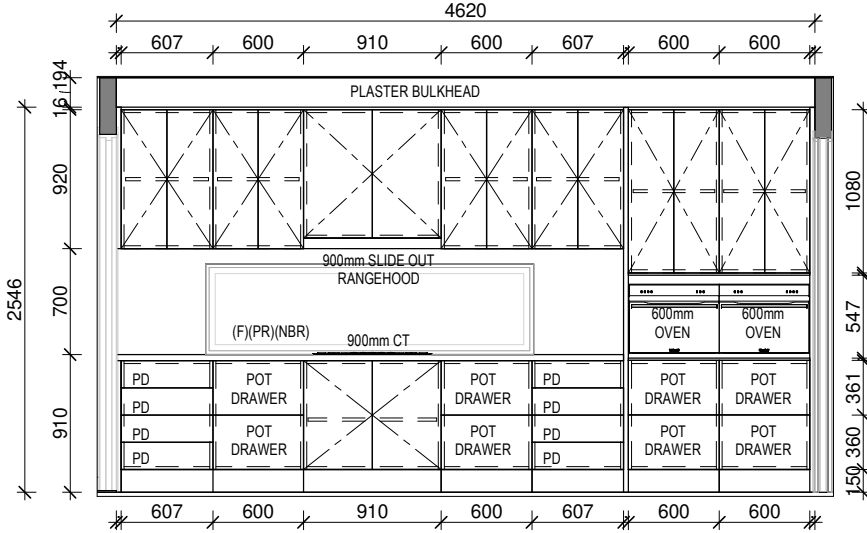


ELEVATION - KB

ELEVATION - KA
KITCHEN ELEVATIONS


ELEVATION - KB

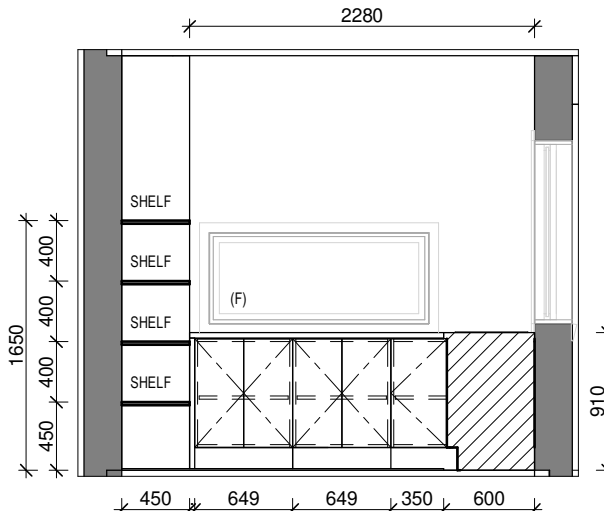


ELEVATION - KAA

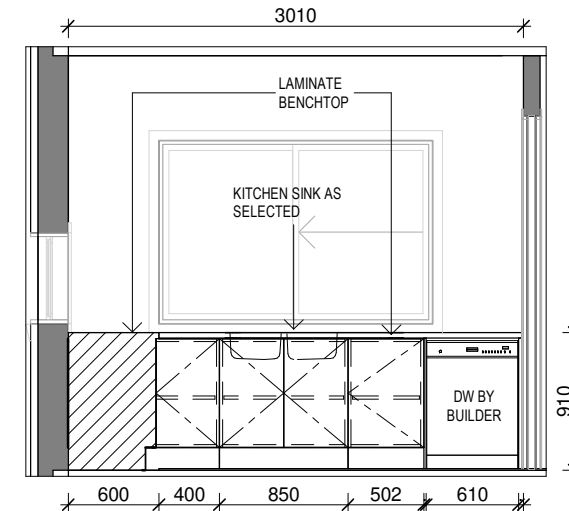


ELEVATION - KBB

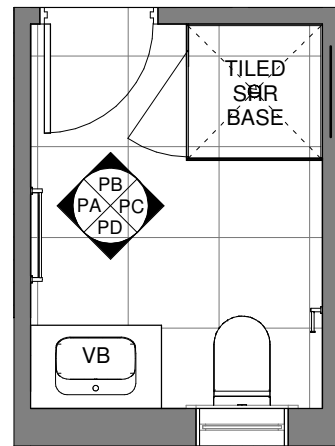


PDR PLAN
SCALE 1 : 50

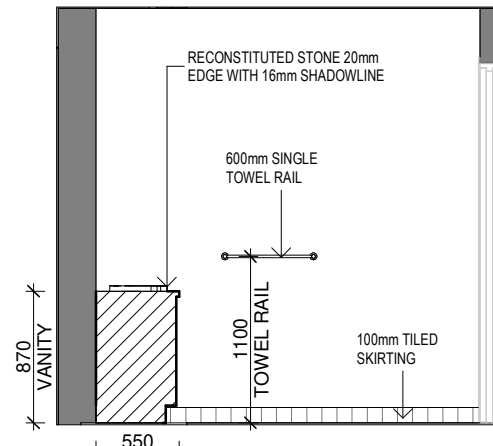


ELEVATION - PA
PDR ELEVATIONS

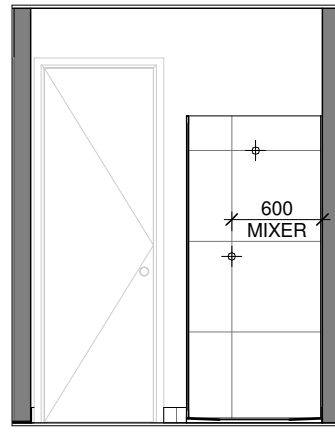

ELEVATION - PB

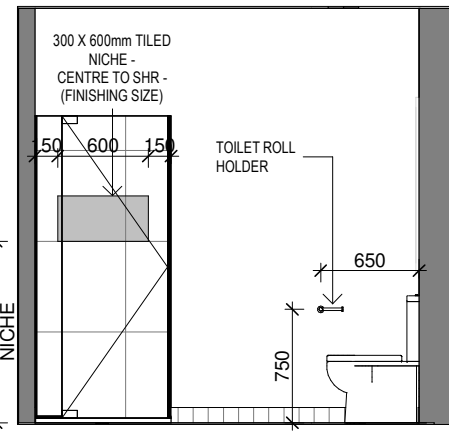

ELEVATION - PC

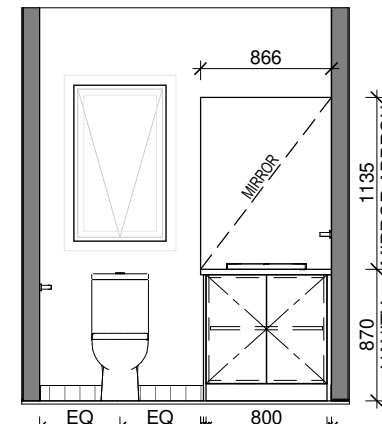

ELEVATION - PD

NOTE:

- PROVIDE SOFT CLOSING MECHANISM TO KITCHEN CABINETY DOORS ONLY
- PROVIDE 20MM OVERHANG TO ALL OVERHEAD CABINETY EXCEPT CABINETY ABOVE RANGEHOOD
- PROVIDE TOUCH RELEASE TO KITCHEN CABINETY AND POT DRAWERS



ISLANDER

Long Island Homes Pty. Ltd.
PO BOX 6269
Point Cook, Vic 3030
p. 61 3 9369 6486 (1800 604 011)
f. 61 3 9369 0994
email: admin@longislandhomes.com.au
www.longislandhomes.com.au

© Copyright
THIS DESIGN & DRAWING SHALL REMAIN THE INTELLECTUAL PROPERTY OF LONG ISLAND HOMES PTY. LTD. AND SHALL NOT BE COPIED IN WHOLE OR PART WITHOUT WRITTEN CONSENT FROM LONG ISLAND HOMES PTY LTD.
DB NUMBER: CDB - U 58094

GENERAL NOTES:

- THE CONTRACTOR IS RESPONSIBLE FOR SETTING OUT AND CHECKING ALL LEVELS AND DIMENSIONS ON SITE PRIOR TO COMMENCING ANY SITE WORKS.
- FIGURED DIMENSIONS ARE TO TAKE PREFERENCE OVER SCALE
- DIMENSIONS TO STRUCTURAL TIMBERS & FACE OF BRICKS EXCLUDING BATTENS, PLASTERBOARD ETC.
- ALL DIMENSIONS ON PLAN ARE NOMINAL & MAY VARY TO ACTUAL SIZE
- PROVIDE LOCKS TO ALL OPENABLE WINDOWS & EXTERNAL SLIDING DOORS (KEYED ALIKE).
- MAN HOLE LOCATION MAY BE CHANGED DUE TO TRUSS LAYOUT.
- WINDOW AND DOOR FRAME SIZES ARE NOMINAL AND MAY VARY WITH LONG ISLAND HOMES APPROVED SUPPLIERS.

CLIENT

I / WE.....

CONFIRM THESE DRAWINGS ACCORD WITH OUR REQUIREMENTS AND AUTHORISE THEIR USE FOR NEXT STAGE PURPOSES.

SIGNED..... DATE.....

SIGNED..... DATE.....

SHEET CONTENT:


KITCHEN, BUTLERS & PDR

HOUSE TYPE: **HAMPTON 490** MIN LOT WIDTH: **14M**


PROPERTY ADDRESS: **188 MONCRIEFF CRESCENT WANDANA HEIGHTS**

CLIENT: **SANDEEP & IMMACOLATA BANSAL**


NORTH:			FACADE:		SHEET NUMBER: 8.1		JOB NUMBER: 0188MON	
			SCALE: As indicated				JOB ISSUE:	
			DATE: 20.12.22				I	
REVISIONS	ISSUE	DATE	REVISION DESCRIPTION					INITIALS
	A	10.03.20	MASTER ISSUED					MP
	B	9.11.21	AMENDED GAS. LIV. BULKHEAD TO LIGHT WEIGHT					MP
	C	07.11.22	TENDER DRAWINGS, IDU & COLOUR DOC ADDED					CM
	D	09.11.22	COLOUR CHECK ADDED					CM
	E	10.11.22	ENERGY ADDED					CM
	F	17.11.22	DA RFI					BL
	G	30.11.22	ENG. ADDED, CONTRACT DRAWINGS ISSUED					BL
	H	20.12.22	B.S RFI & CONTRACT QUOTE AMENDMENT					BL
	I	21.12.22	AMENDED ENRGY ADDED					BL

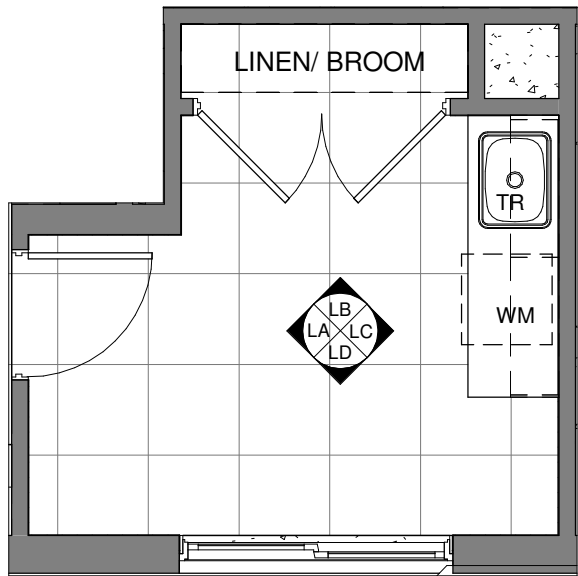


LAUNDRY PLAN
SCALE 1 : 50

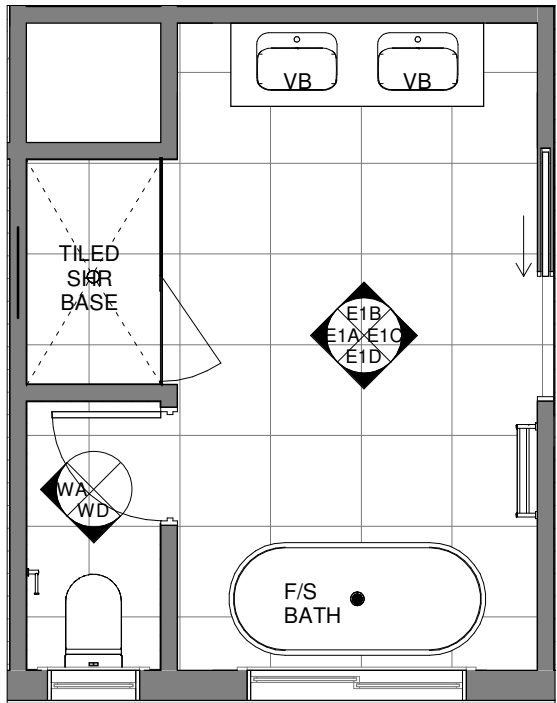


ENS 1 PLAN
SCALE 1 : 50

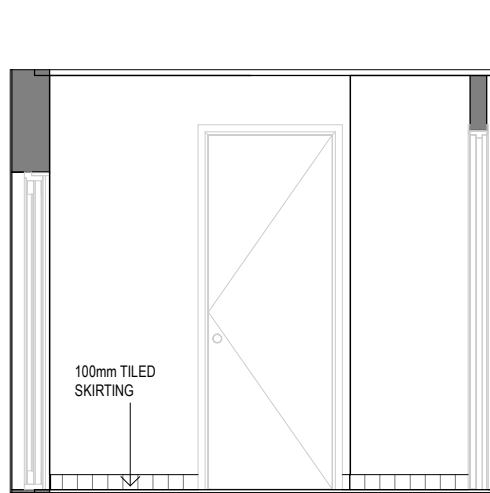


ELEVATION - LA
LAUNDRY ELEVATIONS

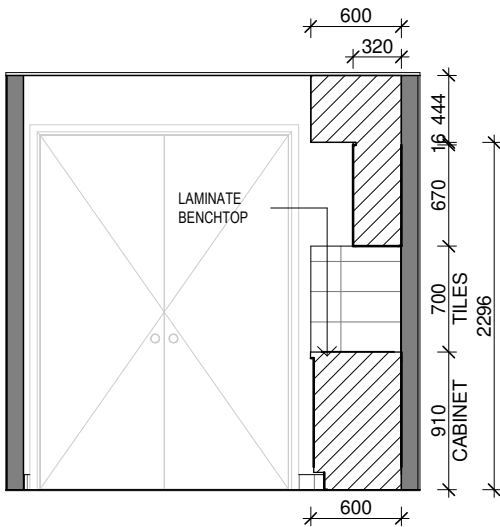


ELEVATION - LB

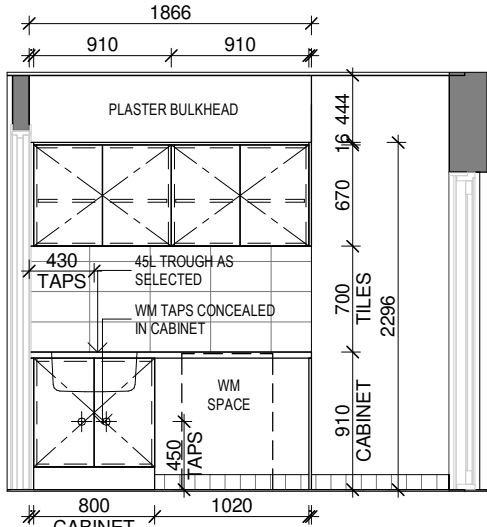


ELEVATION - LC

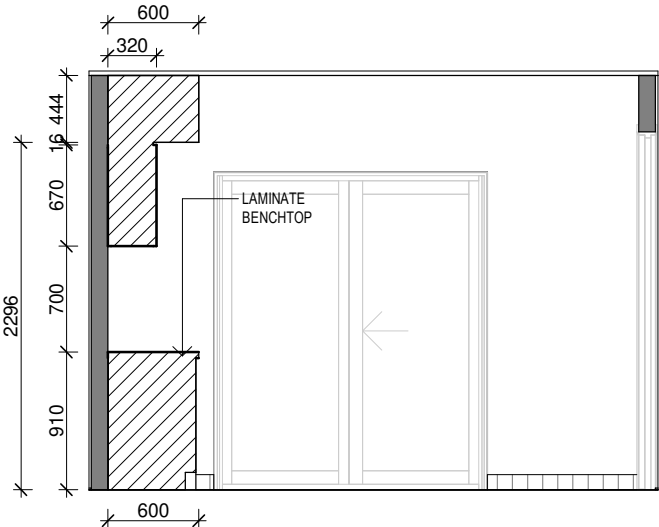


ELEVATION - LD

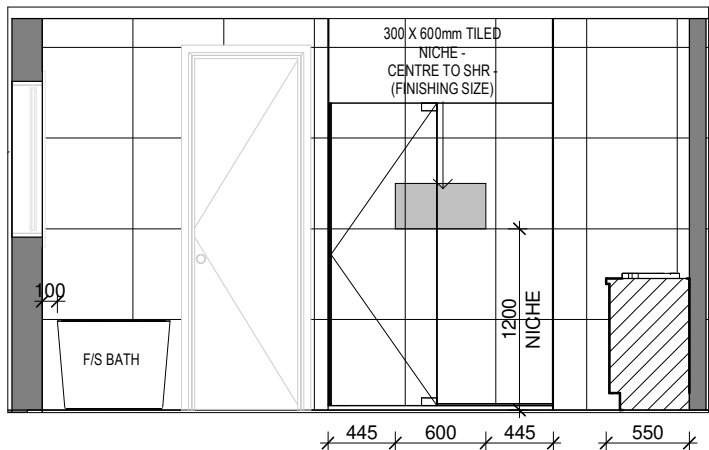


ELEVATION - E1A
ENS 1 ELEVATIONS

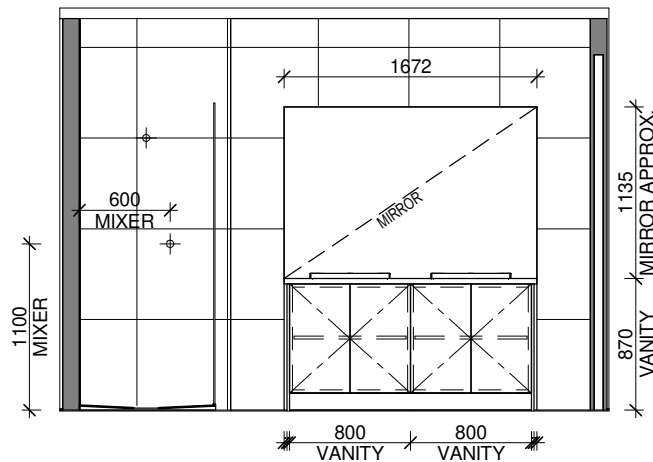


ELEVATION - E1B

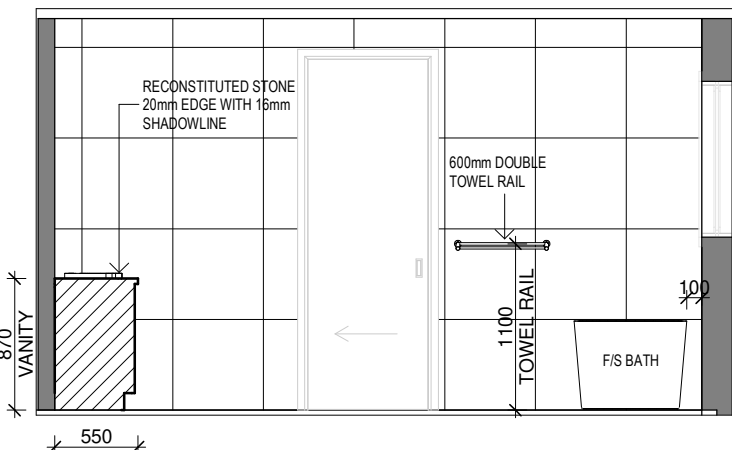


ELEVATION - E1C

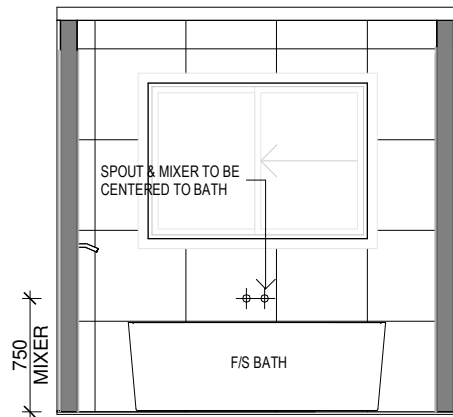

ELEVATION - E1D

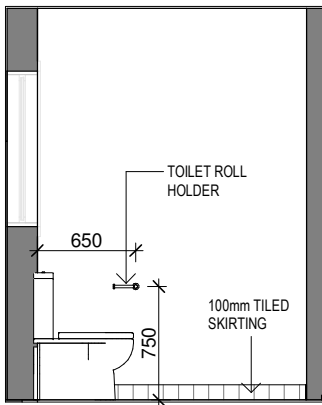

ELEVATION - WA
WC ELEVATIONS

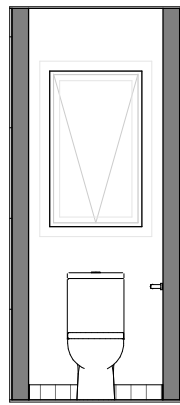

ELEVATION - WD



ISLANDER

Long Island Homes Pty. Ltd.
PO BOX 6269
Point Cook, Vic 3030
p. 61 3 9369 6486 (1800 604 011)
f. 61 3 9369 0994
email: admin@longislandhomes.com.au
www.longislandhomes.com.au

© Copyright
THIS DESIGN & DRAWING SHALL REMAIN THE INTELLECTUAL PROPERTY OF
LONG ISLAND HOMES PTY. LTD. AND SHALL NOT BE COPIED IN WHOLE OR
PART WITHOUT WRITTEN CONSENT FROM LONG ISLAND HOMES PTY LTD.
DB NUMBER: CDB - U 58094

GENERAL NOTES:

- THE CONTRACTOR IS RESPONSIBLE FOR SETTING OUT AND CHECKING ALL LEVELS AND DIMENSIONS ON SITE PRIOR TO COMMENCING ANY SITE WORKS.
- FIGURED DIMENSIONS ARE TO TAKE PREFERENCE OVER SCALE
- DIMENSIONS TO STRUCTURAL TIMBERS & FACE OF BRICKS EXCLUDING BATTENS, PLASTERBOARD ETC.
- ALL DIMENSIONS ON PLAN ARE NOMINAL & MAY VARY TO ACTUAL SIZE
- PROVIDE LOCKS TO ALL OPENABLE WINDOWS & EXTERNAL SLIDING DOORS (KEYED ALIKE).
- MAN HOLE LOCATION MAY BE CHANGED DUE TO TRUSS LAYOUT.
- WINDOW AND DOOR FRAME SIZES ARE NOMINAL AND MAY VARY WITH LONG ISLAND HOMES APPROVED SUPPLIERS.

CLIENT

I / WE.....

CONFIRM THESE DRAWINGS ACCORD WITH OUR REQUIREMENTS AND AUTHORISE THEIR USE FOR NEXT STAGE PURPOSES.

SIGNED..... DATE.....

SIGNED..... DATE.....

SHEET CONTENT:

L'DRY,ENS 1

HOUSE TYPE:
HAMPTON 490

MIN LOT WIDTH:
14M

PROPERTY ADDRESS:
188 MONCRIEFF CRESCENT
WANDANA HEIGHTS

CLIENT:
SANDEEP & IMMACOLATA BANSAL

NORTH:

FACADE:

SCALE: 1 : 50

DATE: 20.12.22

SHEET NUMBER:

8.2


JOB NUMBER:

0188MON


JOB ISSUE:

1


ISSUE	DATE	REVISION DESCRIPTION	INITIALS
A	10.03.20	MASTER ISSUED	MP
B	9.11.21	AMEDED CAS. LIV. BULKHEAD TO LIGHT WEIGHT	MP
C	07.11.22	TENDER DRAWINGS, IDU & COLOUR DOC ADDED	CM
D	09.11.22	COLOUR CHECK ADDED	CM
E	10.11.22	ENERGY CHECK ADDED	CM
F	17.11.22	DA RFI	BL
G	30.11.22	ENG. ADDED, CONTRACT DRAWINGS ISSUED	BL
H	20.12.22	B.S RFI & CONTRACT QUOTE AMENDMENT	BL
I	21.12.22	AMEDED ENEGRY ADDED	BL

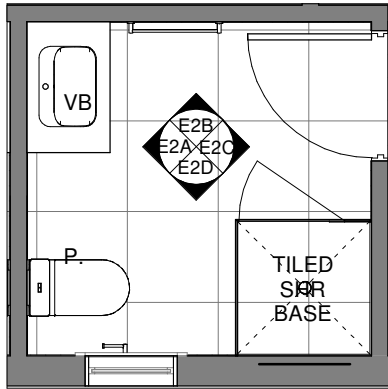


ENS 2 PLAN
SCALE 1 : 50

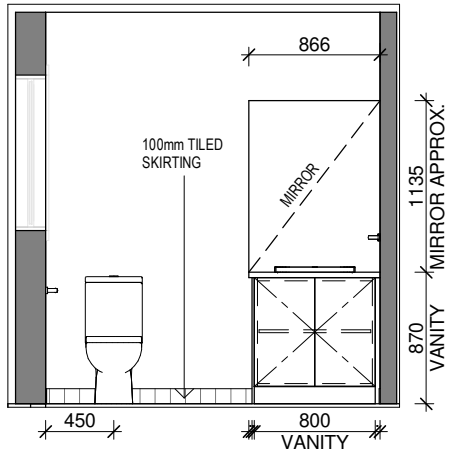


ELEVATION - E2A
ENS 2 ELEVATIONS

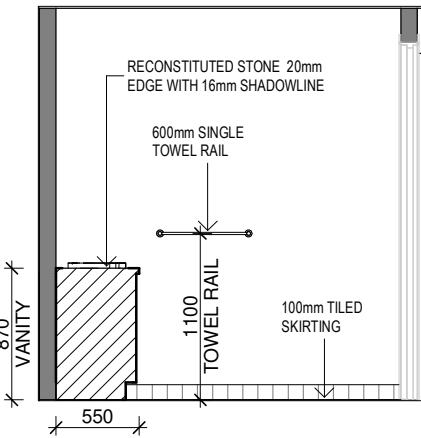


ELEVATION - E2B

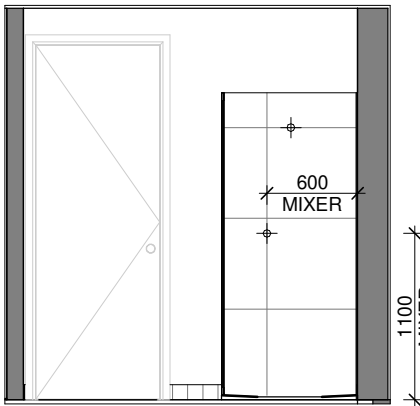


ELEVATION - E2C

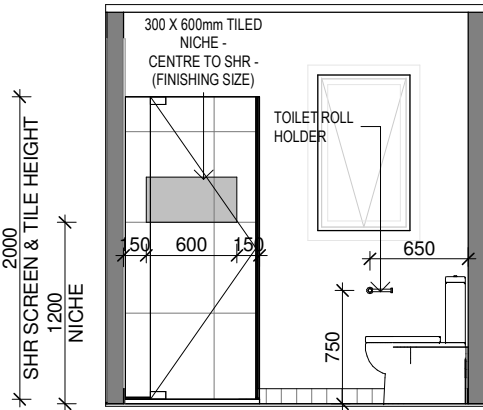


ELEVATION - E2D

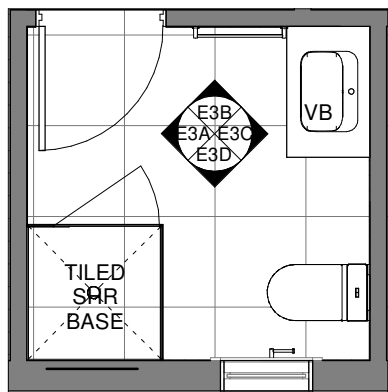


ENS 3 PLAN
SCALE 1 : 50

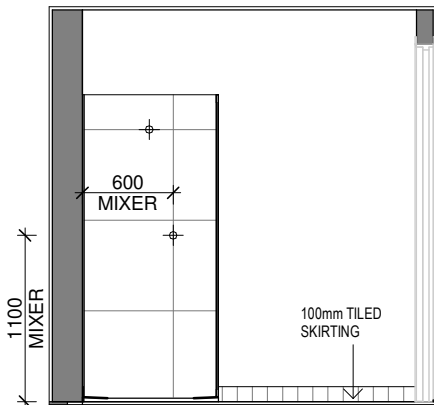


ELEVATION - E3A
ENS 3 ELEVATIONS

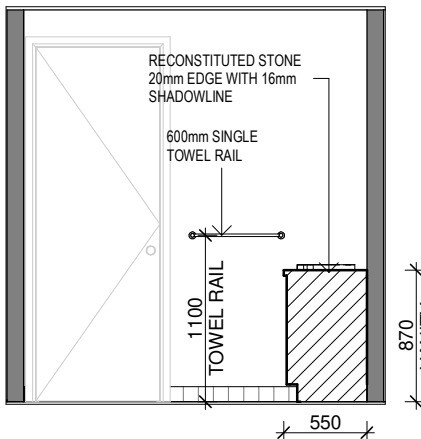


ELEVATION - E3B

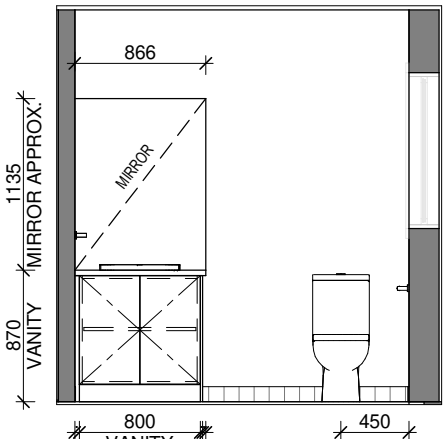


ELEVATION - E3C

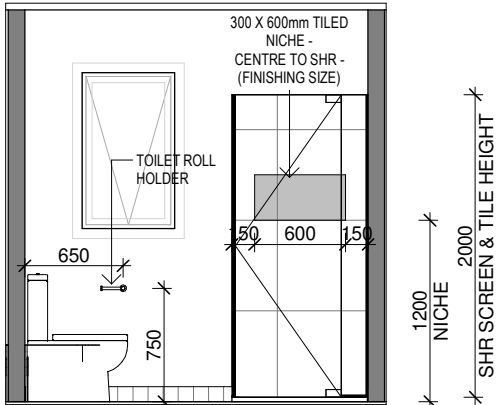


ELEVATION - E3D

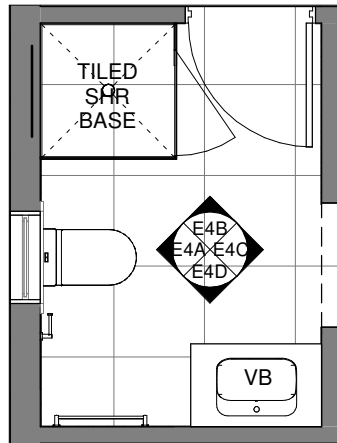


ENS 4 PLAN
SCALE 1 : 50

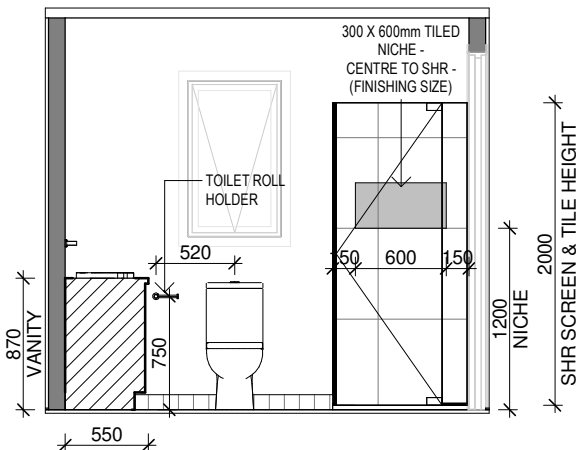


ELEVATION - E4A
ENS 4 ELEVATIONS

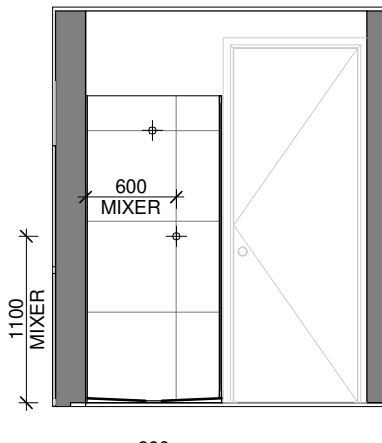

ELEVATION - E4B

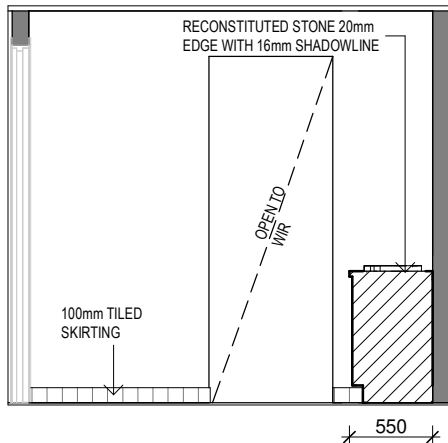

ELEVATION - E4C

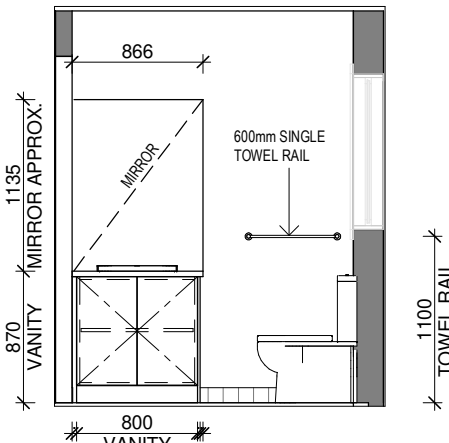

ELEVATION - E4D

GENERAL NOTES:

- THE CONTRACTOR IS RESPONSIBLE FOR SETTING OUT AND CHECKING ALL LEVELS AND DIMENSIONS ON SITE PRIOR TO COMMENCING ANY SITE WORKS.
- FIGURED DIMENSIONS ARE TO TAKE PREFERENCE OVER SCALE
- DIMENSIONS TO STRUCTURAL TIMBERS & FACE OF BRICKS EXCLUDING BATTENS, PLASTERBOARD ETC.
- ALL DIMENSIONS ON PLAN ARE NOMINAL & MAY VARY TO ACTUAL SIZE
- PROVIDE LOCKS TO ALL OPENABLE WINDOWS & EXTERNAL SLIDING DOORS (KEYED ALIKE).
- MAN HOLE LOCATION MAY BE CHANGED DUE TO TRUSS LAYOUT.
- WINDOW AND DOOR FRAME SIZES ARE NOMINAL AND MAY VARY WITH LONG ISLAND HOMES APPROVED SUPPLIERS.

CLIENT

I / WE.....
CONFIRM THESE DRAWINGS ACCORD WITH OUR REQUIREMENTS AND AUTHORISE THEIR USE FOR NEXT STAGE PURPOSES.
SIGNED..... DATE.....
SIGNED..... DATE.....

SHEET CONTENT:
ENS 2, ENS 3, ENS 4

HOUSE TYPE:
HAMPTON 490

MIN LOT WIDTH:
14M

PROPERTY ADDRESS:
188 MONCRIEFF CRESCENT
WANDANA HEIGHTS

CLIENT:
SANDEEP & IMMACOLATA BANSAL

NORTH:

FAÇADE:

SCALE: 1 : 50

DATE: 20.12.22

SHEET NUMBER:

8.3

JOB NUMBER:

0188MON

JOB ISSUE:

1


ISSUE	DATE	REVISION DESCRIPTION	INITIALS
A	10.03.20	MASTER ISSUED	MP
B	9.11.21	AMEDED CAS. LIV. BULKHEAD TO LIGHT WEIGHT	MP
C	07.11.22	TENDER DRAWINGS, IDU & COLOUR DOC ADDED	CM
D	09.11.22	COLOUR CHECK ADDED	CM
E	10.11.22	ENERGY ADDED	CM
F	17.11.22	DA RFI	BL
G	30.11.22	ENG. ADDED, CONTRACT DRAWINGS ISSUED	BL
H	20.12.22	B.S RFI & CONTRACT QUOTE AMENDMENT	BL
I	21.12.22	AMENDED ENEGRY ADDED	BL




ISLANDER

Long Island Homes Pty. Ltd.
PO BOX 6269
Point Cook, Vic 3030
p. 61 3 9369 6486 (1800 604 011)
f. 61 3 9369 0994
email: admin@longislandhomes.com.au
www.longislandhomes.com.au


© Copyright
THIS DESIGN & DRAWING SHALL REMAIN THE INTELLECTUAL PROPERTY OF LONG ISLAND HOMES PTY. LTD. AND SHALL NOT BE COPIED IN WHOLE OR PART WITHOUT WRITTEN CONSENT FROM LONG ISLAND HOMES PTY LTD.
DB NUMBER: CDB - U 58094

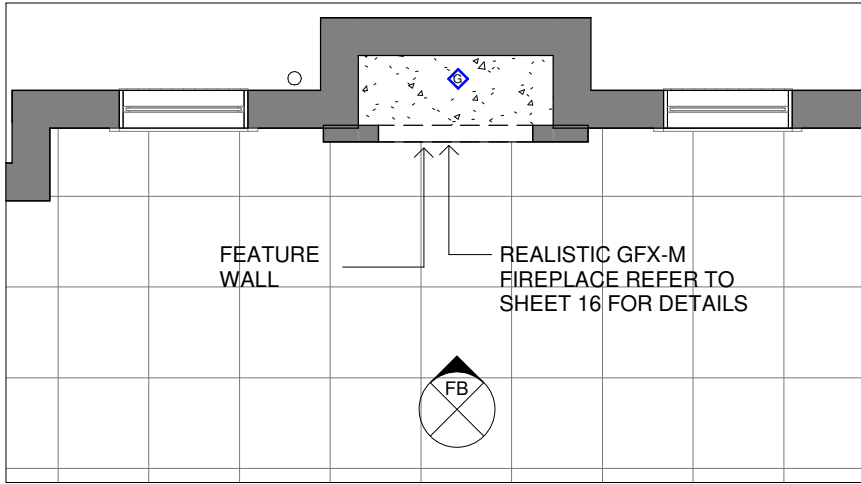


LIVING PLAN
SCALE 1 : 50

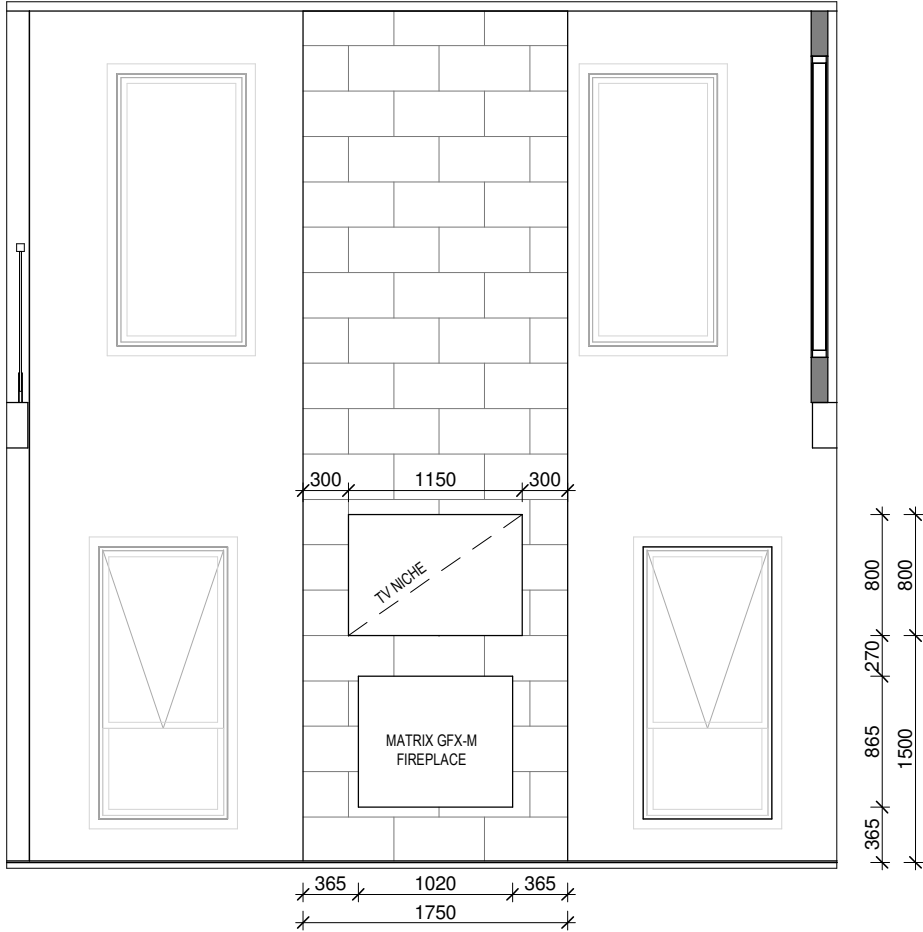

LIVING ROOM FIREPLACE DETAIL - ELEVATION - FB

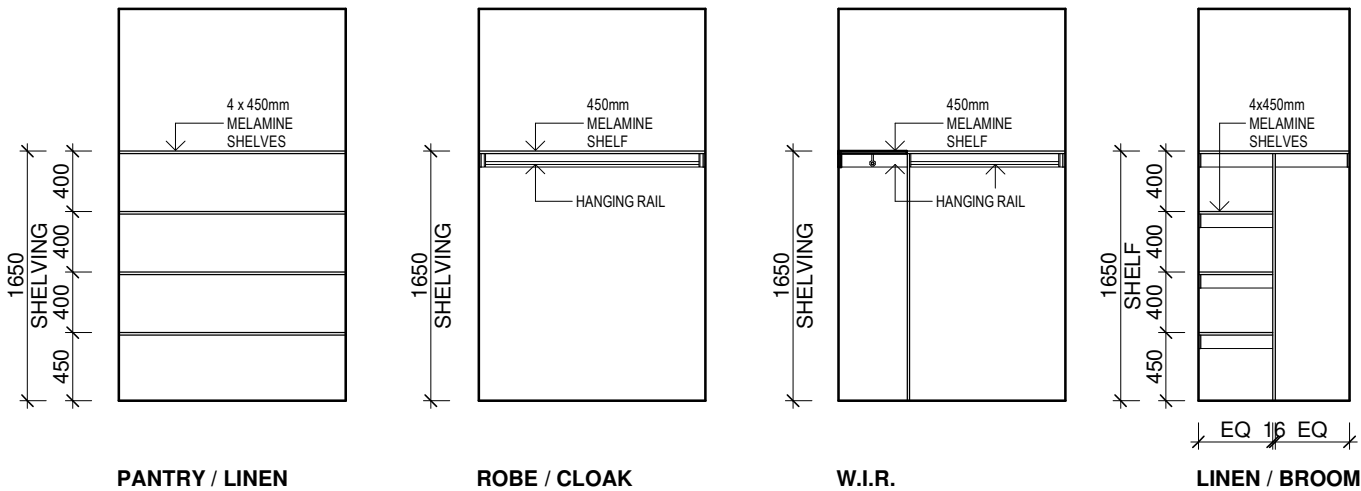

PANTRY / LINEN
ROBE / CLOAK
W.I.R.
LINEN / BROOM
TYPICAL INTERNAL ELEVATIONS

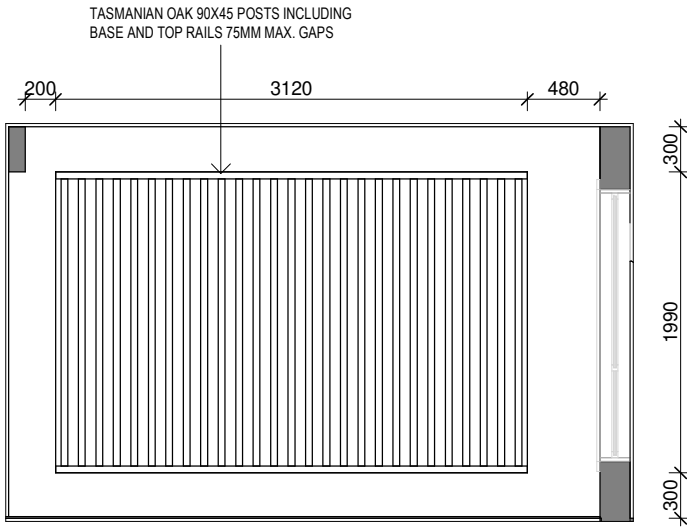

STUDY FEATURE WALL



ISLANDER

Long Island Homes Pty. Ltd.
PO BOX 6269
Point Cook, Vic 3030
p. 61 3 9369 6486 (1800 604 011)
f. 61 3 9369 0994
email: admin@longislandhomes.com.au
www.longislandhomes.com.au

© Copyright
THIS DESIGN & DRAWING SHALL REMAIN THE INTELLECTUAL PROPERTY OF
LONG ISLAND HOMES PTY. LTD. AND SHALL NOT BE COPIED IN WHOLE OR
PART WITHOUT WRITTEN CONSENT FROM LONG ISLAND HOMES PTY LTD.
DB NUMBER: CDB - U 58094

GENERAL NOTES:
- THE CONTRACTOR IS RESPONSIBLE FOR SETTING OUT AND CHECKING ALL LEVELS AND DIMENSIONS ON SITE PRIOR TO COMMENCING ANY SITE WORKS.
- FIGURED DIMENSIONS ARE TO TAKE PREFERENCE OVER SCALE
- DIMENSIONS TO STRUCTURAL TIMBERS & FACE OF BRICKS EXCLUDING BATTENS, PLASTERBOARD ETC.
- ALL DIMENSIONS ON PLAN ARE NOMINAL & MAY VARY TO ACTUAL SIZE
- PROVIDE LOCKS TO ALL OPENABLE WINDOWS & EXTERNAL SLIDING DOORS (KEYED ALIKE).
- MAN HOLE LOCATION MAY BE CHANGED DUE TO TRUSS LAYOUT.
- WINDOW AND DOOR FRAME SIZES ARE NOMINAL AND MAY VARY WITH LONG ISLAND HOMES APPROVED SUPPLIERS.

CLIENT

I / WE.....
CONFIRM THESE DRAWINGS ACCORD WITH OUR REQUIREMENTS AND AUTHORISE THEIR USE FOR NEXT STAGE PURPOSES.

SIGNED..... DATE.....
SIGNED..... DATE.....

SHEET CONTENT:
LIVING & TYPICAL

HOUSE TYPE: HAMPTON 490
MIN LOT WIDTH: 14M

PROPERTY ADDRESS:
188 MONCRIEFF CRESCENT
WANDANA HEIGHTS

CLIENT:
SANDEEP & IMMACOLATA BANSAL


NORTH:
FACADE:
SCALE: 1 : 50
DATE: 20.12.22
SHEET NUMBER: 8.4
JOB NUMBER: 0188MON
JOB ISSUE: I

REVISIONS	ISSUE	DATE	REVISION DESCRIPTION	INITIALS
D	09.11.22		COLOUR CHECK ADDED	CM
E	10.11.22		ENERGY ADDED	CM
F	17.11.22		DA RFI	BL
G	30.11.22		ENG. ADDED, CONTRACT DRAWINGS ISSUED	BL
H	20.12.22		B.S RFI & CONTRACT QUOTE AMENDMENT	BL
I	21.12.22		AMENDED ENEGRY ADDED	BL

LANDSCAPE LEGEND




DENOTES PLAIN CONCRETE

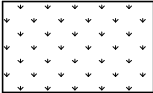


DENOTES TOPSOIL / GRASS SEED



DENOTES MEDIUM SHRUBS

 


DENOTES COLOURED CONCRETE

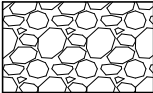


DENOTES CRUSHED ROCK



DENOTES SMALL SHRUBS

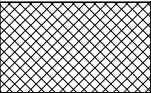


DENOTES EXPOSED AGGREGATE

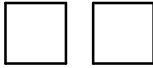


DENOTES CONCRETE PAVERS



DENOTES GROUND COVERS

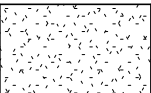

DENOTES DROUGHT TOLERANT PLANTS AND MULCH

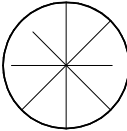


DENOTES TREE IN A 75-LITRE POT WHEN PLANTED



LETTERBOX DESIGN

NOTE: ALL LANDSCAPING TO BE COMPLETED BY CLIENT AFTER HANDOVER AS PER DEVELOPER'S GUIDELINES.

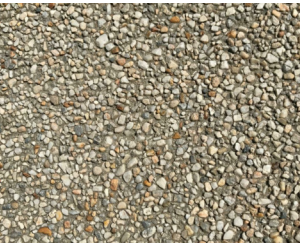

BELLS BEACH EXPOSED AGGREGATE


WANDANA LANDSCAPE GUIDELINE:
• OBJECTIVE IS TO COHESIVE BLEND OF INDEGENOUS VEGETATION AND OTHER LANDSCAPE ELEMENTS
• ALL PLANTATION MUST MINIMISE THE NEED FOR GARDEN WATERING
• NO TREE OR SHRUB WITH A MATURE HEIGHT OF GREATER THAN 3 METRES AND SHOULD BE PLANTED CLOSER THAN 2M TO THE HOUSE
• OWNER TO GET INTO CONTACT WITH CITY OF GREATER GEELONG TO OBTAIN ALLOWABLE VEGETATION.

PROPOSED RETURN FENCING - 1.8m(H)
CAPPED & LAPPED TIMBER PALING
FENCING WITH EXPOSED POSTS ON BOTH SIDES, AS PER DEVELOPERS GUIDELINES, BY OWNER.

EXPOSED AGGREGATE TO DRIVEWAY (44.7m2), BY OWNER. TOTAL: 44.7m2

LETTERBOX TO COMPLY WITH DESIGN GUIDELINES, BY OWNER

MONCRIEFF CRESCENT

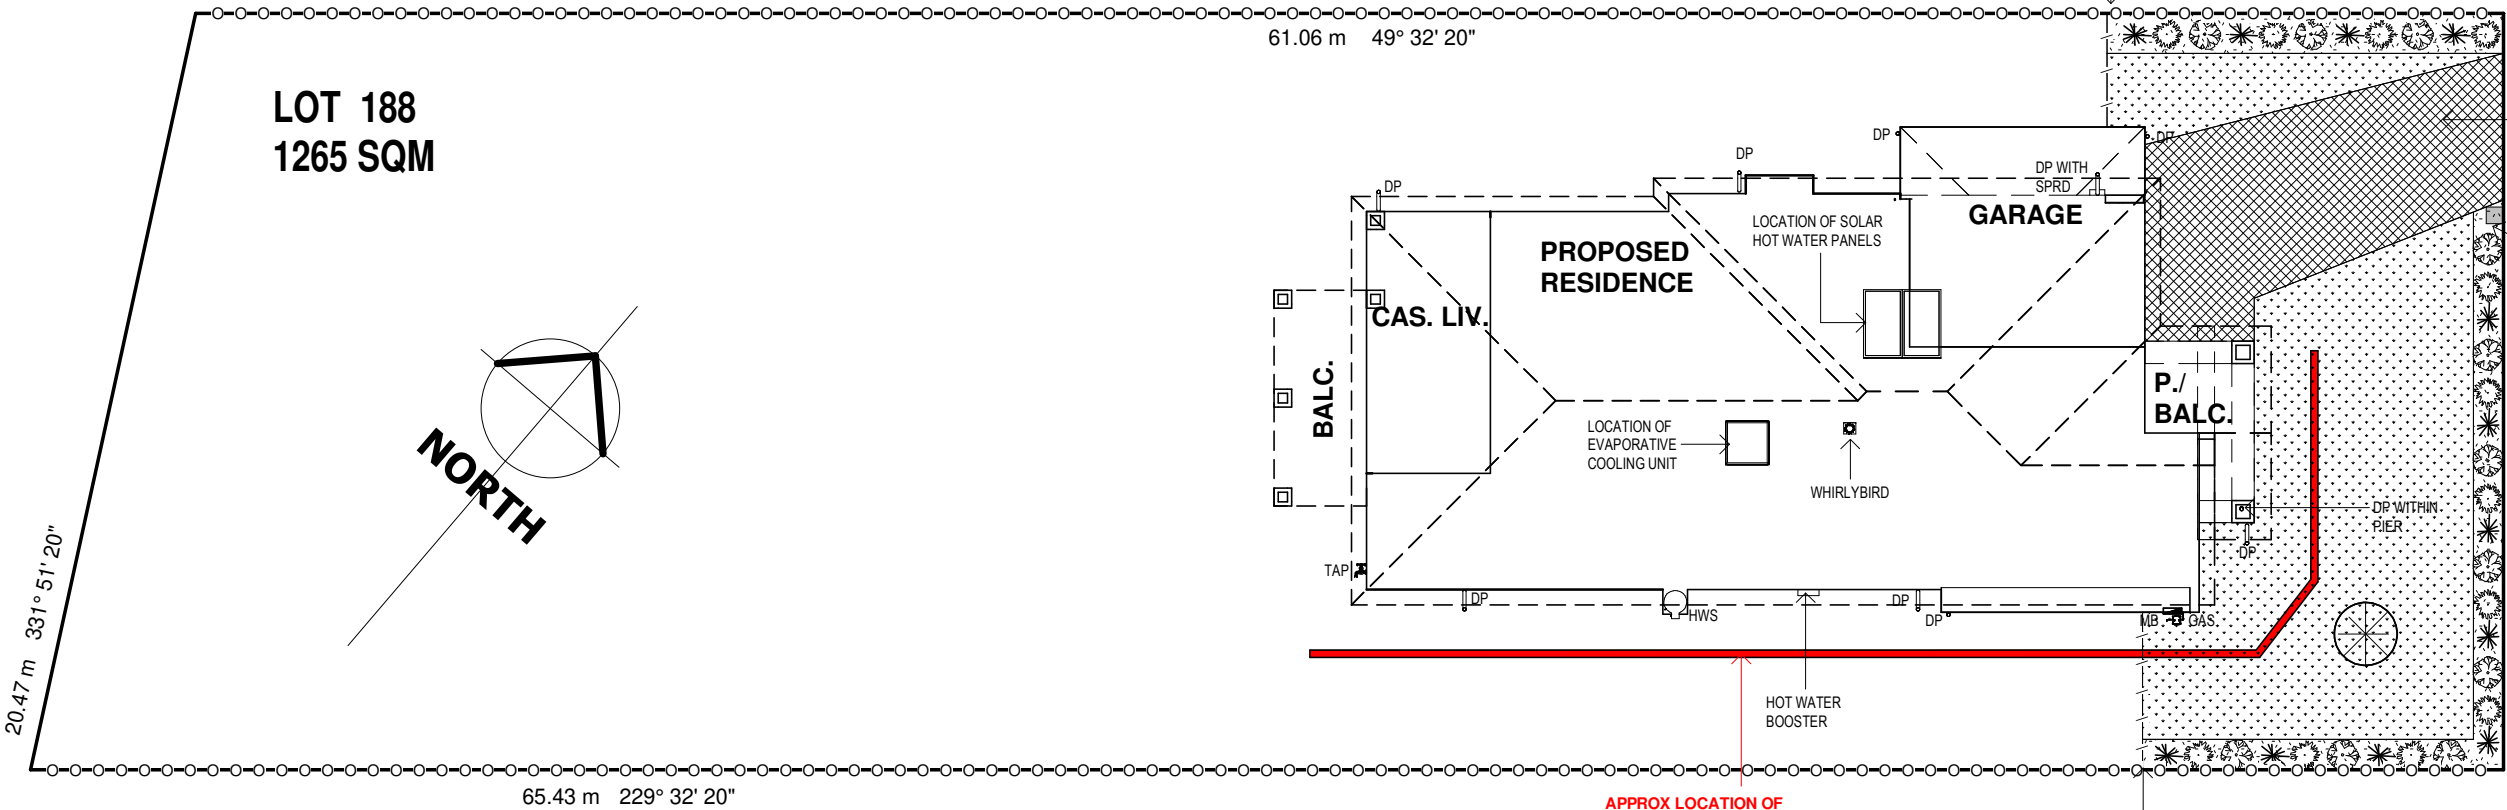

LANDSCAPE PLAN
SCALE 1 : 200

GENERAL NOTES:
- THE CONTRACTOR IS RESPONSIBLE FOR SETTING OUT AND CHECKING ALL LEVELS AND DIMENSIONS ON SITE PRIOR TO COMMENCING ANY SITE WORKS.
- FIGURED DIMENSIONS ARE TO TAKE PREFERENCE OVER SCALE
- DIMENSIONS TO STRUCTURAL TIMBERS & FACE OF BRICKS EXCLUDING BATTENS, PLASTERBOARD ETC.
- ALL DIMENSIONS ON PLAN ARE NOMINAL & MAY VARY TO ACTUAL SIZE
- PROVIDE LOCKS TO ALL OPENABLE WINDOWS & EXTERNAL SLIDING DOORS (KEYED ALIKE).
- MAN HOLE LOCATION MAY BE CHANGED DUE TO TRUSS LAYOUT.
- WINDOW AND DOOR FRAME SIZES ARE NOMINAL AND MAY VARY WITH LONG ISLAND HOMES APPROVED SUPPLIERS.

CLIENT

I / WE.....
CONFIRM THESE DRAWINGS ACCORD WITH OUR REQUIREMENTS AND AUTHORISE THEIR USE FOR NEXT STAGE PURPOSES.

SIGNED..... DATE.....
SIGNED..... DATE.....

SHEET CONTENT:
LANDSCAPE PLAN

HOUSE TYPE:
HAMPTON 490
MIN LOT WIDTH:
14M
PROPERTY ADDRESS:
188 MONCRIEFF CRESCENT
WANDANA HEIGHTS
CLIENT:
SANDEEP & IMMACOLATA BANSAL

NORTH:			FACADE:		SHEET NUMBER: 9.1	JOB NUMBER: 0188MON	
			SCALE: As indicated			JOB ISSUE:	
			DATE: 20.12.22			I	
REVISIONS	ISSUE	DATE	REVISION DESCRIPTION				INITIALS
	A	10.03.20	MASTER ISSUED				MP
	B	9.11.21	AMEDED CAS. LIV. BULKHEAD TO LIGHT WEIGHT				MP
	C	07.11.22	TENDER DRAWINGS, IDU & COLOUR DOC ADDED				CM
	D	09.11.22	COLOUR CHECK ADDED				CM
	E	10.11.22	ENERGY ADDED				CM
	F	17.11.22	DA RFI				BL
	G	30.11.22	ENG. ADDED, CONTRACT DRAWINGS ISSUED				BL
	H	20.12.22	B.S RFI & CONTRACT QUOTE AMENDMENT				BL
	I	21.12.22	AMENDED ENEGRY ADDED				BL





LONG ISLAND HOMES



ISLANDER

Long Island Homes Pty. Ltd.
PO BOX 6269
Point Cook, Vic 3030
p. 61 3 9369 6486 (1800 604 011)
f. 61 3 9369 0994
email: admin@longislandhomes.com.au
www.longislandhomes.com.au
© Copyright
THIS DESIGN & DRAWING SHALL REMAIN THE INTELLECTUAL PROPERTY OF LONG ISLAND HOMES PTY. LTD. AND SHALL NOT BE COPIED IN WHOLE OR PART WITHOUT WRITTEN CONSENT FROM LONG ISLAND HOMES PTY LTD.
DB NUMBER: CDB - U 58094

21/12/2022 4:21:37 PM J:\LONG ISLAND JOBS\188 Moncrieff Crescent, Wandana Heights\DRAWING\0188MON_REV 1.rvt

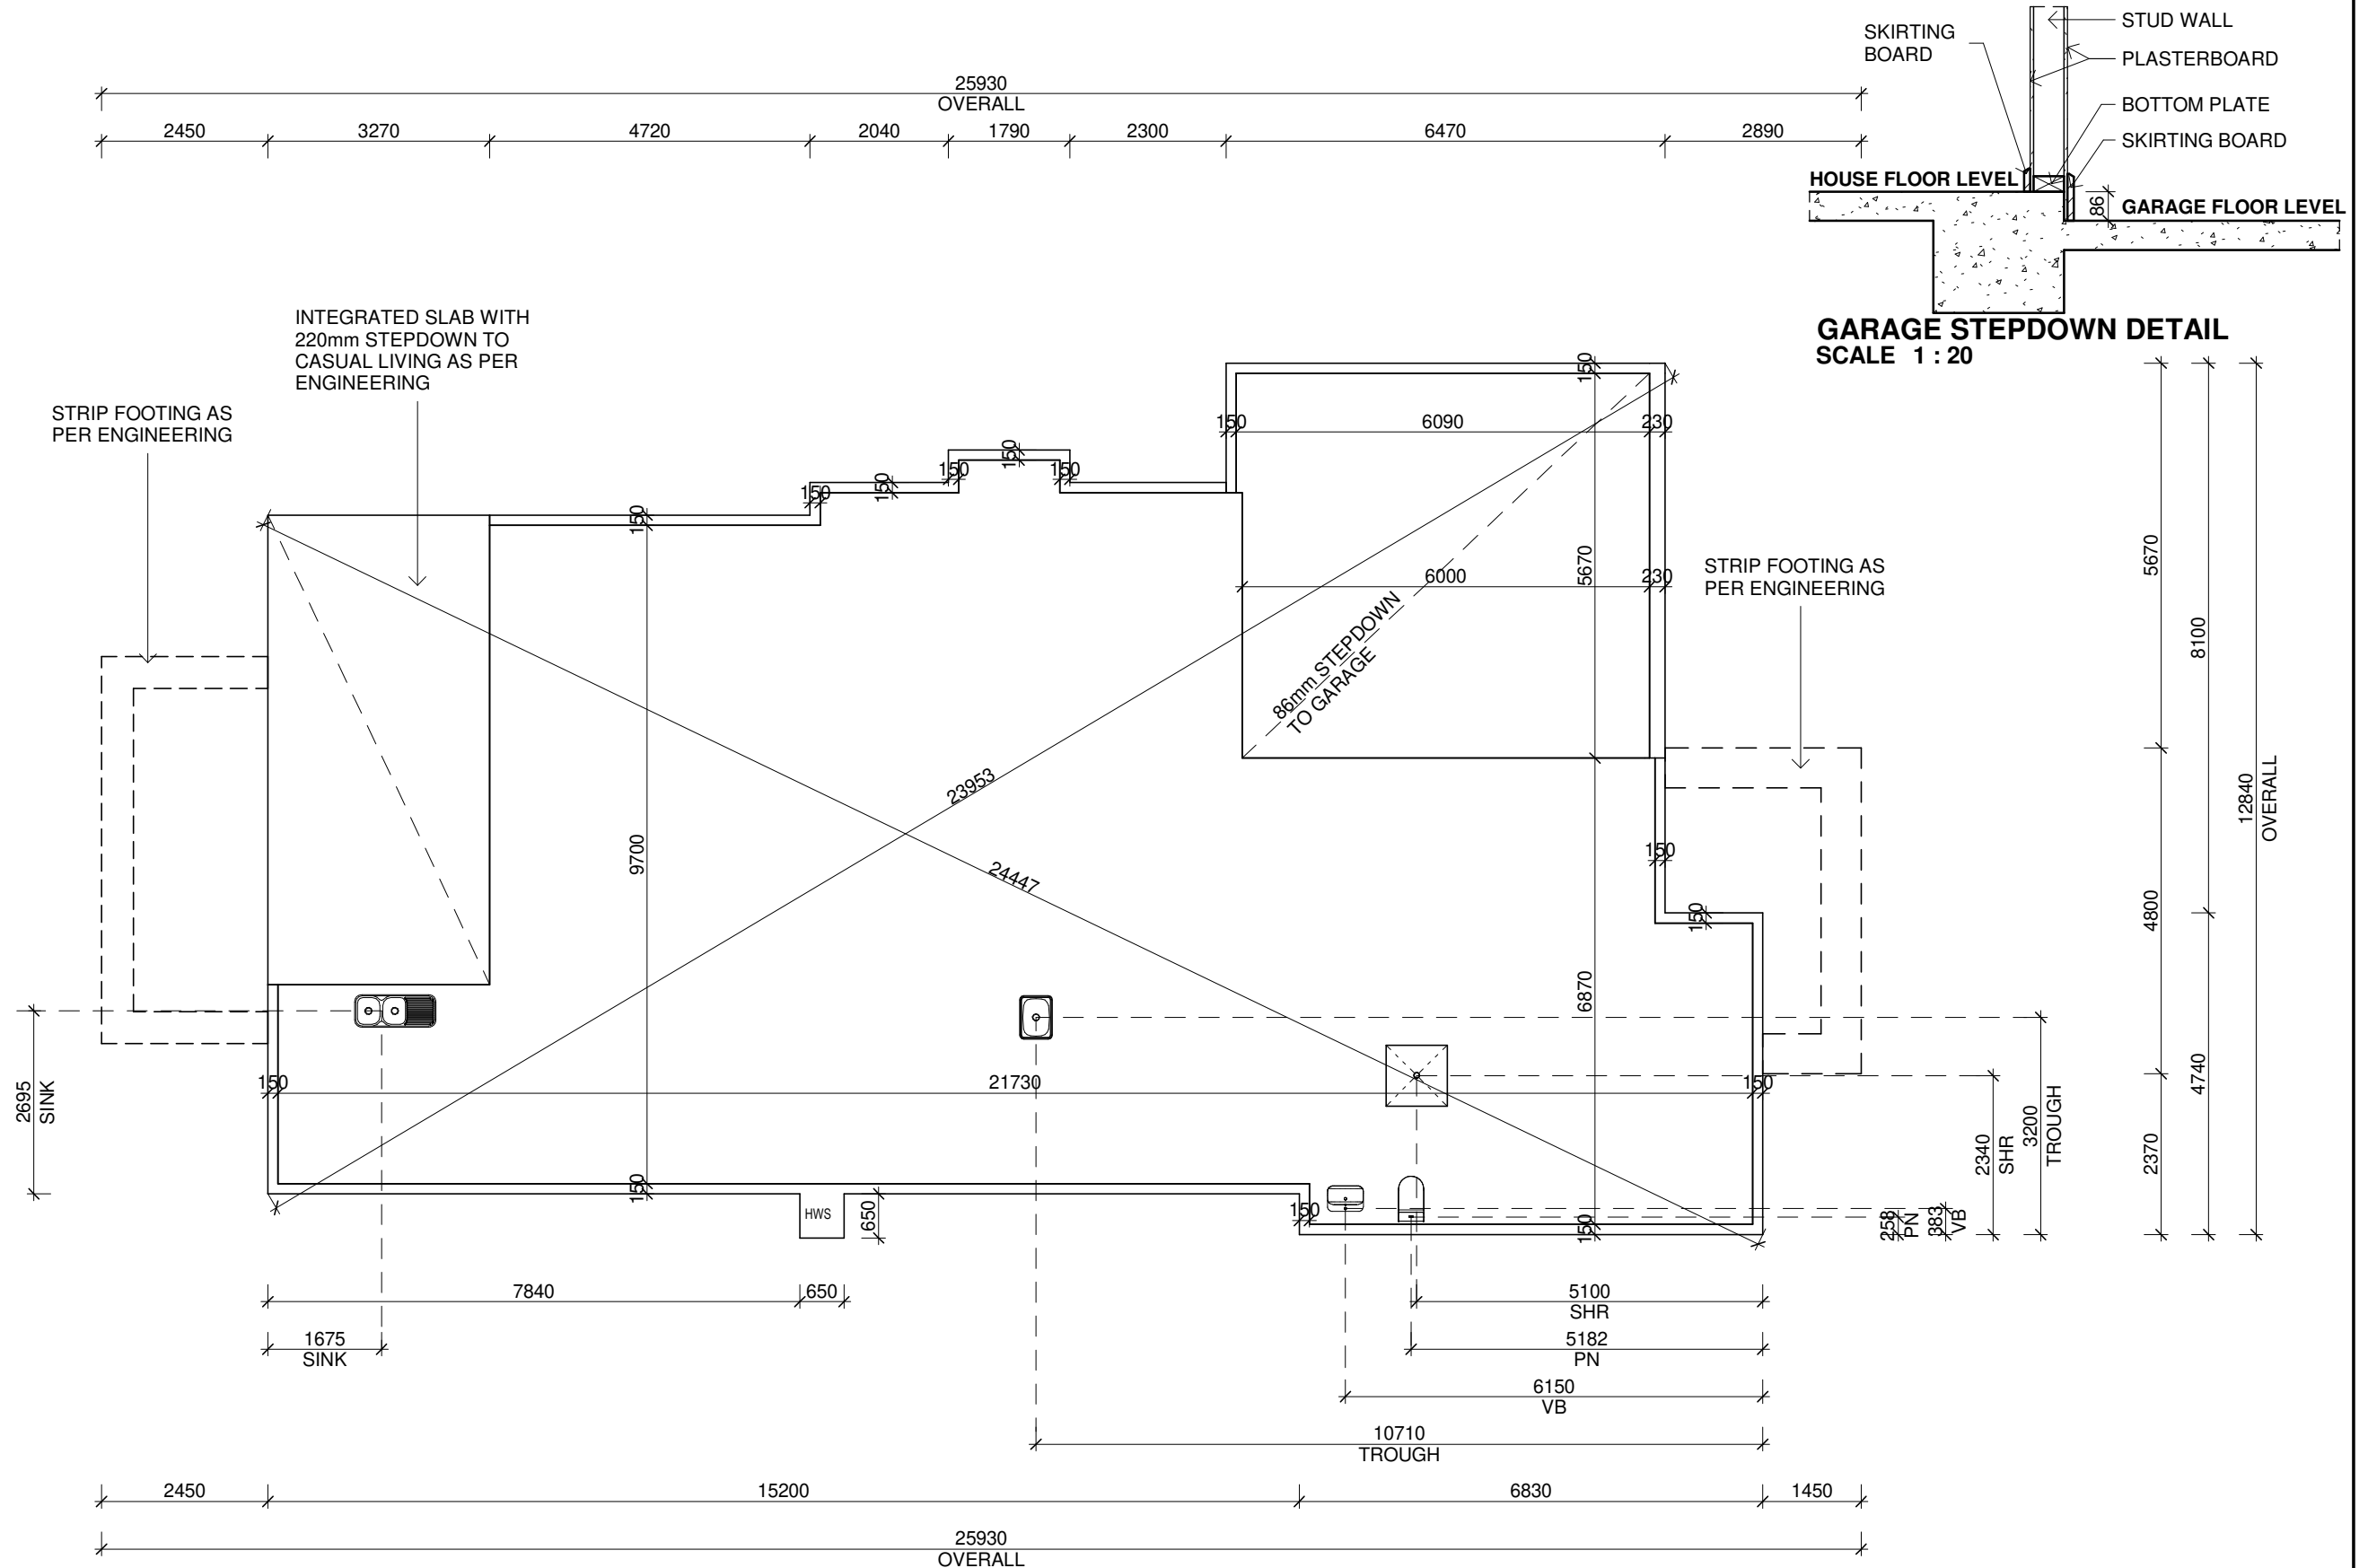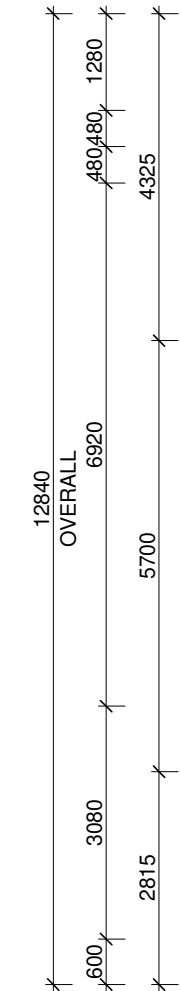

SLAB PLAN
SCALE 1 : 100



ISLANDER

Long Island Homes Pty. Ltd.
PO BOX 6269
Point Cook, Vic 3030
p. 61 3 9369 6486 (1800 604 011)
f. 61 3 9369 0994
email: admin@longislandhomes.com.au
www.longislandhomes.com.au

© Copyright
THIS DESIGN & DRAWING SHALL REMAIN THE INTELLECTUAL PROPERTY OF
LONG ISLAND HOMES PTY. LTD. AND SHALL NOT BE COPIED IN WHOLE OR
PART WITHOUT WRITTEN CONSENT FROM LONG ISLAND HOMES PTY LTD.
DB NUMBER: CDB - U 58094

GENERAL NOTES:

- THE CONTRACTOR IS RESPONSIBLE FOR SETTING OUT AND CHECKING ALL LEVELS AND DIMENSIONS ON SITE PRIOR TO COMMENCING ANY SITE WORKS.
- FIGURED DIMENSIONS ARE TO TAKE PREFERENCE OVER SCALE
- DIMENSIONS TO STRUCTURAL TIMBERS & FACE OF BRICKS EXCLUDING BATTENS, PLASTERBOARD ETC.
- ALL DIMENSIONS ON PLAN ARE NOMINAL & MAY VARY TO ACTUAL SIZE
- PROVIDE LOCKS TO ALL OPENABLE WINDOWS & EXTERNAL SLIDING DOORS (KEYED ALIKE).
- MAN HOLE LOCATION MAY BE CHANGED DUE TO TRUSS LAYOUT.
- WINDOW AND DOOR FRAME SIZES ARE NOMINAL AND MAY VARY WITH LONG ISLAND HOMES APPROVED SUPPLIERS.

CLIENT

I / WE.....

CONFIRM THESE DRAWINGS ACCORD WITH OUR REQUIREMENTS AND AUTHORISE THEIR USE FOR NEXT STAGE PURPOSES.

SIGNED..... DATE.....

SIGNED..... DATE.....

SHEET CONTENT:

SLAB LAYOUT PLAN

HOUSE TYPE:
HAMPTON 490

MIN LOT WIDTH:
14M

PROPERTY ADDRESS:
188 MONCRIEFF CRESCENT
WANDANA HEIGHTS

CLIENT:
SANDEEP & IMMACOLATA BANSAL

NORTH:

FACADE:

SCALE: As indicated

DATE: 20.12.22

SHEET NUMBER:

10.1





JOB NUMBER:

0188MON

JOB ISSUE:

I

REVISIONS	ISSUE	DATE	REVISION DESCRIPTION	INITIALS
A	10.03.20		MASTER ISSUED	MP
B	9.11.21		AMEDED CAS. LIV. BULKHEAD TO LIGHT WEIGHT	MP
C	07.11.22		TENDER DRAWINGS, IDU & COLOUR DOC ADDED	CM
D	09.11.22		COLOUR CHECK ADDED	CM
E	10.11.22		ENERGY ADDED	CM
F	17.11.22		DA RFI	BL
G	30.11.22		ENG. ADDED, CONTRACT DRAWINGS ISSUED	BL
H	20.12.22		B.S RFI & CONTRACT QUOTE AMENDMENT	BL
I	21.12.22		AMEDED ENEGRY ADDED	BL

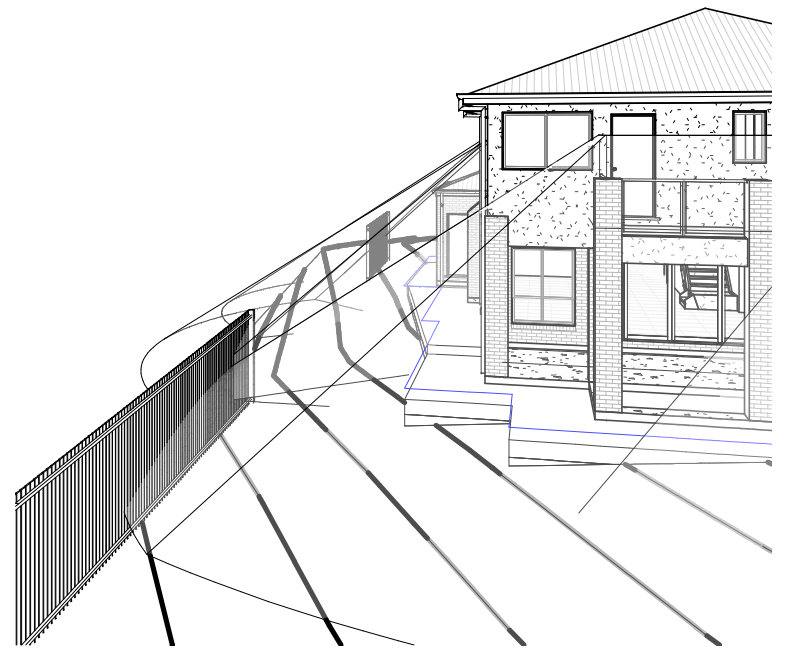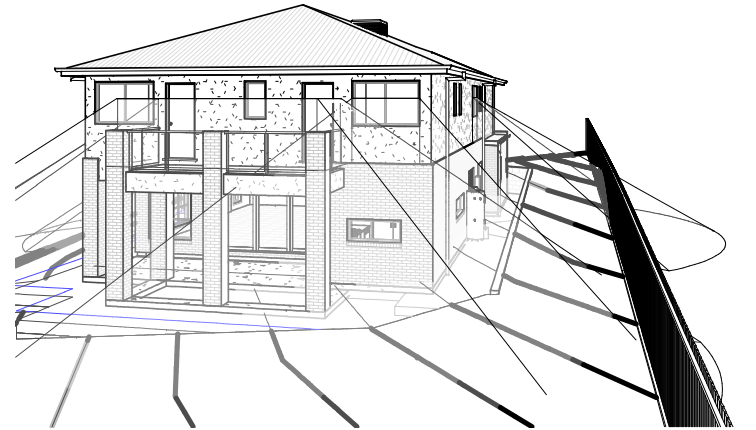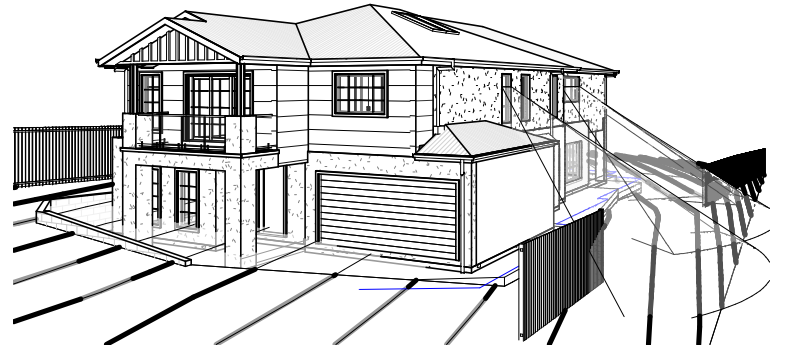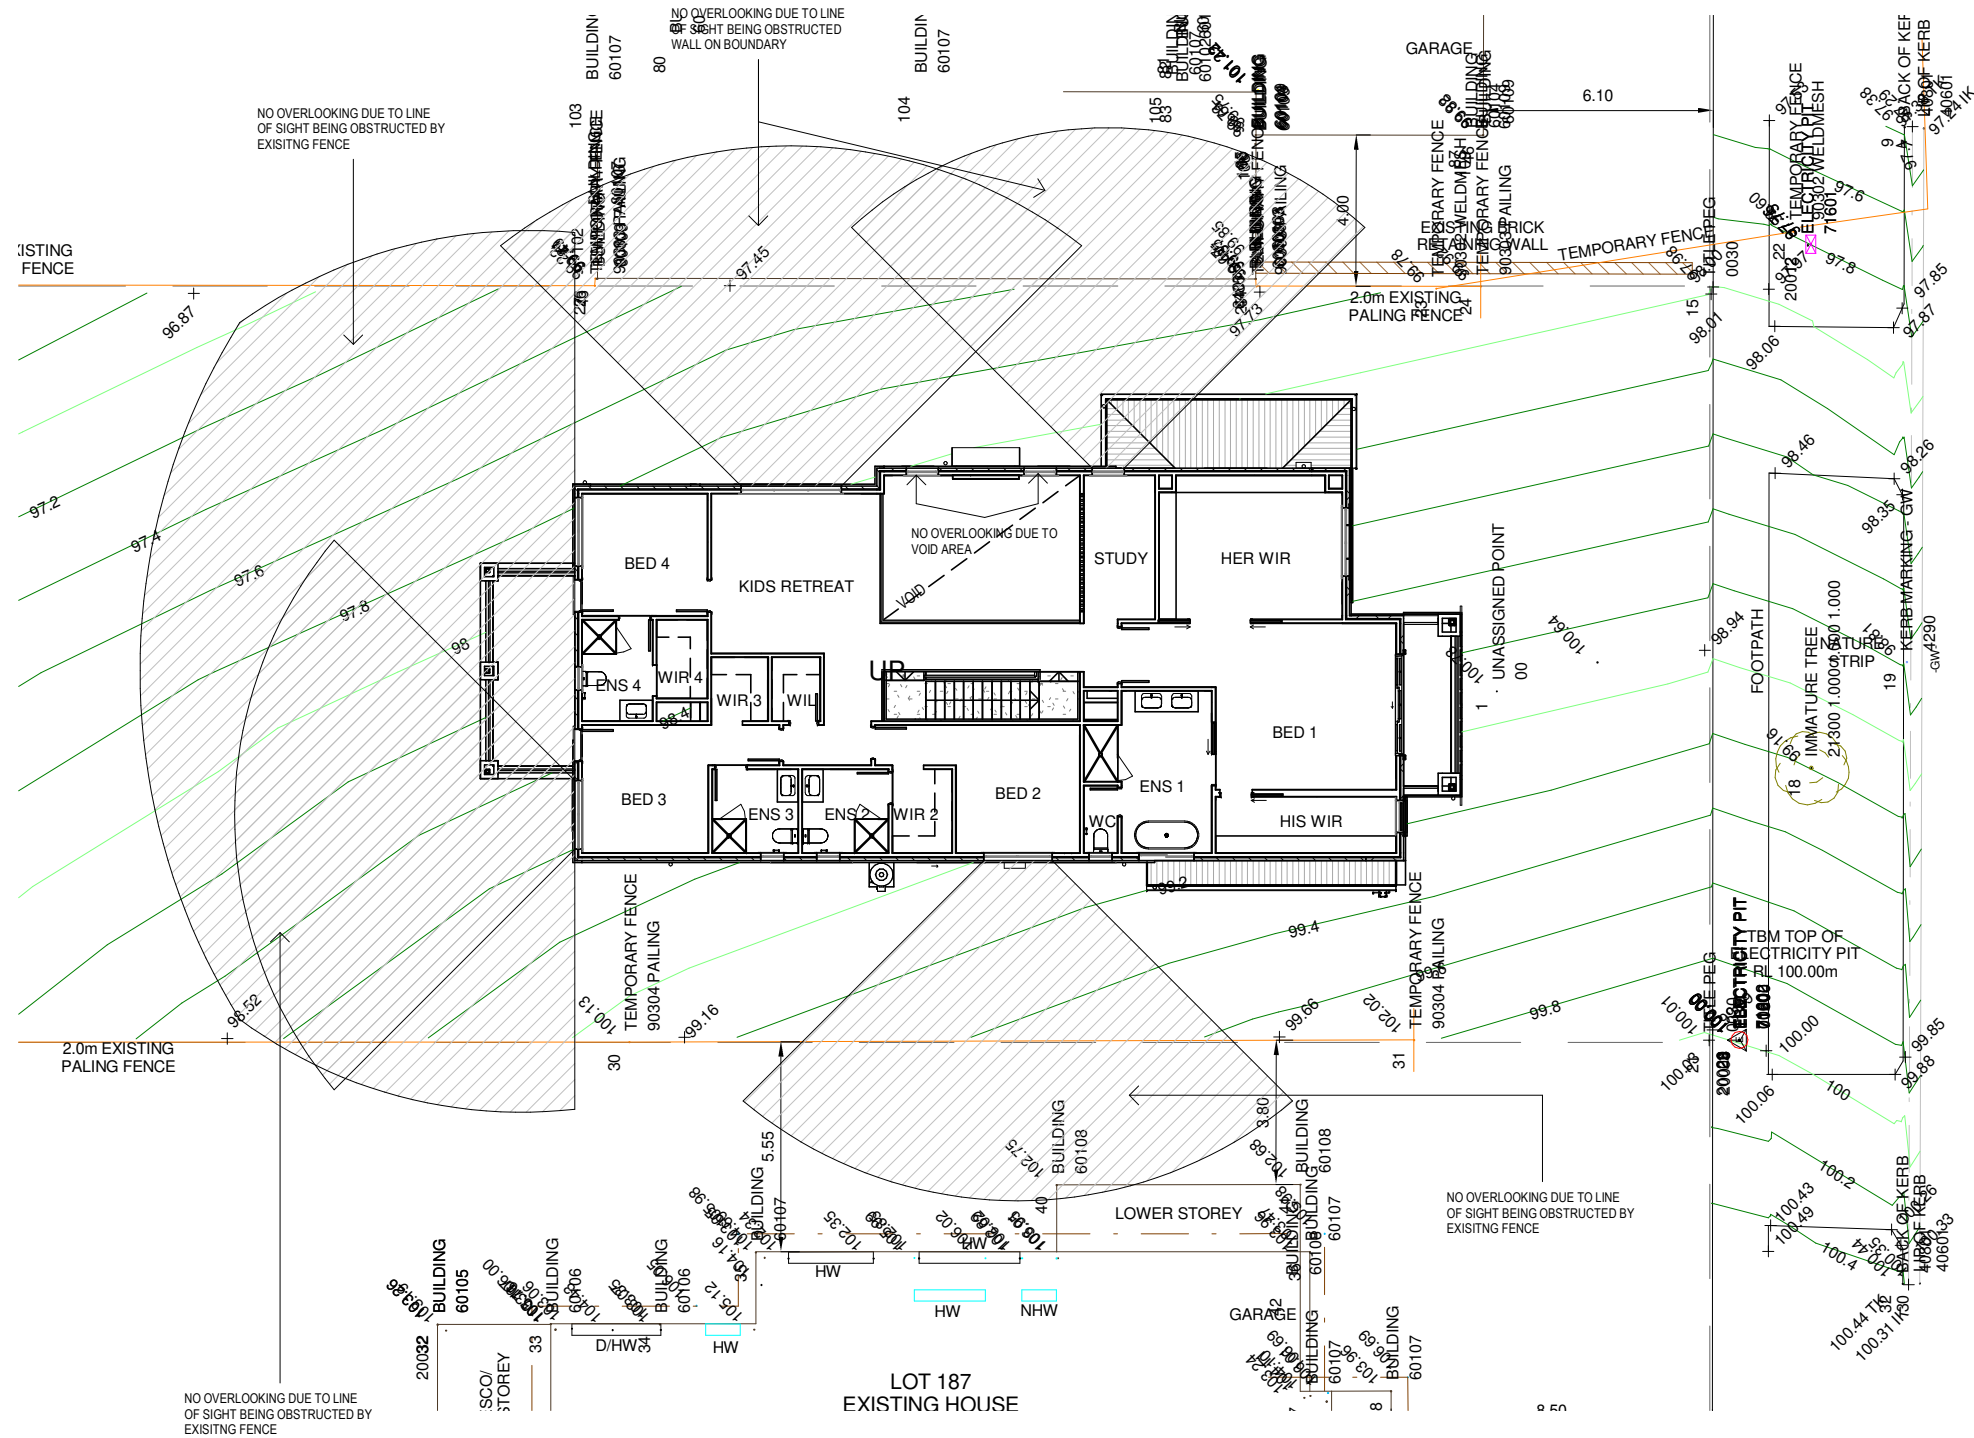

OVERLOOKING

SCALE 1 : 200



ISLANDER

Long Island Homes Pty. Ltd.
PO BOX 6269
Point Cook, Vic 3030
p. 61 3 9369 6486 (1800 604 011)
f. 61 3 9369 0994
email: admin@longislandhomes.com.au
www.longislandhomes.com.au

© Copyright
THIS DESIGN & DRAWING SHALL REMAIN THE INTELLECTUAL PROPERTY OF
LONG ISLAND HOMES PTY. LTD. AND SHALL NOT BE COPIED IN WHOLE OR
PART WITHOUT WRITTEN CONSENT FROM LONG ISLAND HOMES PTY LTD.
DB NUMBER: CDB - U 58094

GENERAL NOTES:

- THE CONTRACTOR IS RESPONSIBLE FOR SETTING OUT AND CHECKING ALL LEVELS AND DIMENSIONS ON SITE PRIOR TO COMMENCING ANY SITE WORKS.
- FIGURED DIMENSIONS ARE TO TAKE PREFERENCE OVER SCALE
- DIMENSIONS TO STRUCTURAL TIMBERS & FACE OF BRICKS EXCLUDING BATTENS, PLASTERBOARD ETC.
- ALL DIMENSIONS ON PLAN ARE NOMINAL & MAY VARY TO ACTUAL SIZE
- PROVIDE LOCKS TO ALL OPENABLE WINDOWS & EXTERNAL SLIDING DOORS (KEYED ALIKE).
- MAN HOLE LOCATION MAY BE CHANGED DUE TO TRUSS LAYOUT.
- WINDOW AND DOOR FRAME SIZES ARE NOMINAL AND MAY VARY WITH LONG ISLAND HOMES APPROVED SUPPLIERS.

CLIENT

I / WE.....

CONFIRM THESE DRAWINGS ACCORD WITH OUR REQUIREMENTS AND AUTHORISE THEIR USE FOR NEXT STAGE PURPOSES.

SIGNED..... DATE.....

SIGNED..... DATE.....

SIGN OFF

SHEET CONTENT:

OVERLOOKING

HOUSE TYPE:
HAMPTON 490

MIN LOT WIDTH:
14M

PROPERTY ADDRESS:
188 MONCRIEFF CRESCENT
WANDANA HEIGHTS

CLIENT:

SANDEEP & IMMACOLATA BANSAL

NORTH:

FACADE:

SCALE: 1 : 200

DATE: 20.12.22

SHEET NUMBER:

11.1

JOB NUMBER:

0188MON

JOB ISSUE:

1

REVISIONS

ISSUE	DATE	REVISION DESCRIPTION	INITIALS
H	20.12.22	B.S RFI & CONTRACT QUOTE AMENDMENT	BL
I	21.12.22	AMENDED ENEGRY ADDED	BL

21/12/2022 4:21:41 PM J:\LONG ISLAND JOBS\188 Moncrieff Crescent, Wandana Heights\DRAWING\0188MON_REV 1.rvt

RESERVE No.1

PROPOSED SHADOW
EXISTING FENCE

LOT 188A
HOUSE UNDER
CONSTRUCTION
SINGLE STOREY
EAVE HT 101.23
RIDGE HT 101.42
(LOCK UP STAGE)
AS OF 21.10.22

GARAGE

PORCH

GARAGE

EXISTING BRICK
RETAINING WALL

TEMPORARY FENCE

2.0m EXISTING
PALING FENCE

2.0m EXISTING
PALING FENCE

2.0m EXISTING
PALING FENCE

10am SHADOW
SCALE 1 : 200

LOT 187
EXISTING HOUSE
DOUBLE STOREY
EAVE HT 106.05
RIDGE HT 108.86
PORCH EAVE HT 106.70

LOWER STOREY

UPPER STOREY

PORCH/
BALCONY

TBM TOP OF
ELECTRICITY PIT
RL 100.00m

FOOTPATH

NATURE
STRIP

GENERAL NOTES:

- THE CONTRACTOR IS RESPONSIBLE FOR SETTING OUT AND CHECKING ALL LEVELS AND DIMENSIONS ON SITE PRIOR TO COMMENCING ANY SITE WORKS.
- FIGURED DIMENSIONS ARE TO TAKE PREFERENCE OVER SCALE
- DIMENSIONS TO STRUCTURAL TIMBERS & FACE OF BRICKS EXCLUDING BATTENS, PLASTERBOARD ETC.
- ALL DIMENSIONS ON PLAN ARE NOMINAL & MAY VARY TO ACTUAL SIZE
- PROVIDE LOCKS TO ALL OPENABLE WINDOWS & EXTERNAL SLIDING DOORS (KEYED ALIKE).
- MAN HOLE LOCATION MAY BE CHANGED DUE TO TRUSS LAYOUT.
- WINDOW AND DOOR FRAME SIZES ARE NOMINAL AND MAY VARY WITH LONG ISLAND HOMES APPROVED SUPPLIERS.

CLIENT

I / WE.....

CONFIRM THESE DRAWINGS ACCORD WITH OUR REQUIREMENTS AND AUTHORISE THEIR USE FOR NEXT STAGE PURPOSES.

SIGNED..... DATE.....

SIGNED..... DATE.....

SHEET CONTENT:

10am SHADOW

HOUSE TYPE:
HAMPTON 490

MIN LOT WIDTH:
14M

PROPERTY ADDRESS:
188 MONCRIEFF CRESCENT
WANDANA HEIGHTS

CLIENT:

SANDEEP & IMMACOLATA BANSAL

NORTH:

FACADE:

SCALE: 1 : 200

DATE: 20.12.22

SHEET NUMBER:

11.3

JOB NUMBER:

0188MON

JOB ISSUE:

1


ISSUE	DATE	REVISION DESCRIPTION	INITIALS
H	20.12.22	B.S RFI & CONTRACT QUOTE AMENDMENT	BL
I	21.12.22	AMENDED ENERGY ADDED	BL



ISLANDER

Long Island Homes Pty. Ltd.
PO BOX 6269
Point Cook, Vic 3030
p. 61 3 9369 6486 (1800 604 011)
f. 61 3 9369 0994
email: admin@longislandhomes.com.au
www.longislandhomes.com.au

© Copyright
THIS DESIGN & DRAWING SHALL REMAIN THE INTELLECTUAL PROPERTY OF
LONG ISLAND HOMES PTY. LTD. AND SHALL NOT BE COPIED IN WHOLE OR
PART WITHOUT WRITTEN CONSENT FROM LONG ISLAND HOMES PTY LTD.
DB NUMBER: CDB - U 58094

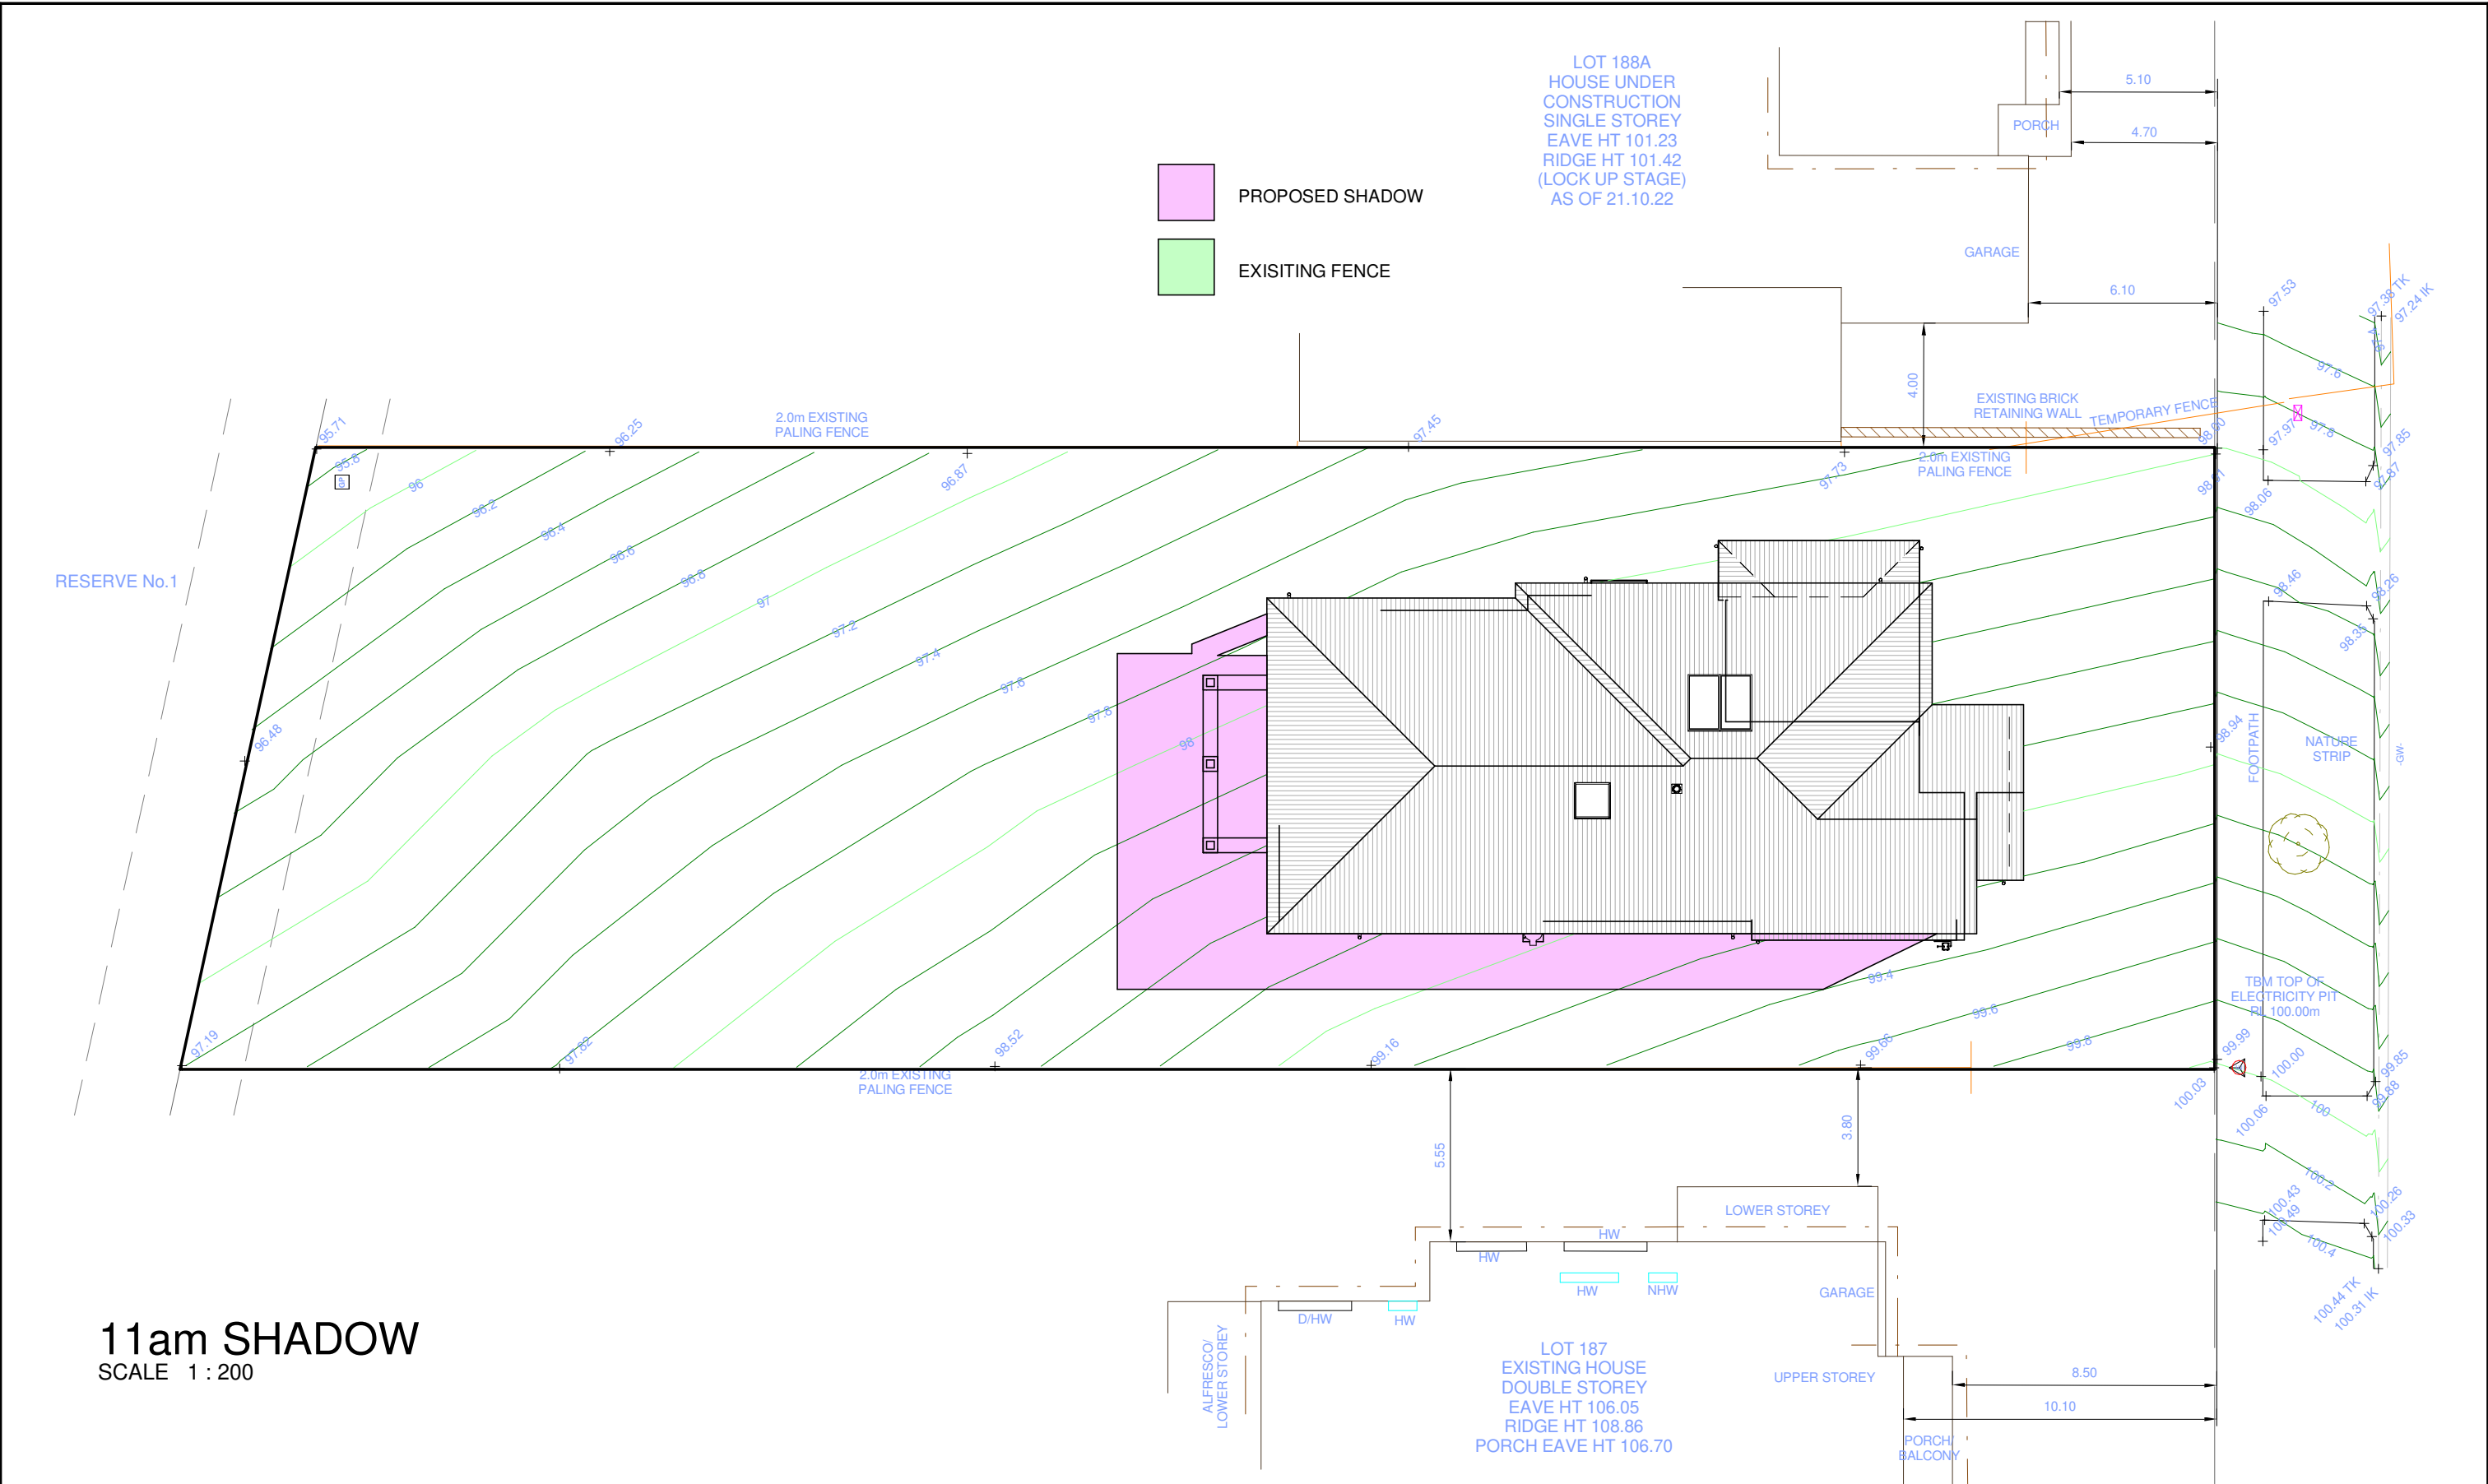

11am SHADOW
SCALE 1 : 200



Long Island Homes Pty. Ltd.
PO BOX 6269
Point Cook, Vic 3030
p. 61 3 9369 6486 (1800 604 011)
f. 61 3 9369 0994
email: admin@longislandhomes.com.au
www.longislandhomes.com.au

© Copyright
THIS DESIGN & DRAWING SHALL REMAIN THE INTELLECTUAL PROPERTY OF
LONG ISLAND HOMES PTY. LTD. AND SHALL NOT BE COPIED IN WHOLE OR
PART WITHOUT WRITTEN CONSENT FROM LONG ISLAND HOMES PTY LTD.
DB NUMBER: CDB - U 58094

GENERAL NOTES:

- THE CONTRACTOR IS RESPONSIBLE FOR SETTING OUT AND CHECKING ALL LEVELS AND DIMENSIONS ON SITE PRIOR TO COMMENCING ANY SITE WORKS.
- FIGURED DIMENSIONS ARE TO TAKE PREFERENCE OVER SCALE
- DIMENSIONS TO STRUCTURAL TIMBERS & FACE OF BRICKS EXCLUDING BATTENS, PLASTERBOARD ETC.
- ALL DIMENSIONS ON PLAN ARE NOMINAL & MAY VARY TO ACTUAL SIZE
- PROVIDE LOCKS TO ALL OPENABLE WINDOWS & EXTERNAL SLIDING DOORS (KEYED ALIKE).
- MAN HOLE LOCATION MAY BE CHANGED DUE TO TRUSS LAYOUT.
- WINDOW AND DOOR FRAME SIZES ARE NOMINAL AND MAY VARY WITH LONG ISLAND HOMES APPROVED SUPPLIERS.

CLIENT

I / WE.....

CONFIRM THESE DRAWINGS ACCORD WITH OUR
REQUIREMENTS AND AUTHORISE THEIR USE FOR
NEXT STAGE PURPOSES.

SIGNED..... DATE.....

SIGNED..... DATE.....

SHEET CONTENT:

11am SHADOW

HOUSE TYPE:
HAMPTON 490

MIN LOT WIDTH:	14M
----------------	-----

PROPERTY ADDRESS:
188 MONCRIEFF CRESCENT
WANDANA HEIGHTS

CLIENT: **SANDEEP & IMMACOLATA BANSAL**

NORTH:	
--------	--

FACADE:

SCALE: 1 : 200

DATE: 20.12.22

SHEET NUMBER:

11.4


JOB NUMBER:

0188MON

JOB ISSUE:

1

	ISSUE	DATE	REVISION DESCRIPTION	INITIALS
REVISED	H	20.12.22	B.S RFI & CONTRACT QUOTE AMENDMENT	BL
	I	21.12.22	AMENDED ENERGY ADDED	BL

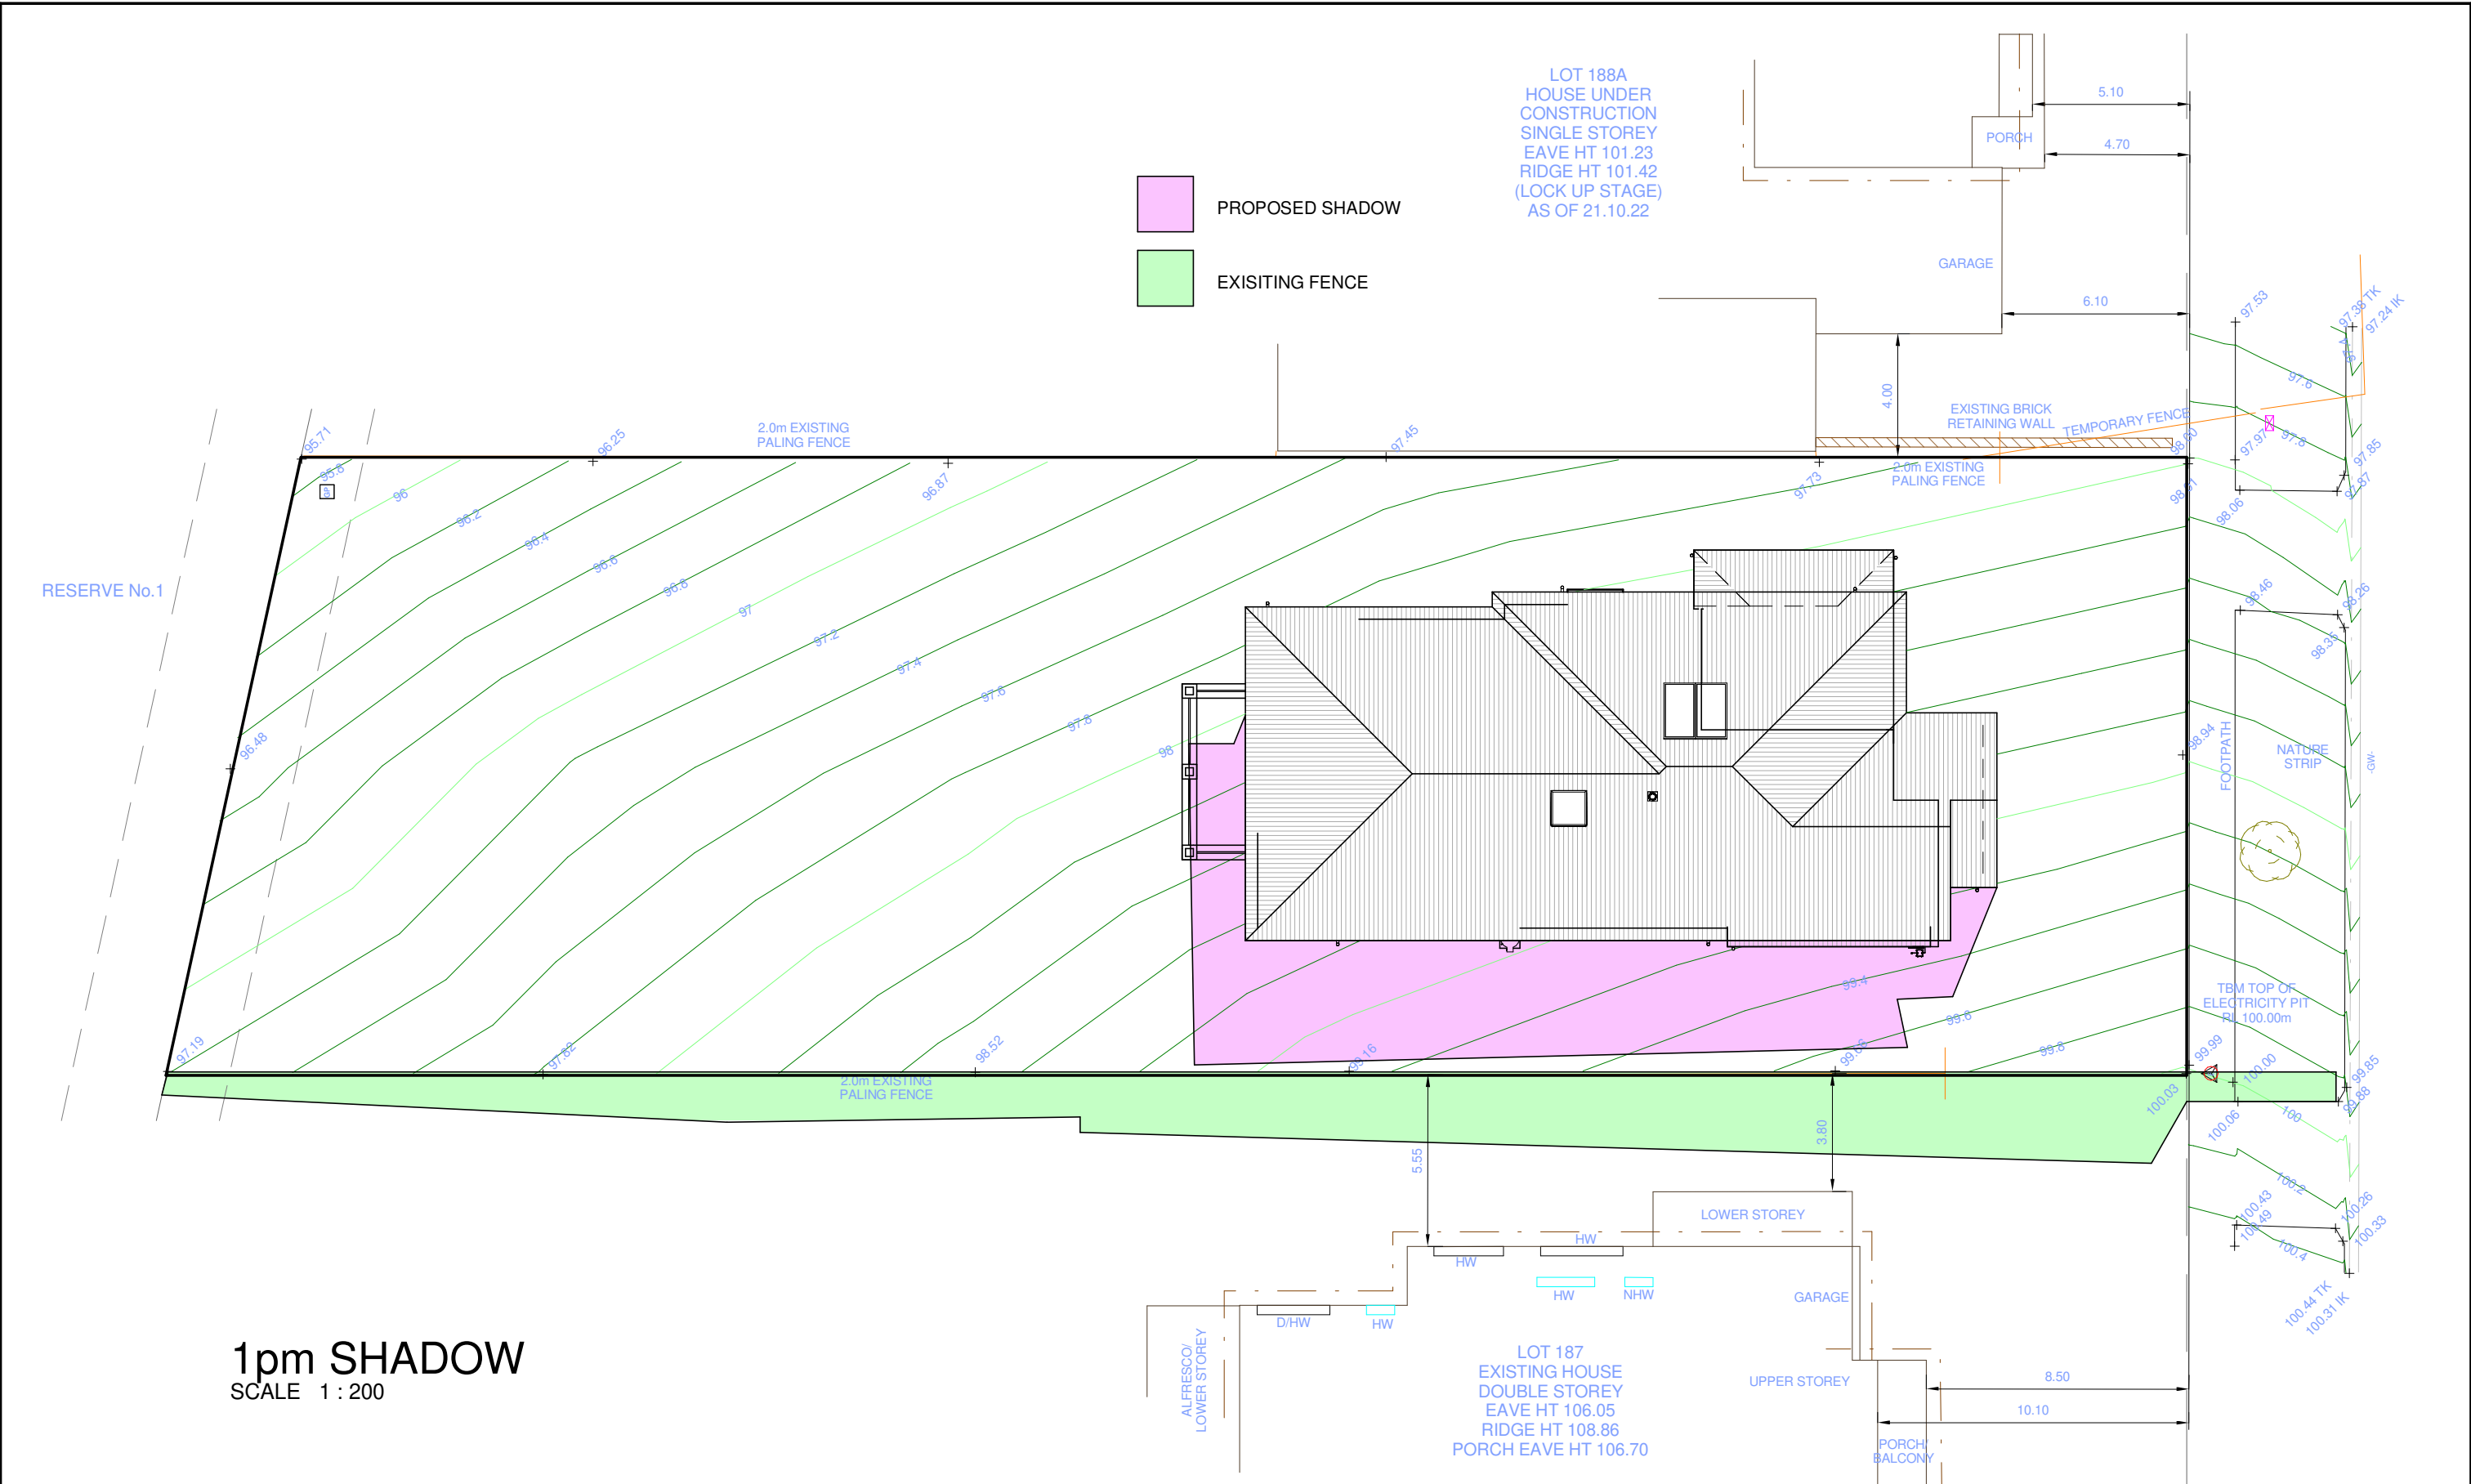

ISLANDER

Long Island Homes Pty. Ltd.
PO BOX 6269
Point Cook, Vic 3030
p. 61 3 9369 6486 (1800 604 011)
f. 61 3 9369 0994
mail: admin@longislandhomes.com.au
www.longislandhomes.com.au

© Copyright
THIS DESIGN & DRAWING SHALL REMAIN THE INTELLECTUAL PROPERTY OF
LONG ISLAND HOMES PTY. LTD. AND SHALL NOT BE COPIED IN WHOLE OR
PART WITHOUT WRITTEN CONSENT FROM LONG ISLAND HOMES PTY LTD.
DB NUMBER: CDB - U 58094

GENERAL NOTES:

- THE CONTRACTOR IS RESPONSIBLE FOR SETTING OUT AND CHECKING ALL LEVELS AND DIMENSIONS ON SITE PRIOR TO COMMENCING ANY SITE WORKS.
- FIGURED DIMENSIONS ARE TO TAKE PREFERENCE OVER SCALE
- DIMENSIONS TO STRUCTURAL TIMBERS & FACE OF BRICKS EXCLUDING BATTENS, PLASTERBOARD ETC.
- ALL DIMENSIONS ON PLAN ARE NOMINAL & MAY VARY TO ACTUAL SIZE
- PROVIDE LOCKS TO ALL OPENABLE WINDOWS & EXTERNAL SLIDING DOORS (KEYED ALIKE).
- MAN HOLE LOCATION MAY BE CHANGED DUE TO TRUSS LAYOUT.
- WINDOW AND DOOR FRAME SIZES ARE NOMINAL AND MAY VARY WITH LONG ISLAND HOMES APPROVED SUPPLIERS.

CLIENT

I / WE.....

CONFIRM THESE DRAWINGS ACCORD WITH OUR
REQUIREMENTS AND AUTHORISE THEIR USE FOR
NEXT STAGE PURPOSES.

SIGNED..... DATE.....

SIGNED..... DATE.....

SHEET CONTENT:

1 pm SHADOW

HOUSE TYPE:
HAMPTON 490

MIN LOT WIDTH:	14M
----------------	-----

PROPERTY ADDRESS:
188 MONCRIEFF CRESCENT
WANDANA HEIGHTS

CLIENT: **SANDEEP & IMMACOLATA BANSAL**

	NORTH:
--	--------

FACADE:

SCALE: 1 : 200

DATE: 20.12.22

SHEET NUMBER:

11.6

JOB NUMBER:

0188MON

JOB ISSUE:

11

[illegible]



© Copyright
THIS DESIGN & DRAWING SHALL REMAIN THE INTELLECTUAL PROPERTY OF
LONG ISLAND HOMES PTY. LTD. AND SHALL NOT BE COPIED IN WHOLE OR
PART WITHOUT WRITTEN CONSENT FROM LONG ISLAND HOMES PTY LTD.
DB NUMBER: CDB - U 58094

- THE CONTRACTOR IS RESPONSIBLE FOR SETTING OUT AND CHECKING ALL LEVELS AND DIMENSIONS ON SITE PRIOR TO COMMENCING ANY SITE WORKS.
- FIGURED DIMENSIONS ARE TO TAKE PREFERENCE OVER SCALE
- DIMENSIONS TO STRUCTURAL TIMBERS & FACE OF BRICKS EXCLUDING BATTENS, PLASTERBOARD ETC.
- ALL DIMENSIONS ON PLAN ARE NOMINAL & MAY VARY TO ACTUAL SIZE
- PROVIDE LOCKS TO ALL OPENABLE WINDOWS & EXTERNAL SLIDING DOORS (KEYED ALIKE).
- MAN HOLE LOCATION MAY BE CHANGED DUE TO TRUSS LAYOUT.
- WINDOW AND DOOR FRAME SIZES ARE NOMINAL AND MAY VARY WITH LONG ISLAND HOMES APPROVED SUPPLIERS.

SIGNED..... DATE.....

CLIENT: **SANDEEP & IMMACOLATA BANSAL**

	ISSUE	DATE	REVISION DESCRIPTION	INITIALS
REVISED	H	20.12.22	B.S RFI & CONTRACT QUOTE AMENDMENT	BL
	I	21.12.22	AMENDED ENEGRY ADDED	BL

21/12/2022 4:21:42 PM J:\LONG ISLAND JOBS\188 Moncrieff Crescent, Wandana Heights\DRAWING\0188MON_REV 1.rvt

RESERVE No.1

3pm SHADOW
SCALE 1 : 200



ISLANDER

Long Island Homes Pty. Ltd.
PO BOX 6269
Point Cook, Vic 3030
p. 61 3 9369 6486 (1800 604 011)
f. 61 3 9369 0994
email: admin@longislandhomes.com.au
www.longislandhomes.com.au

© Copyright
THIS DESIGN & DRAWING SHALL REMAIN THE INTELLECTUAL PROPERTY OF
LONG ISLAND HOMES PTY. LTD. AND SHALL NOT BE COPIED IN WHOLE OR
PART WITHOUT WRITTEN CONSENT FROM LONG ISLAND HOMES PTY LTD.
DB NUMBER: CDB - U 58094

GENERAL NOTES:

- THE CONTRACTOR IS RESPONSIBLE FOR SETTING OUT AND CHECKING ALL LEVELS AND DIMENSIONS ON SITE PRIOR TO COMMENCING ANY SITE WORKS.
- FIGURED DIMENSIONS ARE TO TAKE PREFERENCE OVER SCALE
- DIMENSIONS TO STRUCTURAL TIMBERS & FACE OF BRICKS EXCLUDING BATTENS, PLASTERBOARD ETC.
- ALL DIMENSIONS ON PLAN ARE NOMINAL & MAY VARY TO ACTUAL SIZE
- PROVIDE LOCKS TO ALL OPENABLE WINDOWS & EXTERNAL SLIDING DOORS (KEYED ALIKE).
- MAN HOLE LOCATION MAY BE CHANGED DUE TO TRUSS LAYOUT.
- WINDOW AND DOOR FRAME SIZES ARE NOMINAL AND MAY VARY WITH LONG ISLAND HOMES APPROVED SUPPLIERS.

CLIENT

I / WE.....

SIGN OFF

CONFIRM THESE DRAWINGS ACCORD WITH OUR REQUIREMENTS AND AUTHORISE THEIR USE FOR NEXT STAGE PURPOSES.

SIGNED..... DATE.....

SIGNED..... DATE.....

SHEET CONTENT:

3pm SHADOW

HOUSE TYPE: HAMPTON 490 MIN LOT WIDTH: 14M

PROPERTY ADDRESS:
188 MONCRIEFF CRESCENT
WANDANA HEIGHTS

CLIENT:
SANDEEP & IMMACOLATA BANSAL

NORTH:			FACADE:		SHEET NUMBER: 11.8	JOB NUMBER: 0188MON	
			SCALE: 1 : 200			JOB ISSUE: I	
			DATE: 20.12.22				
REVISIONS	ISSUE	DATE	REVISION DESCRIPTION				INITIALS
	H	20.12.22	B.S RFI & CONTRACT QUOTE AMENDMENT				BL
	I	21.12.22	AMENDED ENEGRY ADDED				BL

